LİSENZİYA

№ 089556

Qeydiyyat nömrəsi İN/L-1542/2016 "30" iyun 2016 il

Azərbaycan Respublikasının İqtisadiyyat Nazirliyi

(lisenziyanı verən dövlət orqanının adı)

Tikintisinə icazə tələb olunan və barəsində məlumatlandırma

(fəaliyyət növü)

icraatı tətbiq olunan bina və qurğuların layihələndirilməsini

_____ həyata keçirməyə icazə verir.

Lisenziya verilib **"STORM BUİLDİNG" Məhdud**

(hüquqi şəxslər üçün - lisenziya verilən hüquqi

Məsuliyyətli Cəmiyyətinə

şəxsin adı və hüquqi ünvanı; fiziki şəxslər üçün - adı, atasının adı, soyadı, şəxsiyyət

Bakı şəhəri, Suraxanı rayonu, AB yaşayış sahəsi

vəsiqəsinə dair məlumat (seriya, nömrə, kim tərəfindən və nə vaxt verilmişdir, ünvanı)

(Yeni Günəşli qəsəbəsi), ev 135, mənzil 18, VÖEN 1902748081

Lisenziyanın qüvvədə olduğu müddət **Müddətsiz** il.

Lisenziyanı təsdiq edən məsul şəxs **SAHİB MƏMMƏDOV**

(adı, soyadı)

Vəzifəsi **NAZİR MÜAVİNİ**

(imza)

M.Y.

Azərbaycan Respublikasının İqtisadiyyat Nazirliyi

LİSENZİYANIN ƏLAVƏSİ

Qeydiyyat nömrəsi İN/4-1542/2016/1 "30" iyun 2016 il

Azərbaycan Respublikasının İqtisadiyyat Nazirliyi (Bakı şəhəri, Ü.Hacıbəyli küçəsi 84 (Hökumət evi) tərəfindən "30" iyun 2016 il tarixində İN/4-1542/2016 qeydiyyat nömrəsi ilə verilmiş lisenziya əsasında **"STORM BUİLDİNG" Məhdud Məsuliyyətli Cəmiyyətinə** (hüquqi ünvanı: Bakı şəhəri, Suraxanı rayonu, AB yaşayış sahəsi (Yeni Günəşli qəsəbəsi), ev 135, mənzil 18, VÖEN 1902748081) tikintisinə icazə tələb olunan və barəsində məlumatlandırma icraatı tətbiq olunan bina və qurğuların layihələndirilməsi fəaliyyəti üzrə görülməsinə icazə verilən işlərin

SİYAHISI

2.1. bina və qurğuların memarlıq layihələndirilməsi
2.2. memarlıq abidələrinin bərpası
3. İnşaat konstruksiyalarının layihələndirilməsi
4.2. avtomobil yolları
4.4. körpülər və yolötürücüləri
4.6. magistral boru kəmərləri
4.7. rezervuarlar
6.3. elektrik təchizatı sistemləri
6.4. istilik təchizatı sistemləri
6.5. su təchizatı və kanalizasiya sistemləri
6.6. qaz təchizatı sistemləri
6.7. rabitə, radio və televiziya şəbəkələri və sistemləri
6.8. ventilyasiya və kondisionerləşdirmə sistemləri
6.9. soyuqluq təchizatı sistemləri
6.10. avtomatlaşdırma və nəzarət-ölçü cihazları
6.11. yanğın-mühafizə siqnalizasiyası və avtomatlaşdırılmış yanğınsöndürmə sistemləri
7.1. korroziyaya qarşı mühafizə tədbirlərinin layihələndirilməsi
7.2. tikintinin təşkilinin layihələndirilməsi
7.3. smetaların tərtib edilməsi

Azərbaycan Respublikası
iqtisadiyyat nazirinin müavini **Sahib Məmmədov**

A Z Ə R B A Y C A N R E S P U B L İ K A S I

"S T O R M B U İ L D İ N G"

M ə h d u d M ə s u l i y y ə t l i C ə m i y y ə t

ABŞERON RAYONU,QOBU QƏSƏBƏSİNDƏ YERLƏŞƏN TORPAQ SAHƏSİNDƏ
TİKİNTİSİ NƏZƏRDƏ TUTULAN ANBAR VƏ İNZİBATİ BİNASI

MEMARLIQ HƏLLİ

İŞÇİ LAYİHƏ

(Anbar və inzibati bina)

B a k ı - 2 0 2 6

AZƏRBAYCAN RESPUBLİKASI

"STORM BUİLDİNG"

Məhdud Məsuliyyətli Cəmiyyət

ABŞERON RAYONU,QOBU QƏSƏBƏSİNDƏ YERLƏŞƏN TORPAQ SAHƏSİNDƏ
TİKİNTİSİ NƏZƏRDƏ TUTULAN ANBAR VƏ İNZİBATİ BİNASI

MEMARLIQ HƏLLİ

İŞÇİ LAYİHƏ
(Anbar binası)

Direktor: A.Cahangiroğlu

L.B.M: G.Musayeva

Bakı-2026

"MH" əsas komplektlərinin işçi cizgilərinin cədvəli

Vərəq	Adı	Qeyd
1	Ümumi məlumatlar	
2	Mövqe planı	
3	Anbar və inzibati binanın ±0.000 səviyyəsinin planı	
4	±0.000 səviyyəsinin planı	
5	±0.000 səviyyəsinin divar markalanması (hörgü planı)	
6	±0.000 səviyyəsinin bəzək planı	
7	Damın planı	
8	Kəsik 1-1	
9	Kəsik 2-2	
10	Fasad 12-4	
11	Fasad 4-12	
12	Fasad A*-E*	
13	Fasad E*-A*	
14	Döşəmə və divarın təsnifatı	
15	Qapı və pəncərələrin spesifikasiyası	

ÜMUMİ GÖSTƏRİŞLƏR

- ± 0.00 NİSBİ YÜKSƏKLİYİ 1-Cİ MƏRTƏBƏNİN DÖŞƏMƏSİNİN ÜSTÜ QƏBUL EDİLMİŞDİR ;
Tikinti rayonu IV B KLİMATİK RAYON
QAR YÜKÜ-80 kq/m^2(I RAYON)
KÜLƏK YÜKÜ-73 kq/m^2(VI SİNİF)
- BİNANIN ODADAVAMLILIQ DƏRƏCƏSİ "II" VƏ "III",
KONSTRUKTİV YANĞIN TƏHLÜKƏSİZLİYİ SİNİFİ "C0",
YANĞIN KATEQORİYASI "E" - yə AİDDİR;
ƏSASLI DİVARLARIN BİR-BİRİ İLƏ VƏ SÜTUNLA BİRLƏŞMƏ YERİNDƏ HÖRGÜYƏ HÜNDÜRLÜK BOYU 600 MM-DƏN
BİR 2.130-6C AZ SERİYALI MT-1 TORLARI QOYULMALIDIR.
- BİNANIN XARİCİ DİVARLARI 400 mm ÖLÇÜLÜ MİŞARLANMIŞ ƏHƏNG DAŞI İLƏ HÖRÜLÜR - 787.4 m^2
- BİNANIN MEMARLIQ PLANLAŞDIRMA HƏLLİ TİKİNTİ NORMA VƏ QAYDALARINA UYĞUN HƏLL OLUNUR;
- BİNANIN HÜNDÜRLÜYÜ - 9.14 m;
- ADDIMLAR - 6.0 m;
- AŞIRIMLAR - 6.0 m
- FASADLAR SEMENT-QUM MƏHLULU İLƏ SUVANIR VƏ ATMOSFER TƏSİRLƏRİNƏ DAVAMLI YÜKSƏK KEYFİYYƏTLİ SUYA DAVAMLI FASAD BOYASI İLƏ ÜZLƏNİR.
- ANTİSEYMİK TƏDBİRLƏR AZDTN 2.3-1-in TƏLƏBLƏRİNƏ ƏSASƏN İŞLƏNMƏLİDİR;
- TİKİNTİ İŞLƏRİ YERİNƏ YETİRİLƏRKƏN TƏHLÜKƏSİZLİK NORMALARINA RİAYƏT OLUNMALIDIR;
- ƏRAZİNİN SEYSMİKLİYİ 8_2 BAL - DIR.
Layihələndirilən binalarının təyinatı qeyri-ərzaqdır.

İSTİNAD OLUNAN VƏ QOŞMA SƏNƏDLƏRİN CƏDVƏLİ

İŞARƏ	ADI	QEYD
"AzDTN 2.6-1"	ŞƏHƏRLƏRİN VƏ QƏSƏBƏLƏRİN KƏND YAŞAYIŞ MƏNTƏQƏLƏRİNİN PLANLAŞDIRILMASI	
"AzDTN 2.8-1"	"ANBAR BINALARI. LAYİHƏLƏNDİRMƏ NORMALARI"	
"AzDTN 2.3-1"	"SEYSMİK RAYONLARDA TİKİNTİ" (Dəyişiklik - №2)	
"AzDTN 2.22-1"	DAM ÖRTÜKLƏRİ. LAYİHƏLƏNDİRMƏ NORMALARI	
"СНиП 2.08.02-89"	ОБЩЕСТВЕННЫЕ ЗДАНИЯ И СООРУЖЕНИЯ	
"МСН 2.02-01-97"	ПОЖАРНАЯ БЕЗОПАСНОСТЬ ЗДАНИЙ И СООРУЖЕНИЙ	
"СНиП 2.03.11-85*"	ЗАЩИТА СТРОИТЕЛЬНЫХ КОНСТРУКЦИЙ ОТ КОРРОЗИИ	
"СН 245-71"	САНИТАРНЫЕ НОРМЫ ПРОЕКТИРОВАНИЯ ПРОМЫШЛЕННЫХ ПРЕДПРИЯТИЙ	

Layihənin işçi cizgiləri, bina və qurğuların istismarı zamanı ətraf mühitin mühafizəsini, partlayış və yanğın təhlükəsizliyini təmin edən tədbirləri nəzərdə tutan mövcud layihə norma və qaydalarına uyğun olaraq yerinə yetirilmişdir.

LBM: / G. Musayeva/

ƏSAS TEXNİKİ - İQTİSADİ GÖSTƏRİCİLƏR

sıra sayı	Adı		Qeyd
1	Tikilinin ümumi sahəsi m^2	1122	
2	Tikinti sahəsi m^2	1181	
3	Mərtəbənin sayı	1	
4	Həcmi m^3	10180.22	

Dəyiş.	Sah.sayı	Vərəq	İnv.№	İmza	Tarix
LBM		G.Musayeva			
Memar		G.Abdullayeva			
Yoxladı		S.Şükürova			

Sifarişçi: Cəfərov Mədət İslam oğlu

Abşeron rayonu, Qobu qəsəbəsində yerləşən torpaq sahəsində tikintisi nəzərdə tutulan anbar və inzibati binası

Anbar binası	mərhələ	vərəq	vərəqlər
	İ.L	1	15
Ümumi məlumatlar	"STORM BUİLDİNG" MMC		

Razılaşdırılıb


İnv.№-si əvəzinə

İmza və tarix

Əsasın inv.№-si

A3



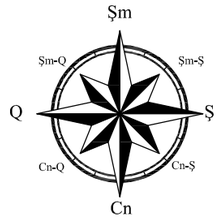

Razılaşdırılıb

İnv.№ əvəzinə

İmza və tarix

İnv.№ əslin

Dəyiş.	Sh.sən	Vərəq	İnv.№	İmza	Tarix
LBM		G.Musayeva			
Memar		G.Abdullayeva			
Yoxladı		S.Şükürova			

Sifarişçi: Cəfərov Mədət İslam oğlu


Abşeron rayonu, Qobu qəsəbəsində yerləşən torpaq sahəsində tikintisi nəzərdə tutulan anbar və inzibati binası

Anbar binası	Mərhələ	Vərəq	Vərəqlər
	İ.L	2	15
Mövqe planı	"STORM BUİLDİNG" MMC		


AZƏRBAYCAN RESPUBLİKASI MƏHDUD MƏSULİYYƏTLİ CƏMİYYƏTİ STORM BUİLDİNG

A3

Anbar və inzibati binanın ±0.000 səviyyəsinin planı

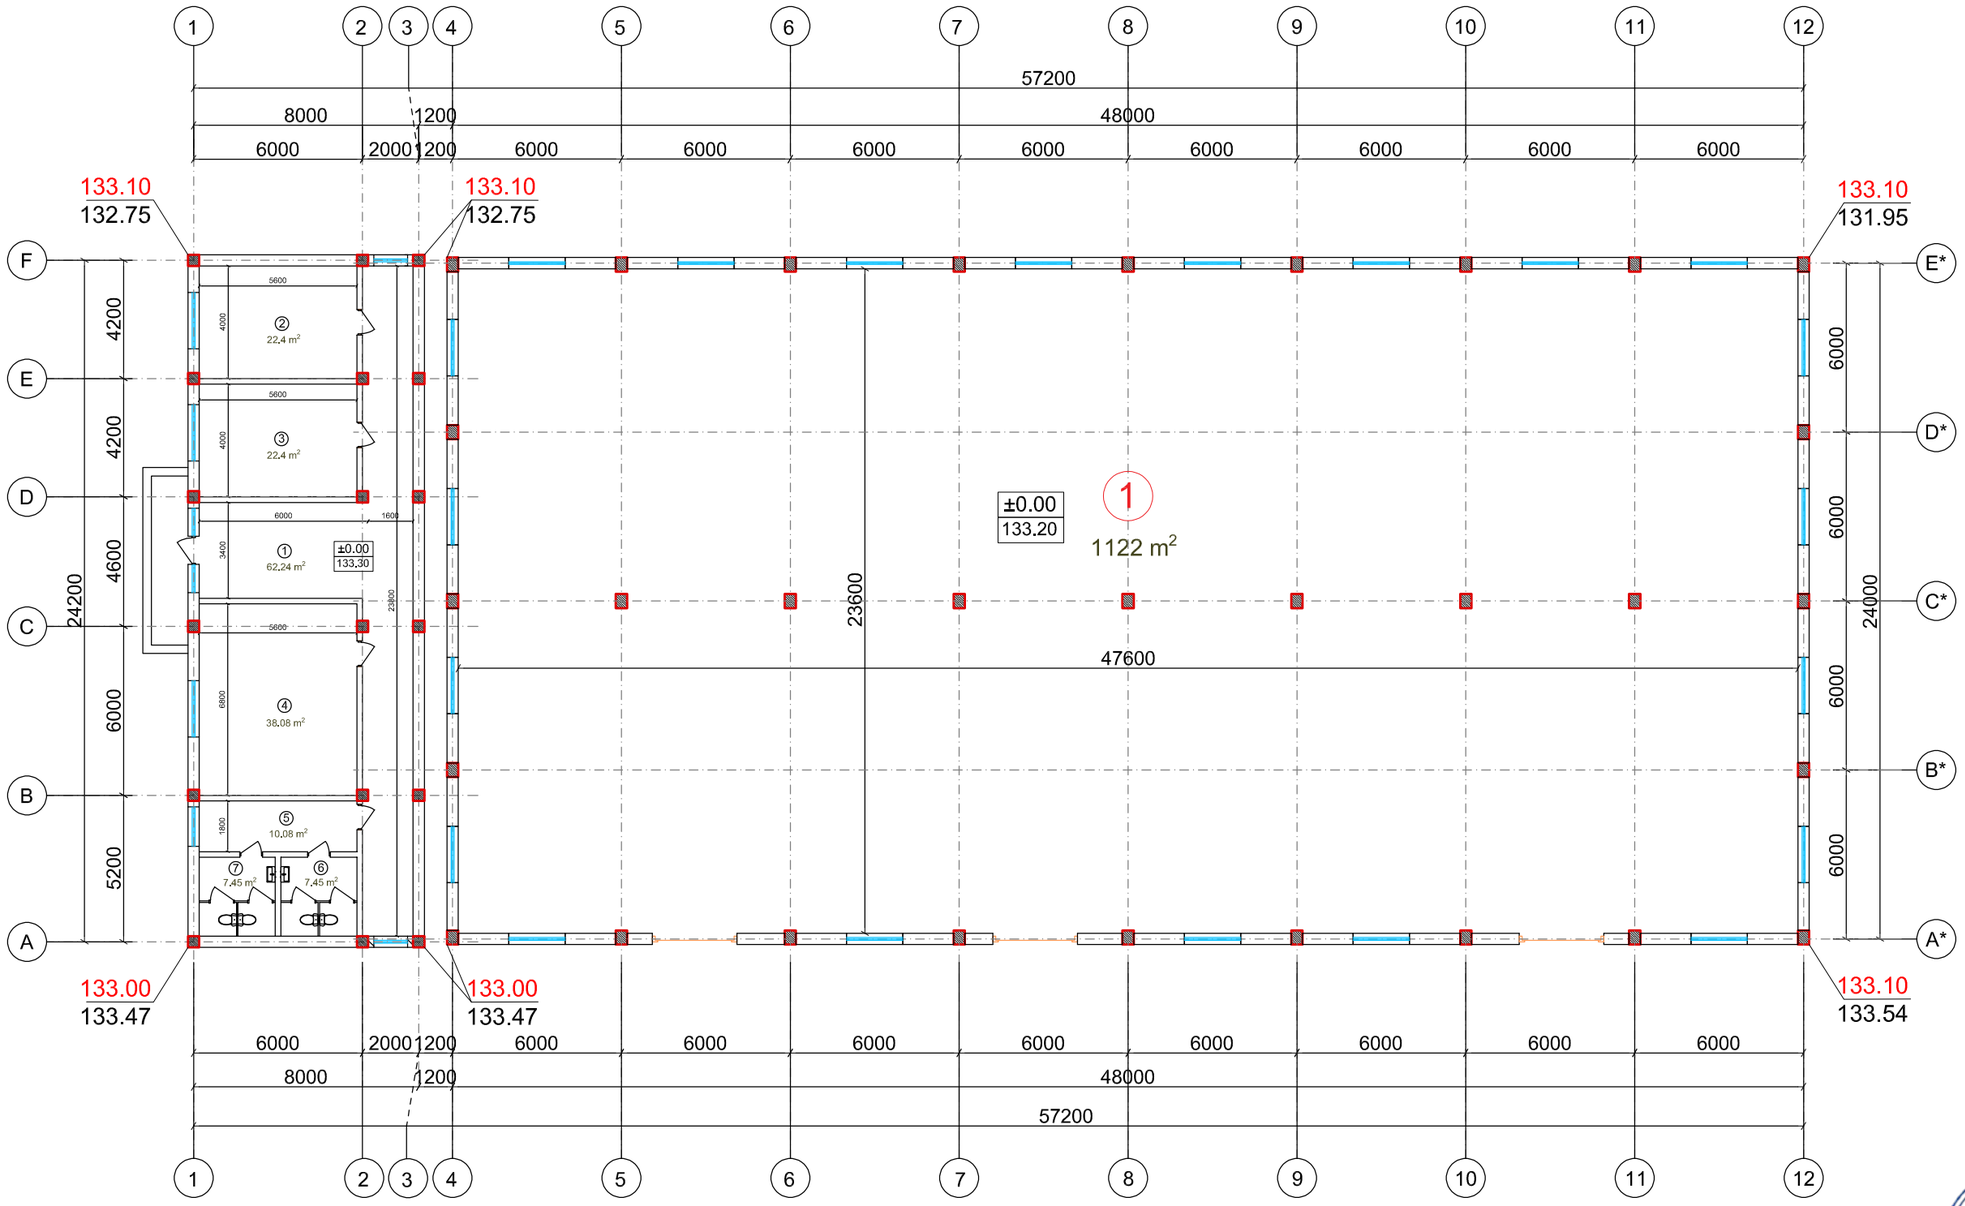

Bloklaşma sxemi

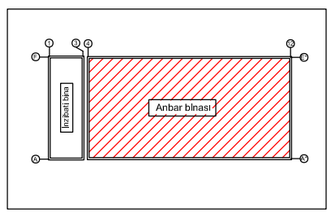

Dəyiş.	Sh.sən	Vərəq	İnv.№	İmza	Tarix
LBM		G.Musayeva			
Memar		G.Abdullayeva			
Yoxladı		S.Şükürova			

Sifarişçi: Cəfərov Mədət İslam oğlu

Abşeron rayonu, Qobu qəsəbəsində yerləşən torpaq sahəsində tikintisi nəzərdə tutulan anbar və inzibati binası

Anbar binası

Mərhələ	Vərəq	Vərəqlər
İ.L	3	15

Anbar və inzibati binanın ±0.000 səviyyəsinin planı

"STORM BUİLDİNG" MMC

A3


Razılaşdırılıb

İnv.№ əvəzinə

İmza və tarix

İnv.№ əslin


±0.000 səviyyəsinin planı

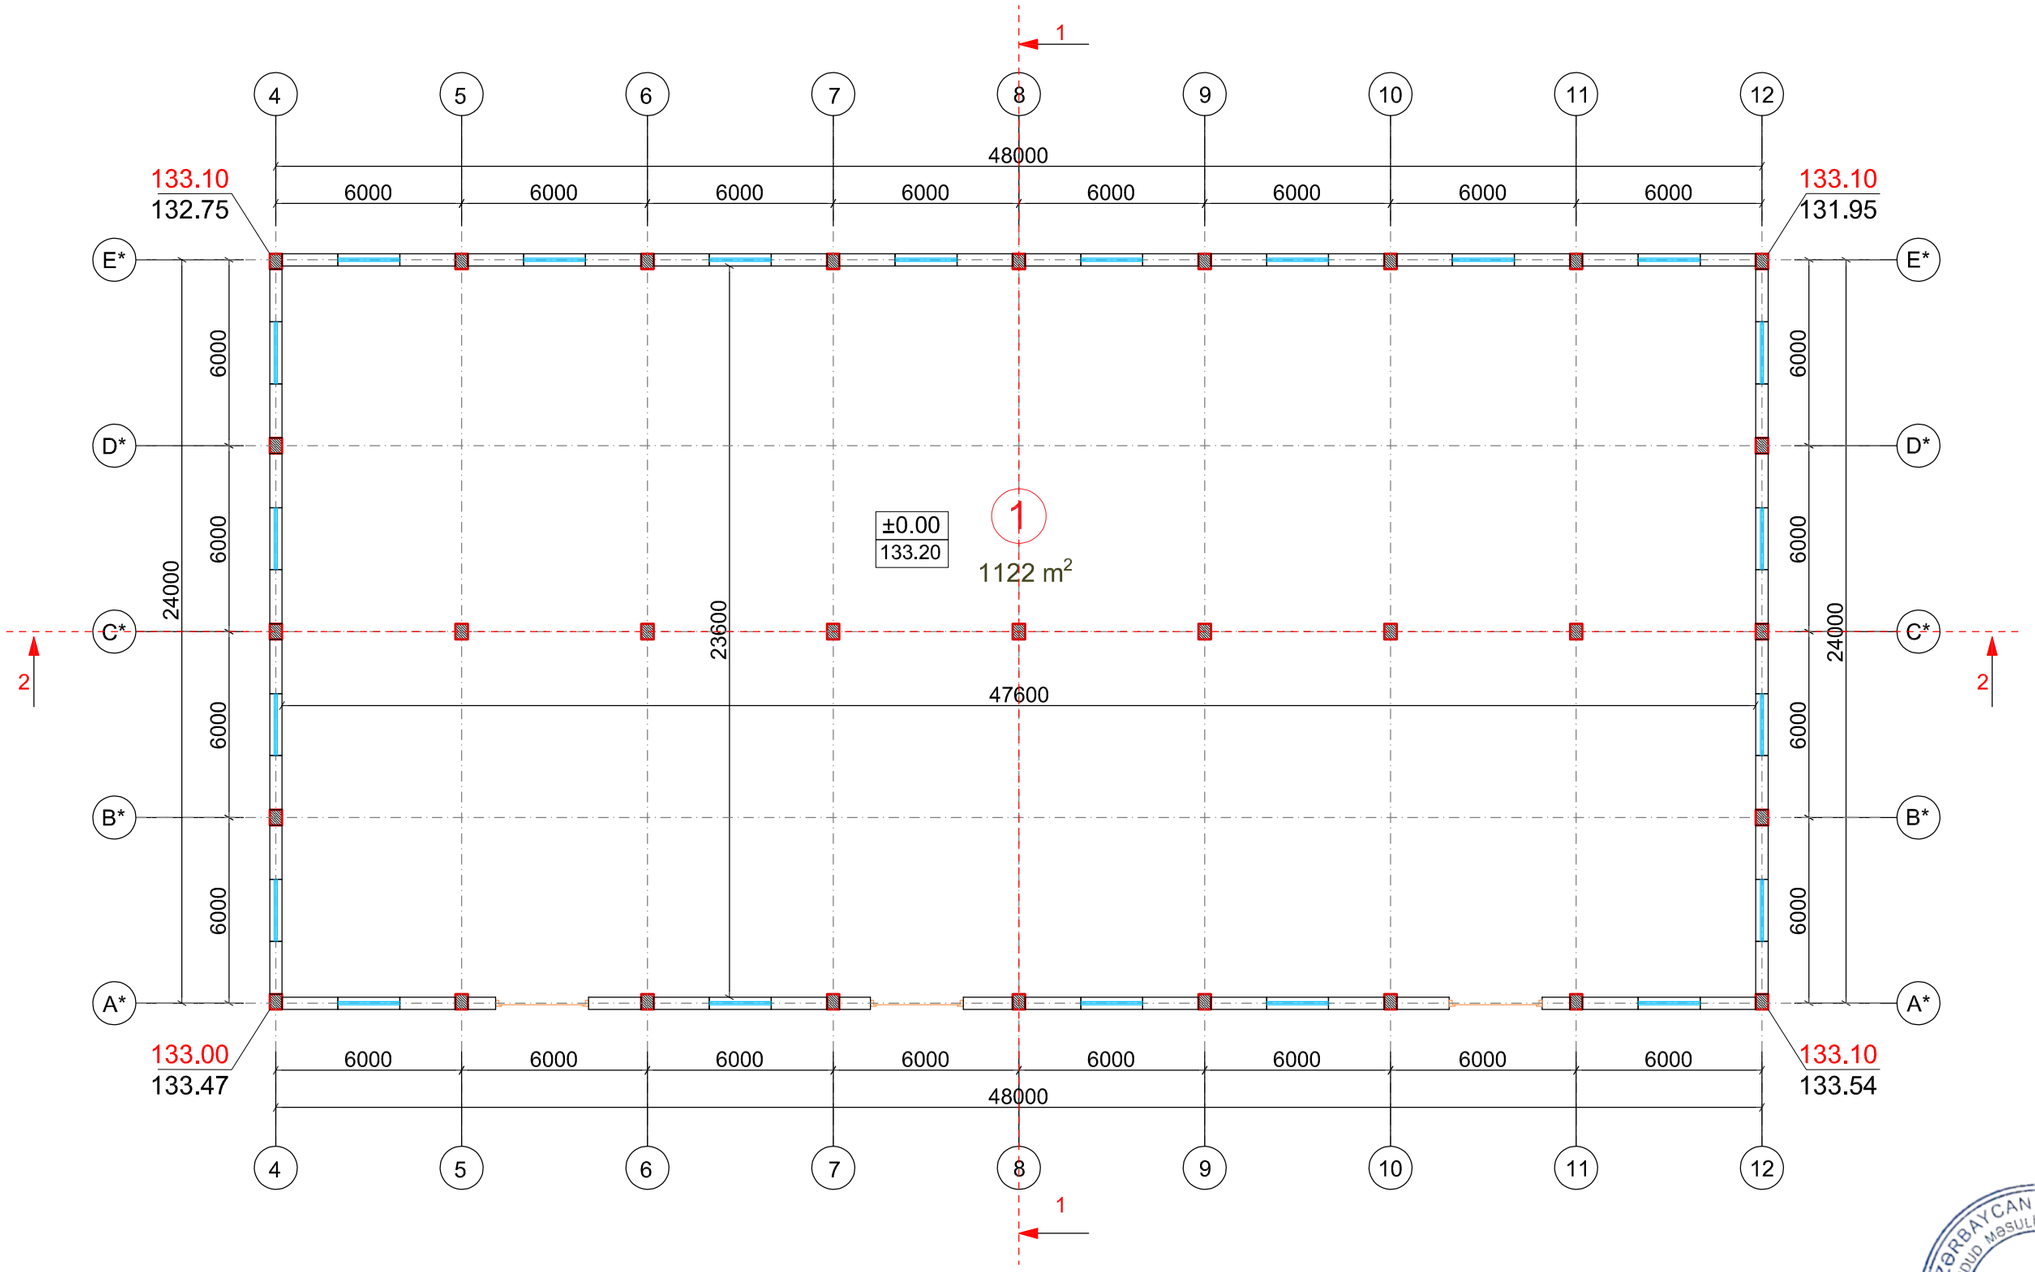

YERLƏŞQƏLƏRİN EKSPLİKASİYASI

Otağın nömrəsi	Adı	Sahəsi (m^2)	Otağın kateqoriyası
1	Anbar sahəsi	1 122	

Bloklaşma sxemi

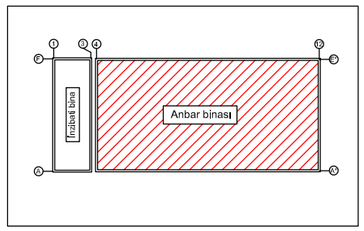

Dəyiş.	Sh.sən	Vərəq	İnv.№	İmza	Tarix
LBM		G.Musayeva			
Memar		G.Abdullayeva			
Yoxladı		S.Şükürova			

Sifarişçi: Cəfərov Mədət İslam oğlu

Abşeron rayonu, Qobu qəsəbəsində yerləşən torpaq sahəsində tikintisi nəzərdə tutulan anbar və inzibati binası

Anbar binası	Mərhələ	Vərəq	Vərəqlər
	İ.L	4	15
±0.000 səviyyəsinin planı	"STORM BUİLDİNG" MMC		

AZƏRBAYCAN RESPUBLİKASI MƏHDUD MƏSULİYYƏTLİ CƏMİYYƏTİ STORM BUİLDİNG

A3


Razılaşdırılıb

İnv.№ əvəzinə

İmza və tarix

İnv.№ əslin


±0.000 səviyyəsinin divar markalanması (hörgü planı)

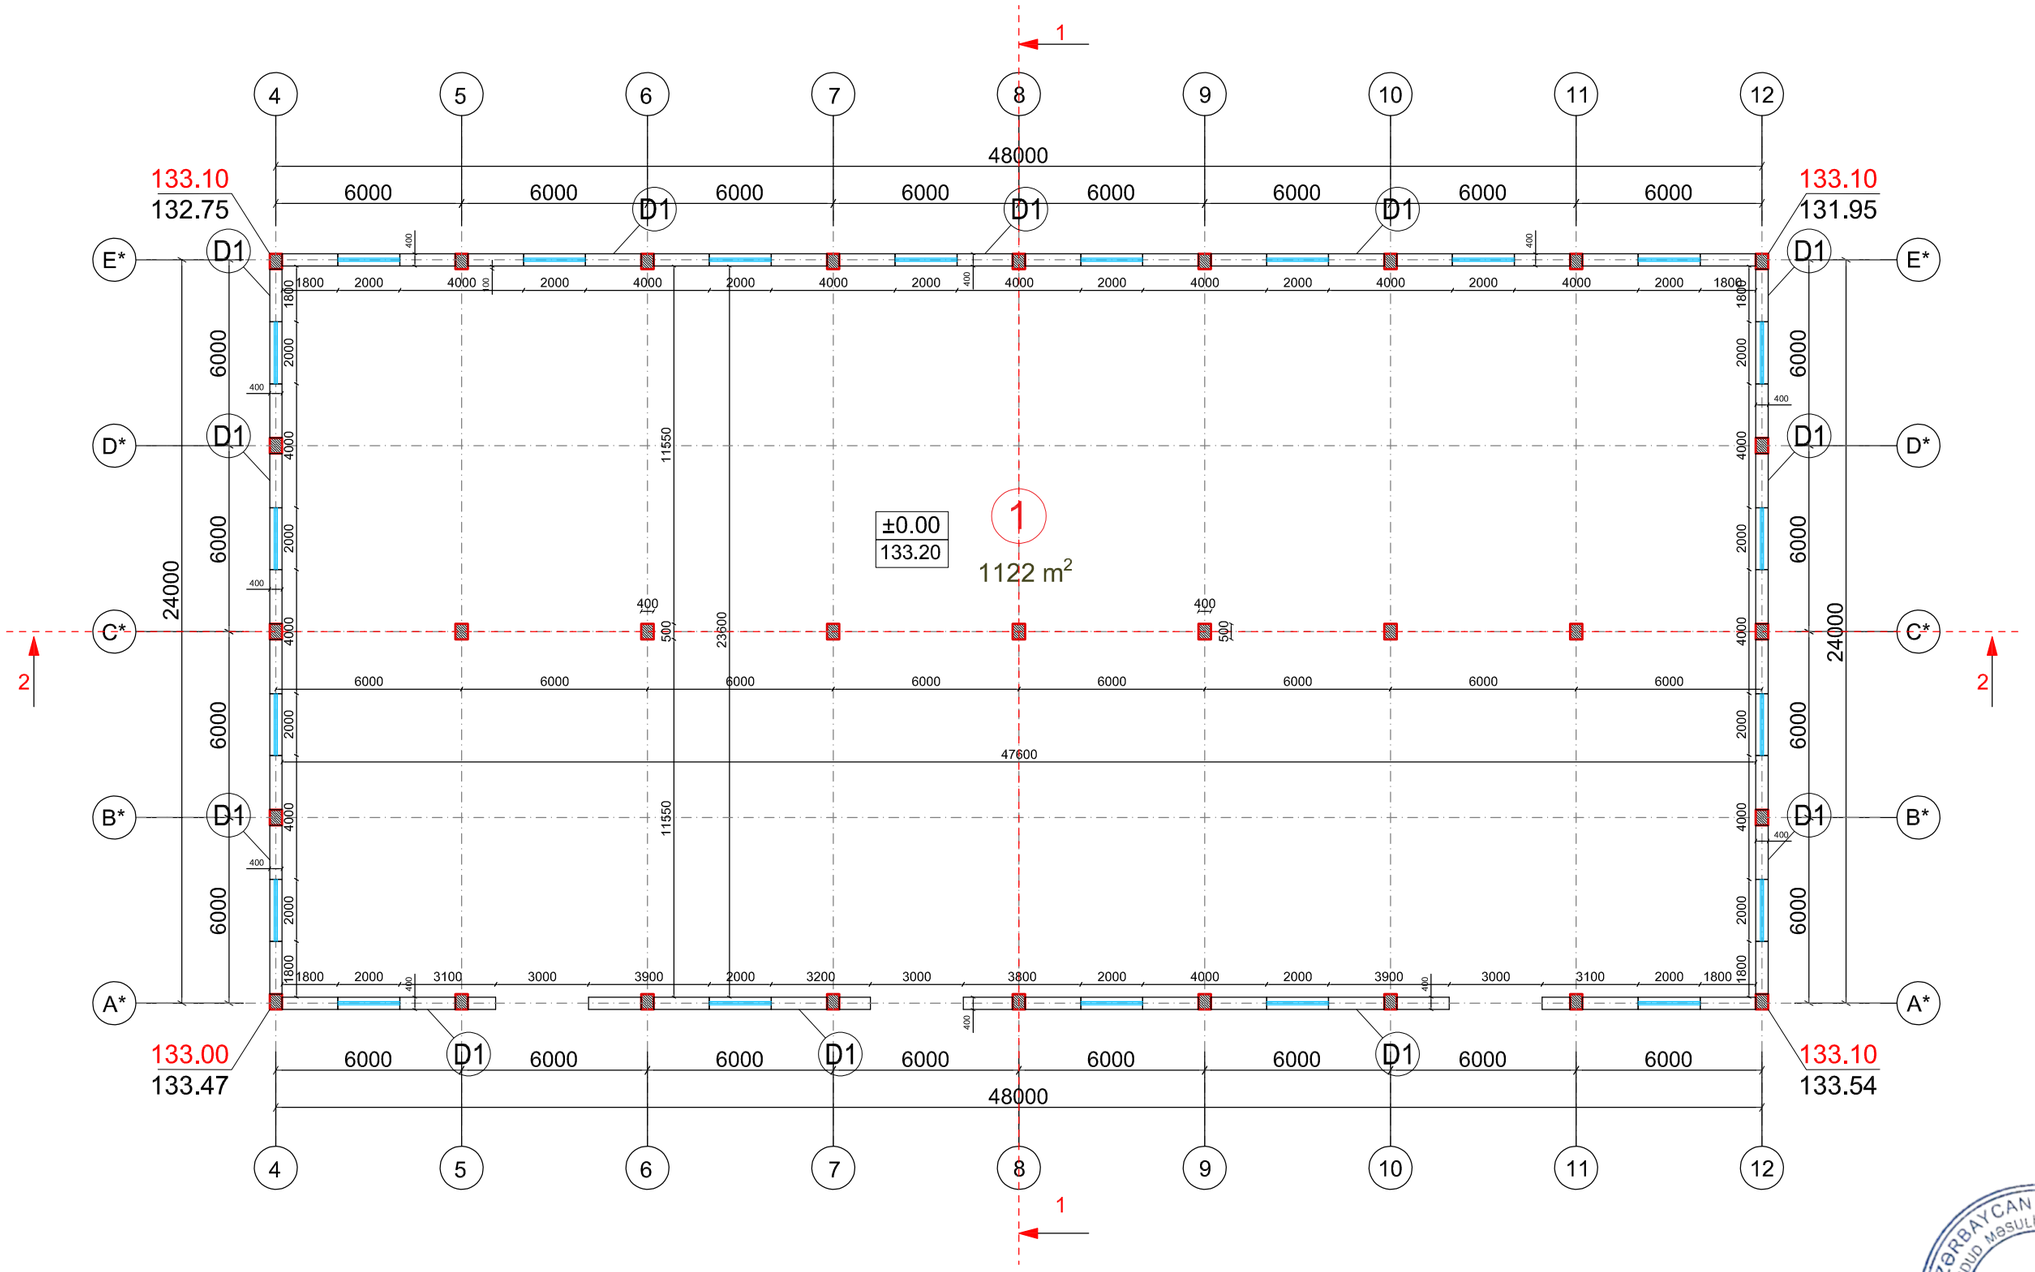

Tikinti işlərinin cədvəli

№	Adları	Eni (m)	Uzunluğu (m)	Hündürlüyü (m)	Ölçü vahidi (m^2)
D1	Xarici divarların (mişarlanmış əhəng daşı) quraşdırılması	0.4	124.4	6.6	787.4

Bloklaşma sxemi

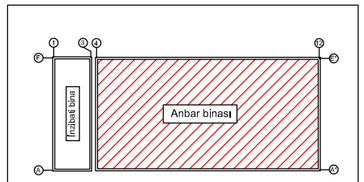

Dəyiş.	Sh.sən	Vərəq	İnv.№	İmza	Tarix
LBM		G.Musayeva			
Memar		G.Abdullayeva			
Yoxladı		S.Şükürova			

Sifarişçi: Cəfərov Mədət İslam oğlu

Abşeron rayonu, Qobu qəsəbəsində yerləşən torpaq sahəsində tikintisi nəzərdə tutulan anbar və inzibati binası

Anbar binası	Mərhələ	Vərəq	Vərəqlər
	İ.L	5	15
±0.000 səviyyəsinin divar markalanması (hörgü planı)	"STORM BUİLDİNG" MMC		

A3


İnv.№ əvəzinə

İmza və tarix

İnv.№ əslin

Razılaşdırılıb


±0.000 səviyyəsinin bəzək planı

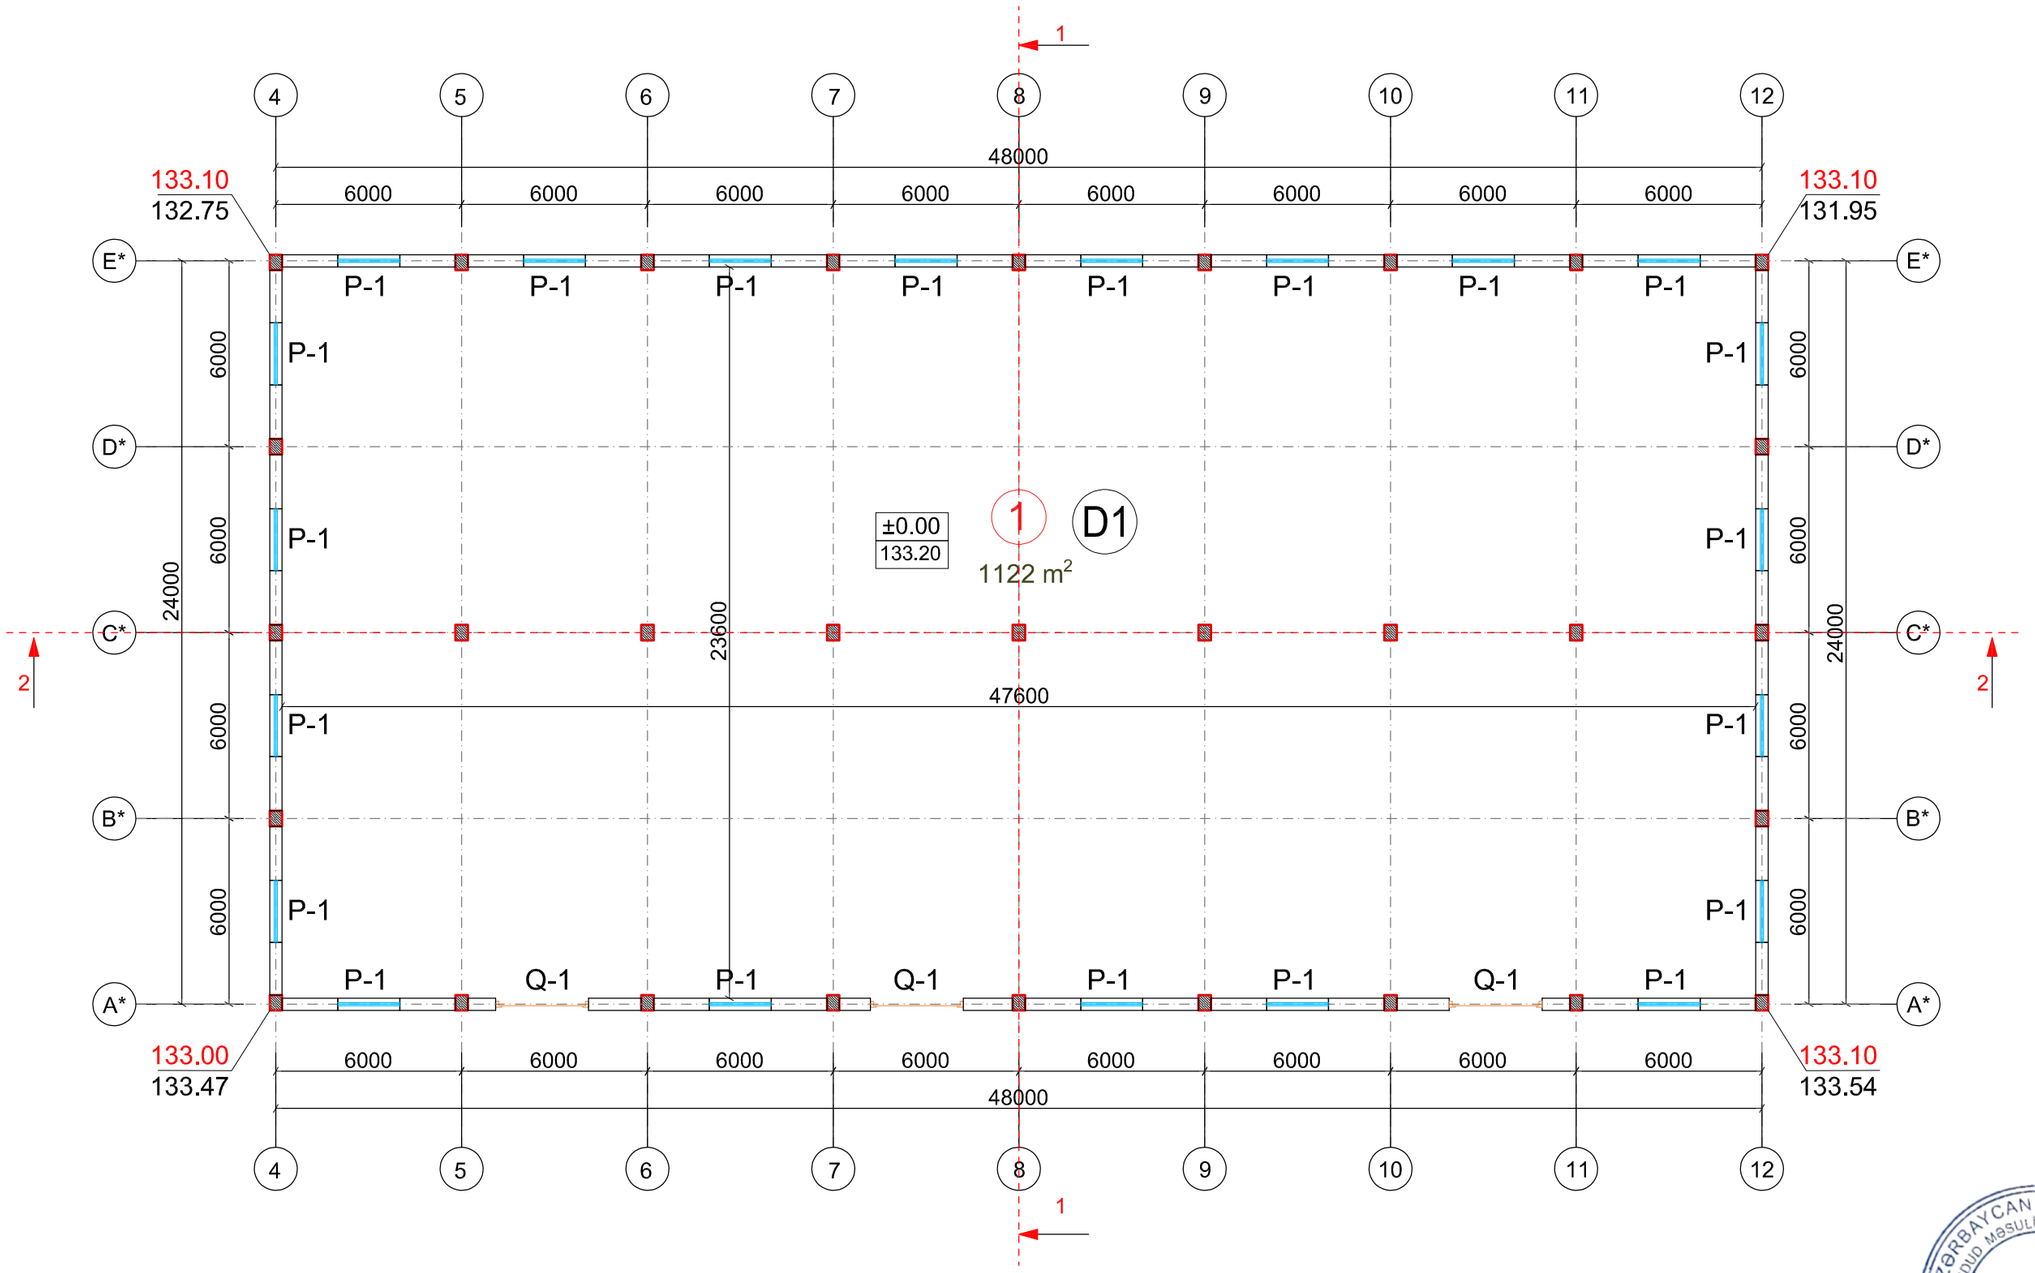

YERLƏŞQƏLƏRİN EKSPLİKASİYASI

Otağın nömrəsi	Adı	Sahəsi (m^2)	Otağın kateqoriyası
1	Anbar sahəsi	1 122	

Bloklaşma sxemi

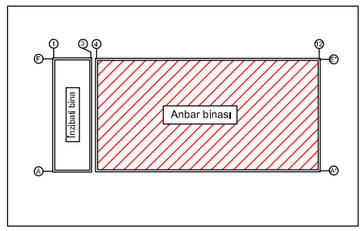

Dəyiş.	Sh.sən	Vərəq	İnv.№	İmza	Tarix
LBM		G.Musayeva			
Memar		G.Abdullayeva			
Yoxladı		S.Şükürova			

Sifarişçi: Cəfərov Mədət İslam oğlu

Abşeron rayonu, Qobu qəsəbəsində yerləşən torpaq sahəsində tikintisi nəzərdə tutulan anbar və inzibati binası

Anbar binası	Mərhələ	Vərəq	Vərəqlər
	İ.L	6	15
±0.000 səviyyəsinin bəzək planı	"STORM BUİLDİNG" MMC		

A3


Razılaşdırılıb

İnv.№ əvəzinə

İmza və tarix


İnv.№ əslin

Damın planı

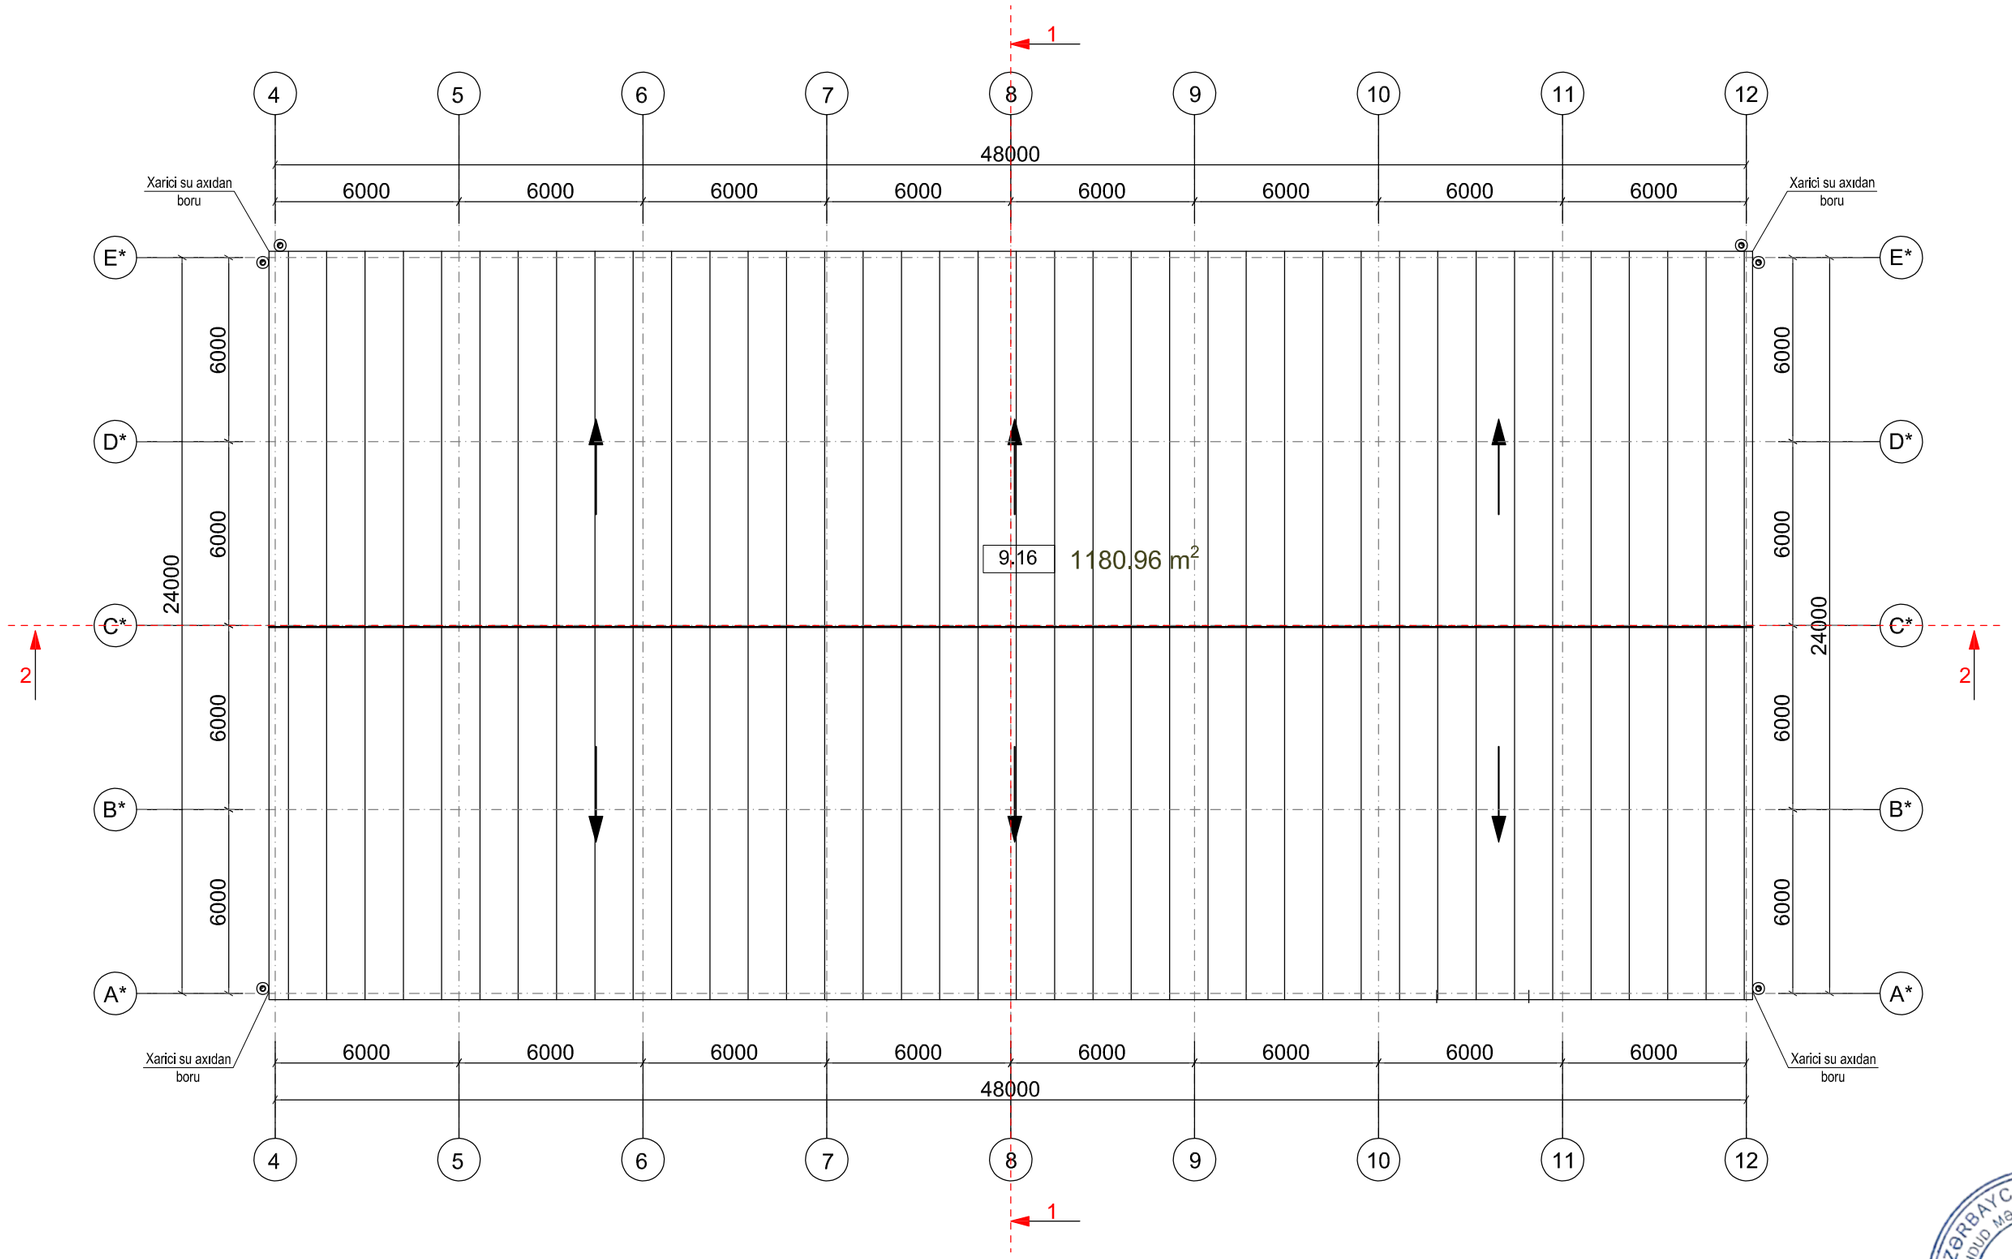

Mövqe	Materialların Təsnifatı			
	Adı	Ölçü vahidi	Miqdarı 1 ədəd üçün	Miqdarı bina üzrə
1	Boru Ø100	m		45
2	Dirsək Ø100	ədəd		6
3	Su qəbul edici qıf	ədəd	1	6
4	Metal xamut 100x150	ədəd		60

Bloklaşma sxemi

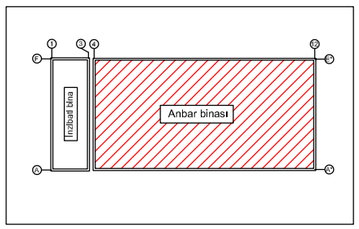

Dəyiş.	Sh.sən	Vərəq	İnv.№	İmza	Tarix
LBM		G.Musayeva			
Memar		G.Abdullayeva			
Yoxladı		S.Şükürova			

Sifarişçi: Cəfərov Mədət İslam oğlu

Abşeron rayonu, Qobu qəsəbəsində yerləşən torpaq sahəsində tikintisi nəzərdə tutulan anbar və inzibati binası

Anbar binası	Mərhələ	Vərəq	Vərəqlər
	İ.L	7	15
Damın planı	"STORM BUİLDİNG" MMC		

AZƏRBAYCAN RESPUBLİKASI STORM BUİLDİNG MƏHDUD MƏSULİYYƏTLİ CƏMİYYƏTİ

A3


Razılaşdırılıb

İnv.№ əvəzinə


İmza və tarix

İnv.№ əslin

Kəsik 1-1

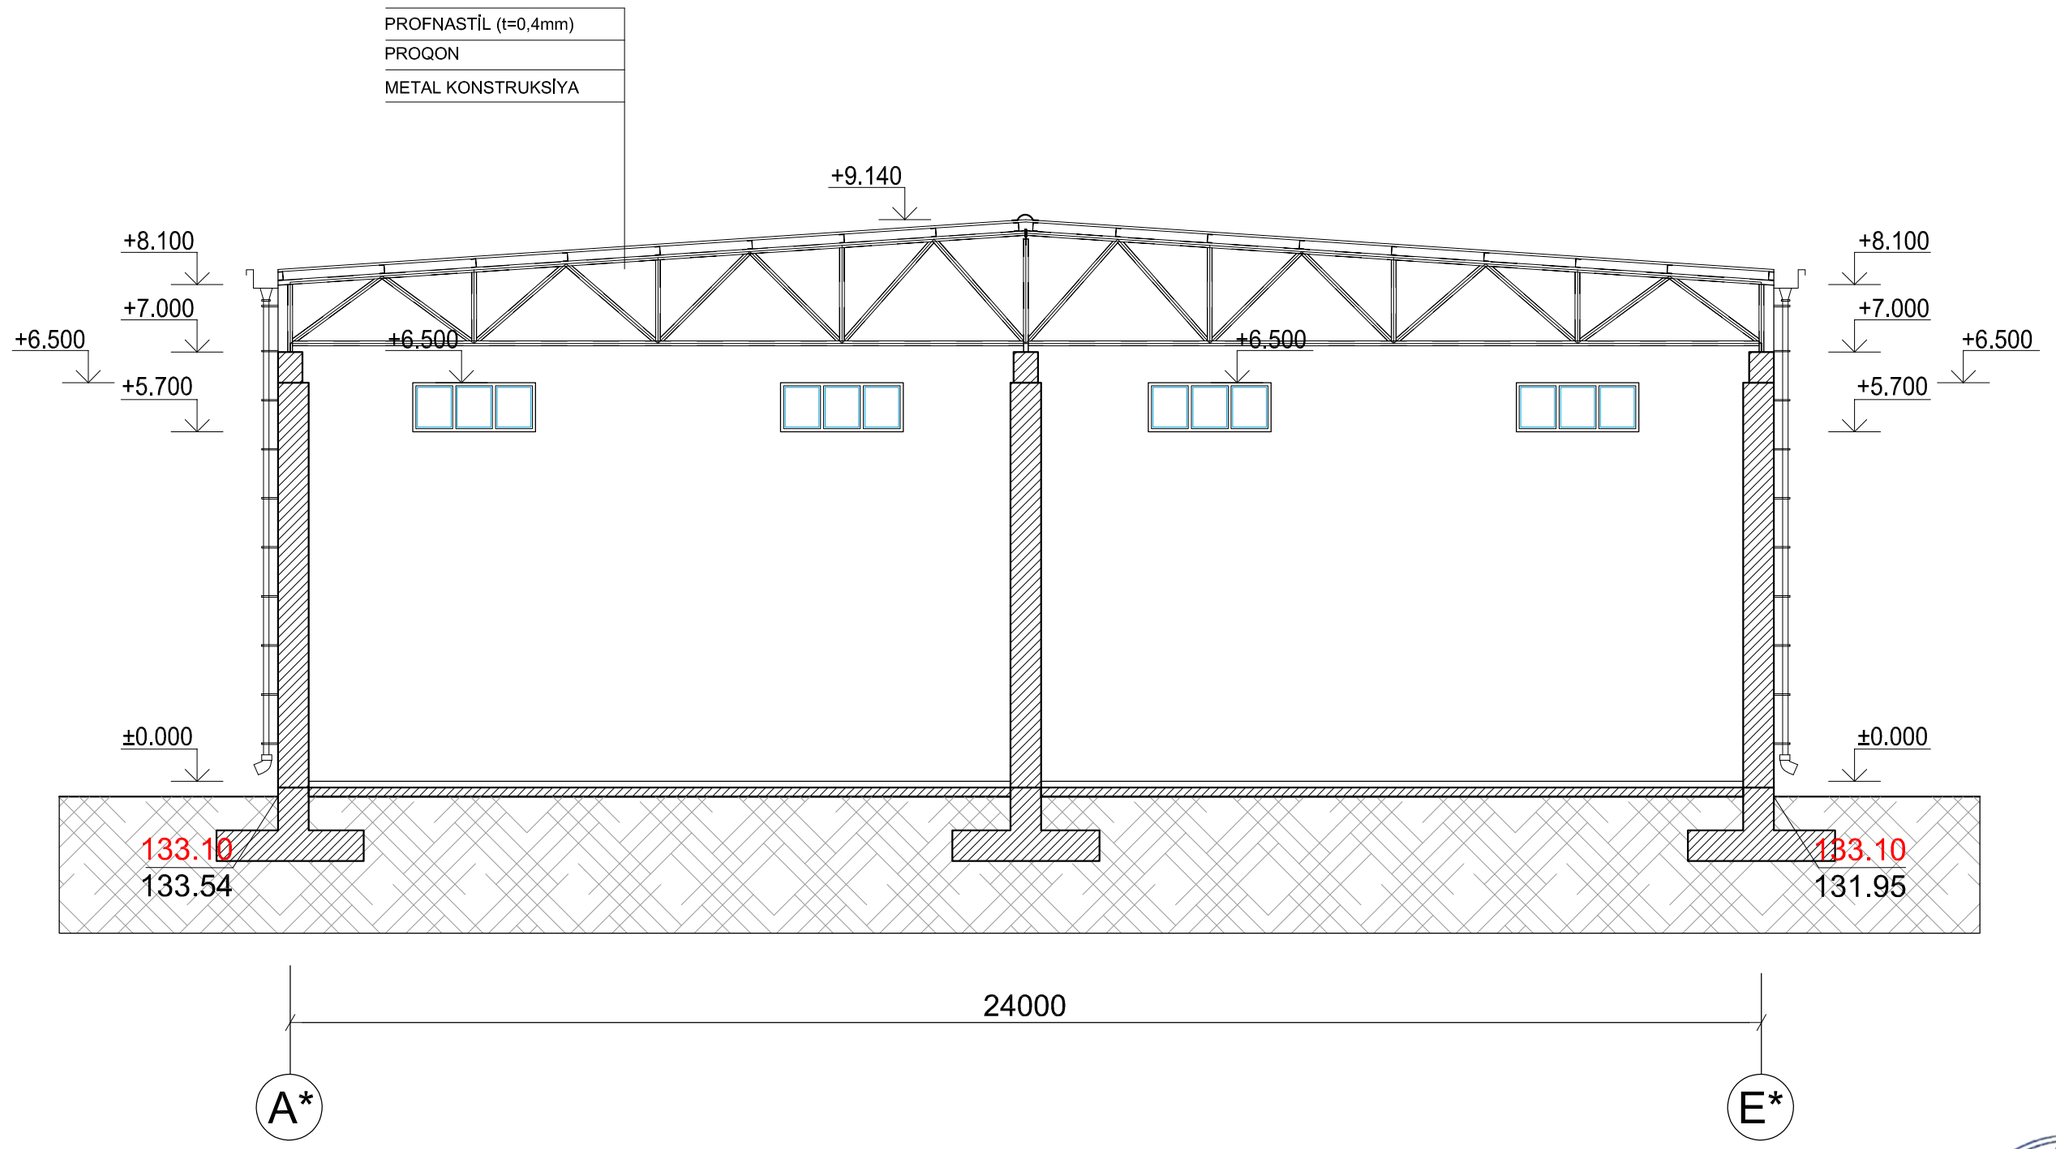

Bloklaşma sxemi

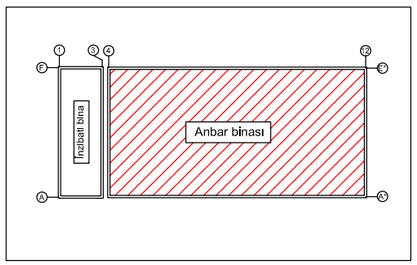

Dəyiş.	Sh.sən	Vərəq	İnv.№	İmza	Tarix
LBM		G.Musayeva			
Memar		G.Abdullayeva			
Yoxladı		S.Şükürova			

Sifarişçi: Cəfərov Mədət İslam oğlu

Abşeron rayonu, Qobu qəsəbəsində yerləşən torpaq sahəsində tikintisi nəzərdə tutulan anbar və inzibati binası

Anbar binası	Mərhələ	Vərəq	Vərəqlər
	İ.L	8	15
Kəsik 1-1	"STORM BUİLDİNG" MMC		

STORM BUİLDİNG

A3


Razılaşdırılıb

İnv.№ əvəzinə


İmza və tarix

İnv.№ əslin

Kəsik 2-2

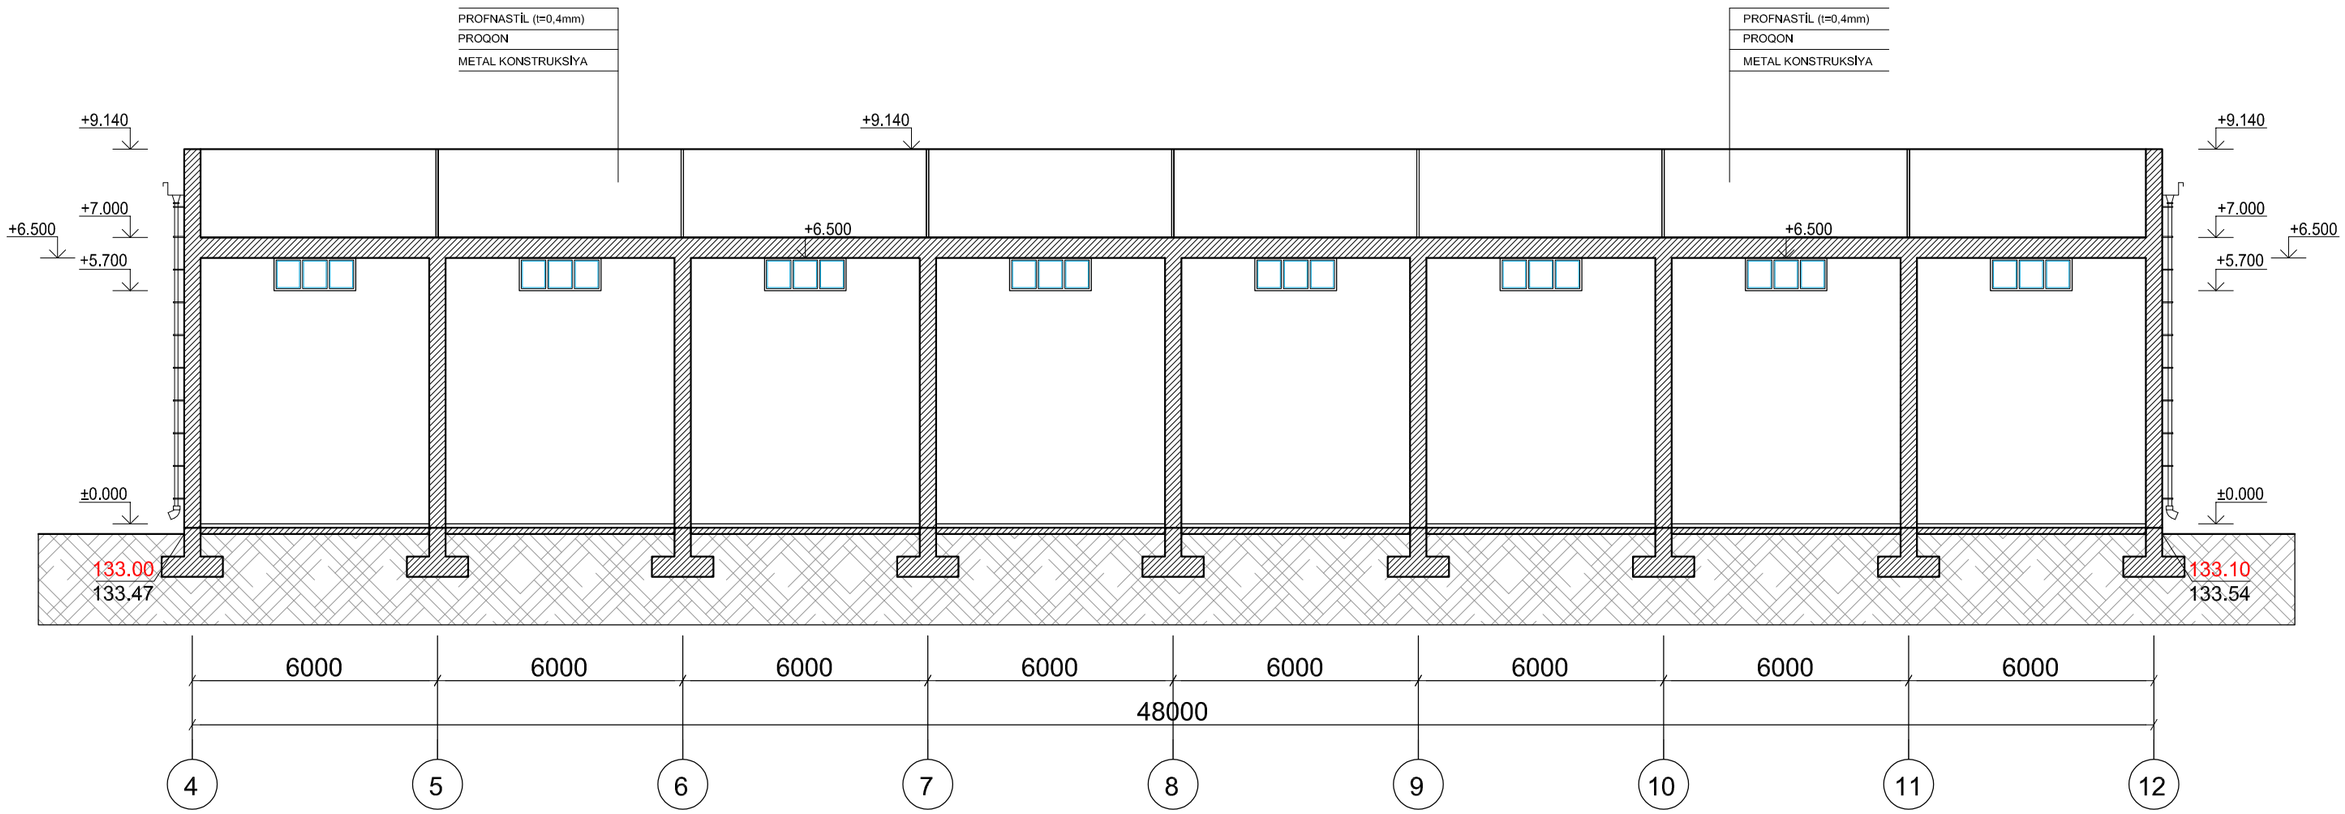

Bloklaşma sxemi

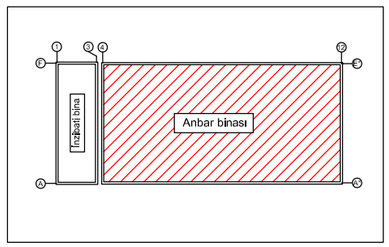

Dəyiş.	Sh.sən	Vərəq	Inv.№	İmza	Tarix
LBM		G.Musayeva			
Memar		G.Abdullayeva			
Yoxladı		S.Şükürova			

Sifarişçi: Cəfərov Mədət İslam oğlu

Abşeron rayonu, Qobu qəsəbəsində yerləşən torpaq sahəsində tikintisi nəzərdə tutulan anbar və inzibati binası

Anbar binası

Mərhələ	Vərəq	Vərəqlər
İ.L	9	15

Kəsik 2-2

"STORM BUİLDİNG" MMC

STORM BUİLDİNG

A3


Razılaşdırılıb

İnv.№ əvəzinə

İmza və tarix

İnv.№ əslin

Fasad 12-4

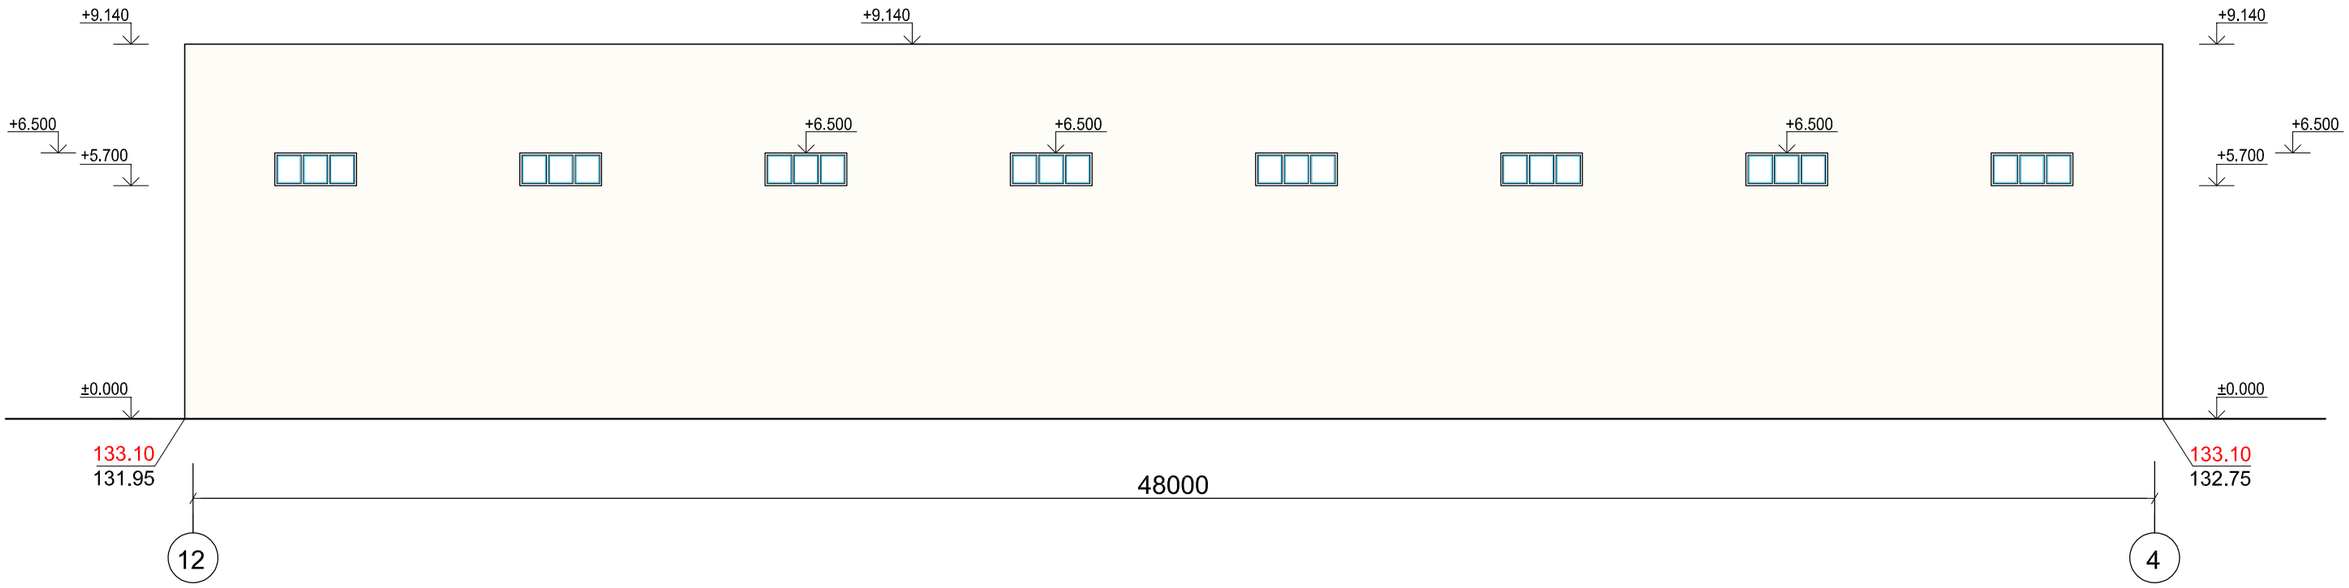

Razılaşdırılıb

İnv.№ əvəzinə


İmza və tarix

İnv.№ əsilin

Fasad materiallarının spesifikasiyası

Fasad materiallarının adı	Sahə m^2	Düyün
1. Mişarlanmış əhəng daşı 2. Suvaq 3. 3 qat boya	430.6	

Bloklaşma sxemi

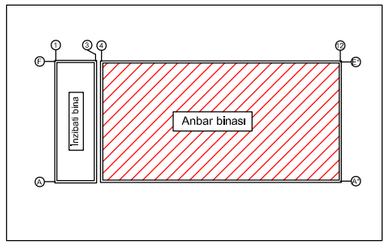

Dəyiş.	Sh.sən	Vərəq	Inv.№	İmza	Tarix
LBM		G.Musayeva			
Memar		G.Abdullayeva			
Yoxladı		S.Şükürova			


Sifarişçi: Cəfərov Mədət İslam oğlu

Abşeron rayonu, Qobu qəsəbəsində yerləşən torpaq sahəsində tikintisi nəzərdə tutulan anbar və inzibati binası

Anbar binası	Mərhələ	Vərəq	Vərəqlər
	İ.L	10	15
Fasad 12-4	"STORM BUİLDİNG" MMC		

A3


Fasad 4-12

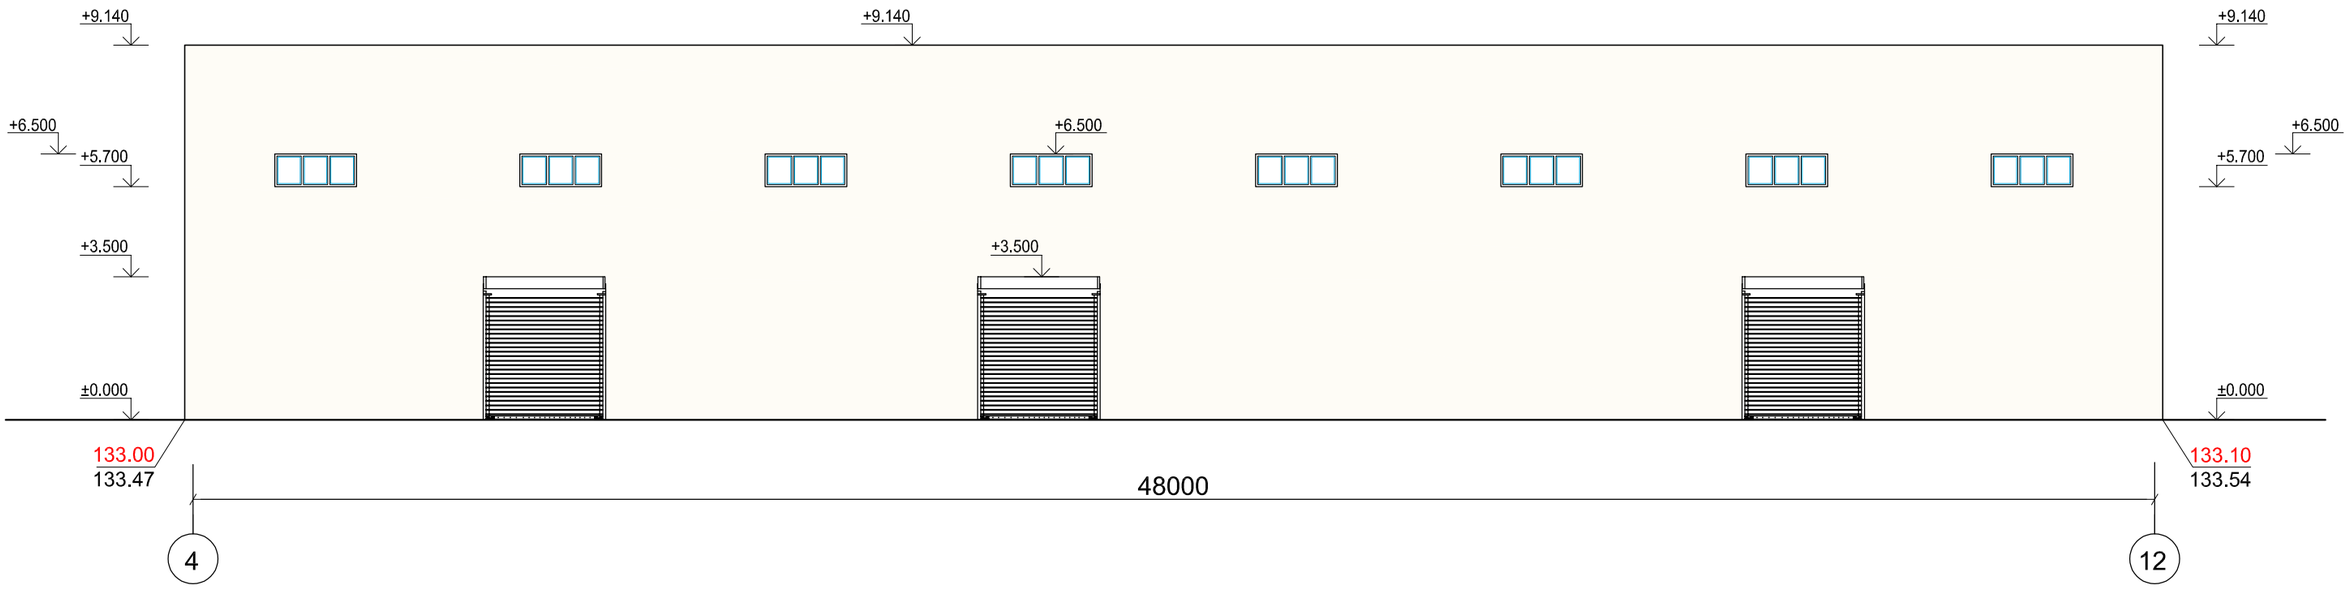

Fasad materiallarının spesifikasiyası

Fasad materiallarının adı	Sahə m^2	Düyün
1. Mişarlanmış əhəng daşı 2. Suvaq 3. 3 qat boya	400.0	

Bloklaşma sxemi

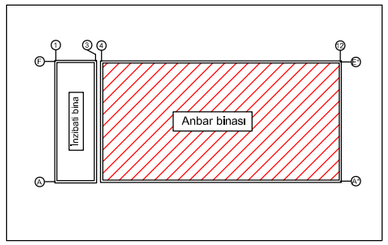

Dəyiş.	Sh.sən	Vərəq	İnv.№	İmza	Tarix
LBM		G.Musayeva			
Memar		G.Abdullayeva			
Yoxladı		S.Şükürova			

Sifarişçi: Cəfərov Mədət İslam oğlu

Abşeron rayonu, Qobu qəsəbəsində yerləşən torpaq sahəsində tikintisi nəzərdə tutulan anbar və inzibati binası

Anbar binası	Mərhələ	Vərəq	Vərəqlər
	İ.L	11	15
Fasad 4-12	"STORM BUİLDİNG" MMC		

A3


Razılaşdırılıb

İnv.№ əvəzinə

İmza və tarix

İnv.№ əslin


Fasad A*-E*

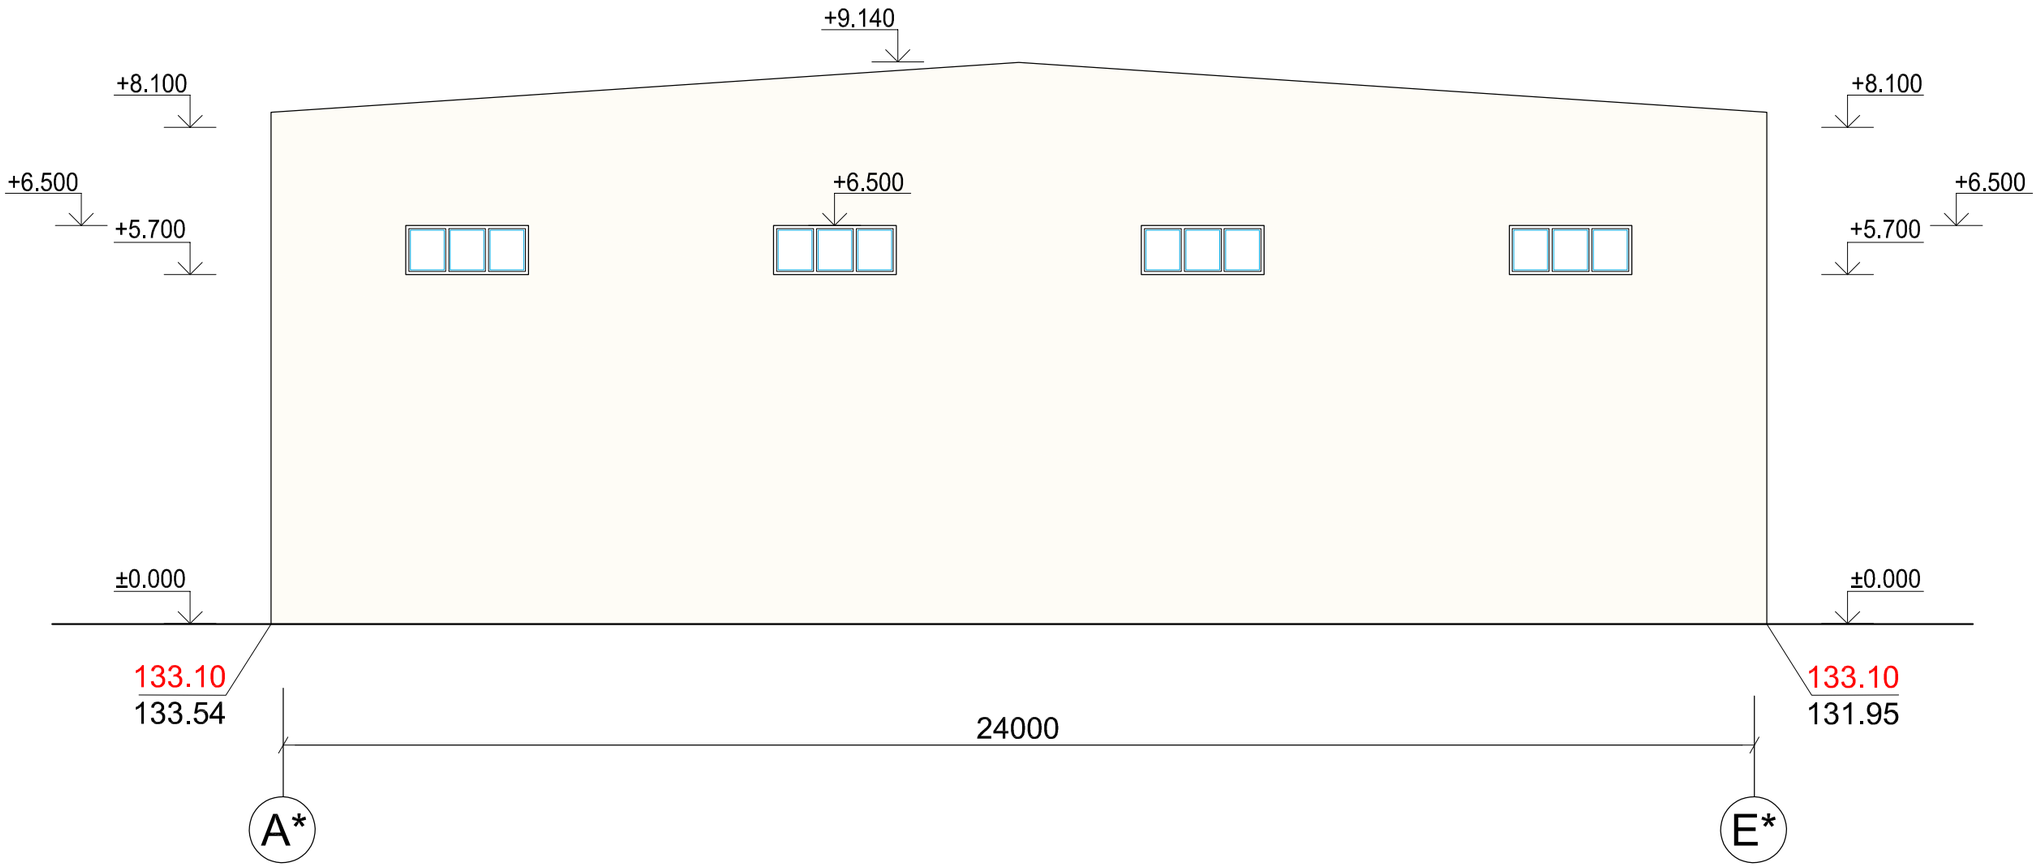

Fasad materiallarının spesifikasiyası

Fasad materiallarının adı	Sahə m^2	Düyün
1. Mişarlanmış əhəng daşı 2. Suvaq 3. 3 qat boya	207.2	

Bloklaşma sxemi

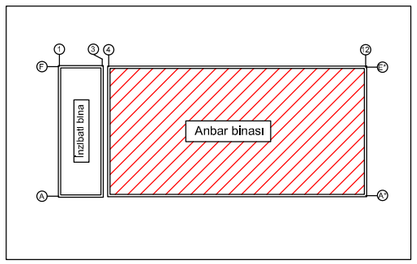

Dəyiş.	Sh.sən	Vərəq	Inv.№	İmza	Tarix
LBM		G.Musayeva			
Memar		G.Abdullayeva			
Yoxladı		S.Şükürova			

Sifarişçi: Cəfərov Mədət İslam oğlu

Abşeron rayonu, Qobu qəsəbəsində yerləşən torpaq sahəsində tikintisi nəzərdə tutulan anbar və inzibati binası

Anbar binası	Mərhələ	Vərəq	Vərəqlər
	İ.L	12	15
Fasad A*- E*	"STORM BUİLDİNG" MMC		

A3


Razılaşdırılıb

İnv.№ əvəzinə

İmza və tarix

İnv.№ əslin


Fasad E*-A*

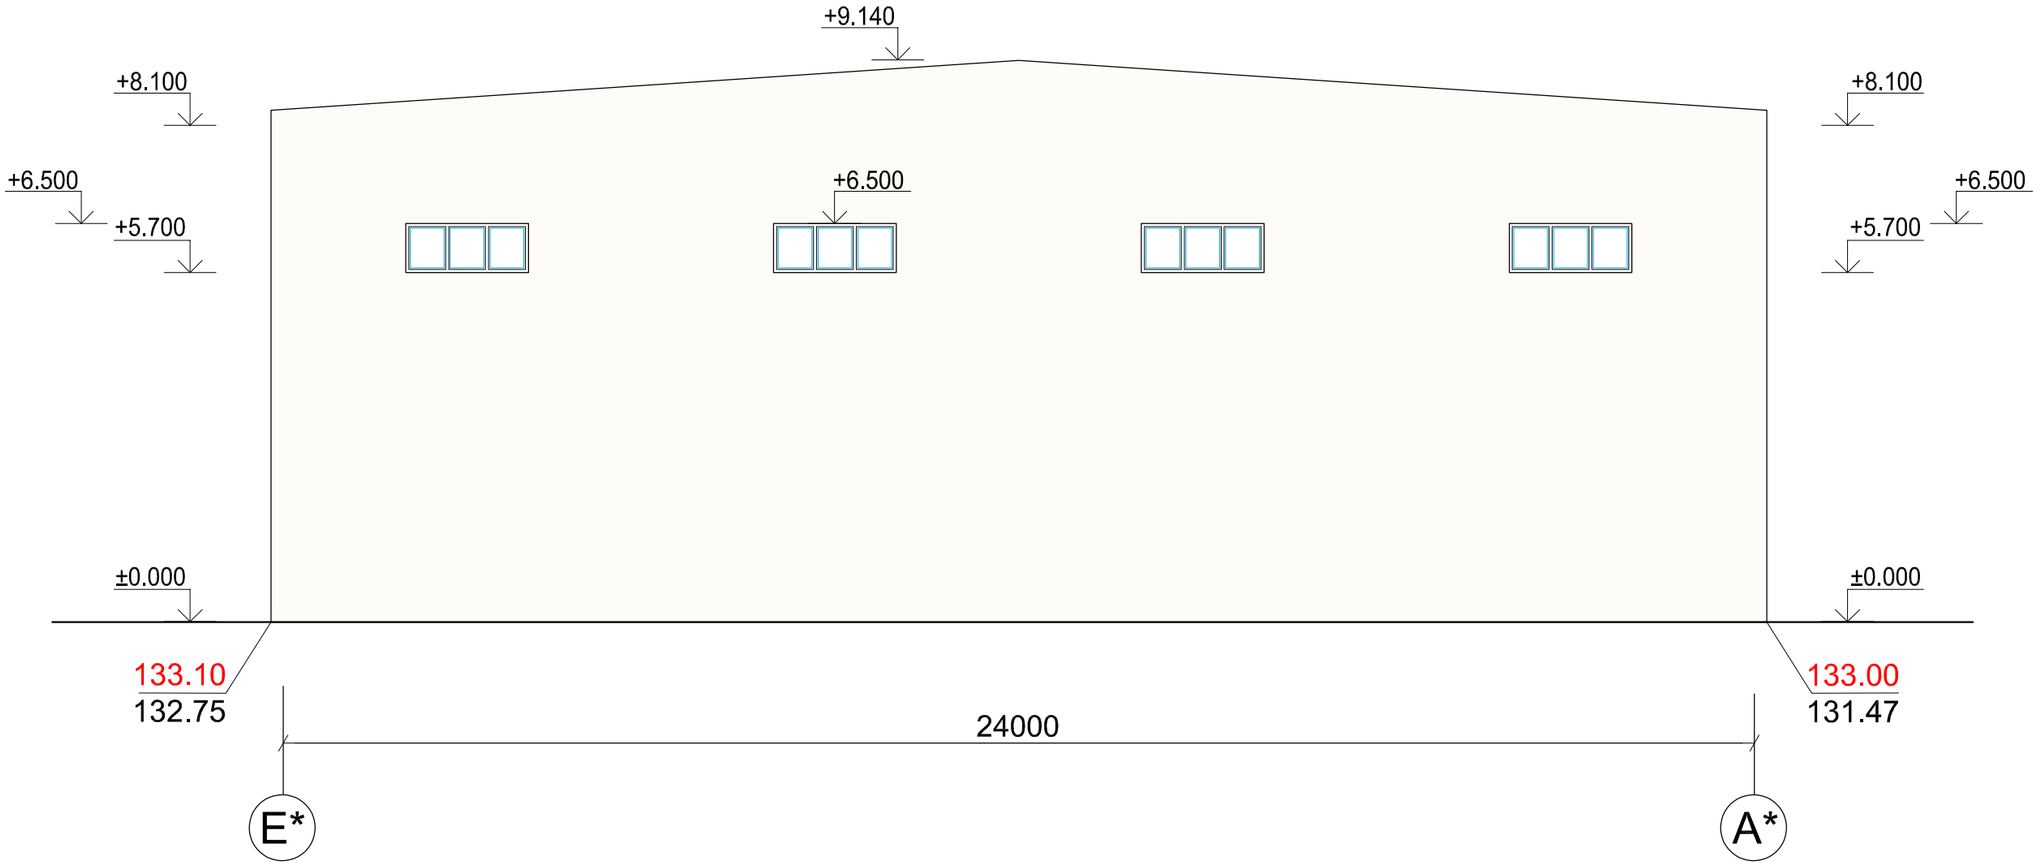

Fasad materiallarının spesifikasiyası

Fasad materiallarının adı	Sahə m^2	Düyün
1. Mişarlanmış əhəng daşı 2. Suvaq 3. 3 qat boya	207.2	

Bloklaşma sxemi

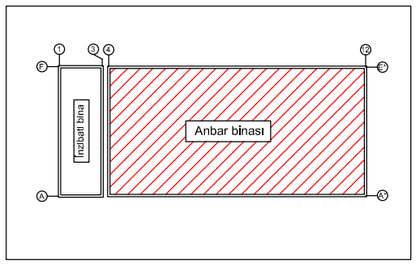

Dəyiş.	Sh.sən	Vərəq	Inv.№	İmza	Tarix
LBM		G.Musayeva			
Memar		G.Abdullayeva			
Yoxladı		S.Şükürova			

Sifarişçi: Cəfərov Mədət İslam oğlu

Abşeron rayonu, Qobu qəsəbəsində yerləşən torpaq sahəsində tikintisi nəzərdə tutulan anbar və inzibati binası

Anbar binası	Mərhələ	Vərəq	Vərəqlər
	İ.L	13	15
Fasad E*- A*	"STORM BUİLDİNG" MMC		

A3


Razılaşdırılıb

İnv.№ əvəzinə


İmza və tarix

İnv.№ əslin

Döşəmə və divarın təsnifatı

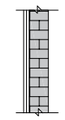		Döşəmə						Divar		
Sıra sayı	Otağın adı və ya nömrəsi	Döşəmə materiallarının adı	Sahə m^2	Həcm m^3	Düyün		Uzunluğu p/m	Divar materiallarının adı	Sahə m^2	Düyün
	±0.000 səviyyəsi									
1	1	**D1** 1.Cilalanmış beton - 50 mm 2.Döşəmə qatı - 150 mm 3.Beton hazırlıq qatı - 100 mm 4.Qırmadaş qatı - 100 mm 5.Karbonat qatı - 500 mm		56.1 168.3 112.2 112.2 561		—	—	**D1** 1. Mişarlanmış əhəng daşı 2. Suvaq 3. Şpatlovka 4. 3 qat boya	787.4	

Bloklaşma sxemi

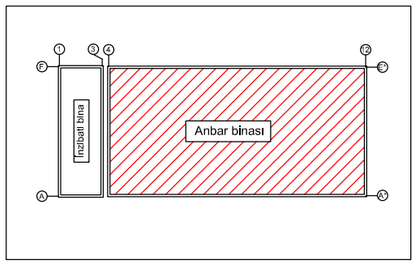

Dəyiş.	Sh.sən	Vərəq	Inv.№	İmza	Tarix
LBM		G.Musayeva			
Memar		G.Abdullayeva			
Yoxladı		S.Şükürova			

Sifarişçi: Cəfərov Mədət İslam oğlu

Abşeron rayonu, Qobu qəsəbəsində yerləşən torpaq sahəsində tikintisi nəzərdə tutulan anbar və inzibati binası

Anbar binası	Mərhələ	Vərəq	Vərəqlər
	İ.L	14	15
Döşəmə və divarın təsnifatı	"STORM BUİLDİNG" MMC		

A3

Razılaşdırılıb

İnv.№ əvəzinə


İmza və tarix

İnv.№ əslin


Qapı və pəncərələrin spesifikasiyası

Mövqe	İşarə	Adı		Sayı	Sahəsi m²	Qeyd
Q-1	Germetik jalüz qapı	Qapı	3000 x 3500 (h)	3	31.5	
P-1	Plastik (PVC) pəncərə	Pəncərə	2000 x 800 (h)	21	33.6	


Q-1 MARKALI QAPI

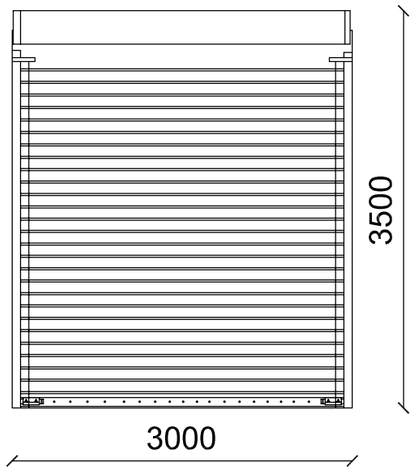

P-1 MARKALI PƏNCƏRƏ

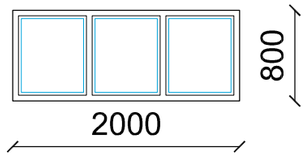

Bloklaşma sxemi

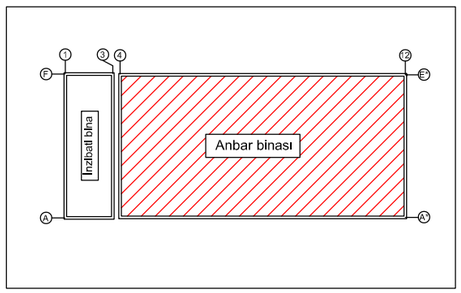

Dəyiş.	Sh.sən	Vərəq	İnv.№	İmza	Tarix
LBM		G.Musayeva			
Memar		G.Abdullayeva			
Yoxladı		S.Şükürova			

Sifarişçi: Cəfərov Mədət İslam oğlu

Abşeron rayonu, Qobu qəsəbəsində yerləşən torpaq sahəsində tikintisi nəzərdə tutulan anbar və inzibati binası

Anbar binası	Mərhələ	Vərəq	Vərəqlər
	İ.L.	15	15
Qapı və pəncərələrin spesifikasiyası	"STORM BUİLDİNG" MMC		

Razılaşdırılıb

İnv.№ əvəzinə

İmza və tarix

İnv.№ əslin

A3

AZƏRBAYCAN RESPUBLİKASI

"STORM BUİLDİNG"

Məhdud Məsuliyyətli Cəmiyyət

ABŞERON RAYONU,QOBU QƏSƏBƏSİNDƏ YERLƏŞƏN TORPAQ SAHƏSİNDƏ
TİKİNTİSİ NƏZƏRDƏ TUTULAN ANBAR VƏ İNZİBATİ BİNASI

MEMARLIQ HƏLLİ

İŞÇİ LAYİHƏ
(İnzibati bina)

Direktor: A.Cahangiroğlu

L.B.M: G.Musayeva

Bakı-2026

"MH" əsas komplektlərinin işçi cizgilərinin cədvəli

Vərəq	Adı	Qeyd
1	Ümumi məlumatlar	
2	Mövqe planı	
3	Anbar və inzibati binanın ±0.000 səviyyəsinin planı	
4	±0.000 səviyyəsinin planı	
5	±0.000 səviyyəsinin divar markalanması (hörgü planı)	
6	±0.000 səviyyəsinin döşəmə markalanması (bəzək planı)	
7	±0.000 səviyyəsinin tavan markalanması (bəzək planı)	
8	±0.000 səviyyəsinin qapı-pəncərə markalanması (bəzək planı)	
9	±0.000 səviyyəsinin mebel planı	
10	Damın planı	
11	Kəsik 1-1	
12	Kəsik 2-2	
13	Fasad F-A; Fasad A-F	
14	Fasad 1-3; Fasad 3-1	
15	Döşəmə, tavan və divarın təsnifatı	
16	Qapı və pəncərələrin spesifikasiyası	

İSTİNAD OLUNAN VƏ QOŞMA SƏNƏDLƏRİN CƏDVƏLİ

İŞARƏ	ADI	QEYD
"AzDTN 2.6-1"	ŞƏHƏRLƏRİN VƏ QƏSƏBƏLƏRİN KƏND YAŞAYIŞ MƏNTƏQƏLƏRİNİN PLANLAŞDIRILMASI	
"AzDTN 2.3-1"	"SEYSMİK RAYONLARDA TİKİNTİ" (Dəyişiklik - №2)	
"СНиП 2.09.04-87"	АДМИНИСТРАТИВНЫЕ И БЫТОВЫЕ ЗДАНИЯ	
"СНиП 2.08.02-89"	ОБЩЕСТВЕННЫЕ ЗДАНИЯ И СООРУЖЕНИЯ	
"МСН 2.02-01-97"	ПОЖАРНАЯ БЕЗОПАСНОСТЬ ЗДАНИЙ И СООРУЖЕНИЙ	
"СНиП 2.03.11-85*"	ЗАЩИТА СТРОИТЕЛЬНЫХ КОНСТРУКЦИЙ ОТ КОРРОЗИИ	
"СН 245-71"	САНИТАРНЫЕ НОРМЫ ПРОЕКТИРОВАНИЯ ПРОМЫШЛЕННЫХ ПРЕДПРИЯТИЙ	

Layihənin işçi cizgiləri, bina və qurğuların istismarı zamanı ətraf mühitin mühafizəsini, partlayış və yanğın təhlükəsizliyini təmin edən tədbirləri nəzərdə tutan mövcud layihə norma və qaydalarına uyğun olaraq yerinə yetirilmişdir.

LBM: / G. Musayeva/

ÜMUMİ GÖSTƏRİŞLƏR

1. ± 0.00 NİSBİ YÜKSƏKLİYİ 1-Cİ MƏRTƏBƏNİN DÖŞƏMƏSİNİN ÜSTÜ QƏBUL EDİLMİŞDİR .
2. BİNANIN ODADAVAMLILIQ DƏRƏCƏSİ "I",
   KONSTRUKTİV YANĞIN TƏHLÜKƏSİZLİYİ SİNİFİ "C0",
   YANĞIN KATEQORİYASI "B" - yə AİDDİR;
3. BİNANIN BÜTÜN YÜKGÖTÜRƏN KONSTRUKSİYALARI MONOLİT DƏMİR-BETONDAN İBARƏTDİR.
   - BÜNÖVRƏ - MONOLİT DƏMİR-BETON (LENTVARİ).
   - KARKASIN ELEMENTLƏRİ (SÜTUNLAR, RİGEL, ÖRTÜK TAVASI,) MONOLİT DƏMİR-BETONDANDIR.
4. ƏSASLI DİVARLARIN BİR-BİRİ İLƏ VƏ SÜTUNLA BİRLƏŞMƏ YERİNDƏ HÖRGÜYƏ HÜNDÜRLÜK BOYU 600 MM-DƏN
   BİR 2.130-6C AZ SERİYALI MT-1 TORLARI QOYULMALIDIR.
5. BİNANIN XARİCİ DİVARLARI 400 mm ÖLÇÜLÜ MİŞARLANMIŞ ƏHƏNG DAŞI İLƏ HÖRÜLÜR - 187.73 m^2;
6. DAXİLİ ARAKƏSMƏLƏR 50 mm VƏ 200 mm ÖLÇÜLÜ YÜNGÜL BOŞLUQLU KƏRPİCLƏ 50 MARKALI SEMENT QUM MƏHLULU İLƏ HÖRÜLÜR.
   - 50 mm ÖLÇÜLÜ HÖRGÜ -13.7 m^2;
   - 200 mm ÖLÇÜLÜ HÖRGÜ -149.27 m^2;
7. BİNANIN MEMARLIQ PLANLAŞDIRMA HƏLLİ TİKİNTİ NORMA VƏ QAYDALARINA UYĞUN HƏLL OLUNUR;
   - MƏRTƏBƏNİN HÜNDÜRLÜYÜ - 3.30 m
   - AŞIRIMLAR - 4.20 m, 4.60 m ,5.20 m, 6.0 m
   - ADDIMLAR - 6.0 m, 2.0 m ;
8. BİNANIN DAM ÖRTÜYÜ PROFNASTİL ÖRTÜK MATERİALINDAN İBARƏTDİR.
9. BİNANIN FASADLARI YÜKSƏK KEYFİYYƏTLİ SEMENT-QUM MƏHLULU İLƏ SUVANIR VƏ ATMOSFER TƏSİRLƏRİNƏ DAVAMLI YÜKSƏK KEYFİYYƏTLİ SUYA DAVAMLI FASAD BOYASI İLƏ ÜZLƏNİR.
10. ANTİSEYMİK TƏDBİRLƏR AZDTN 2.3-1-in TƏLƏBLƏRİNƏ ƏSASƏN İŞLƏNMƏLİDİR;
11. TİKİNTİ İŞLƏRİ YERİNƏ YETİRİLƏRKƏN TƏHLÜKƏSİZLİK NORMALARINA RİAYƏT OLUNMALIDIR;
12. ƏRAZİNİN SEYSMİKLİYİ 8_2 BAL - DIR.
    -TIKINTI RAYONU IV B KLIMATIK RAYONA AIDDIR.
    -QAR ÖRTÜYÜNÜN ÇƏKISI -80 KQ/M² (I RAYON)
    -KÜLƏYIN TƏZYIQ SÜRƏTI -73 KQ/M² (VI SİNİF)

ƏSAS TEXNİKİ - İQTİSADİ GÖSTƏRİCİLƏR

sıra sayı	Adı		Qeyd
1	Tikilinin ümumi sahəsi m^2	170.1	
2	Tikinti sahəsi m^2	217.2	
3	Mərtəbənin sayı	1	
4	Həcmi m^3	836.89	

Dəyiş.	Sah.sayı	Vərəq	İnv.№	İmza	Tarix
LBM		G.Musayeva			
Memar		G.Abdullayeva			
Yoxladı		S.Şükürova			

Sifarişçi: Cəfərov Mədət İslam oğlu

Abşeron rayonu, Qobu qəsəbəsində yerləşən torpaq sahəsində tikintisi nəzərdə tutulan anbar və inzibati binası

	mərhələ	vərəq	vərəqlər
Inzibati bina	İ.L	1	16
Ümumi məlumatlar	"STORM BUİLDİNG" MMC		

Razılaşdırılıb


Inv.№-si əvəzinə

İmza və tarix

Əsasın inv.№-si

A3



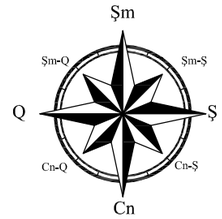

Razılaşdırılıb

İnv.№ əvəzinə

İmza və tarix

İnv.№ əslin

Dəyiş.	Sh.sən	Vərəq	İnv.№	İmza	Tarix
LBM		G.Musayeva			
Memar		G.Abdullayeva			
Yoxladı		S.Şükürova			


Sifarişçi: Cəfərov Mədət İslam oğlu

Abşeron rayonu, Qobu qəsəbəsində yerləşən torpaq sahəsində tikintisi nəzərdə tutulan anbar və inzibati binası


Inzibati bina	Mərhələ	Vərəq	Vərəqlər
	İ.L	2	16
Mövqe planı	"STORM BUİLDİNG" MMC		

A3

Anbar və inzibati binanın ±0.000 səviyyəsinin planı

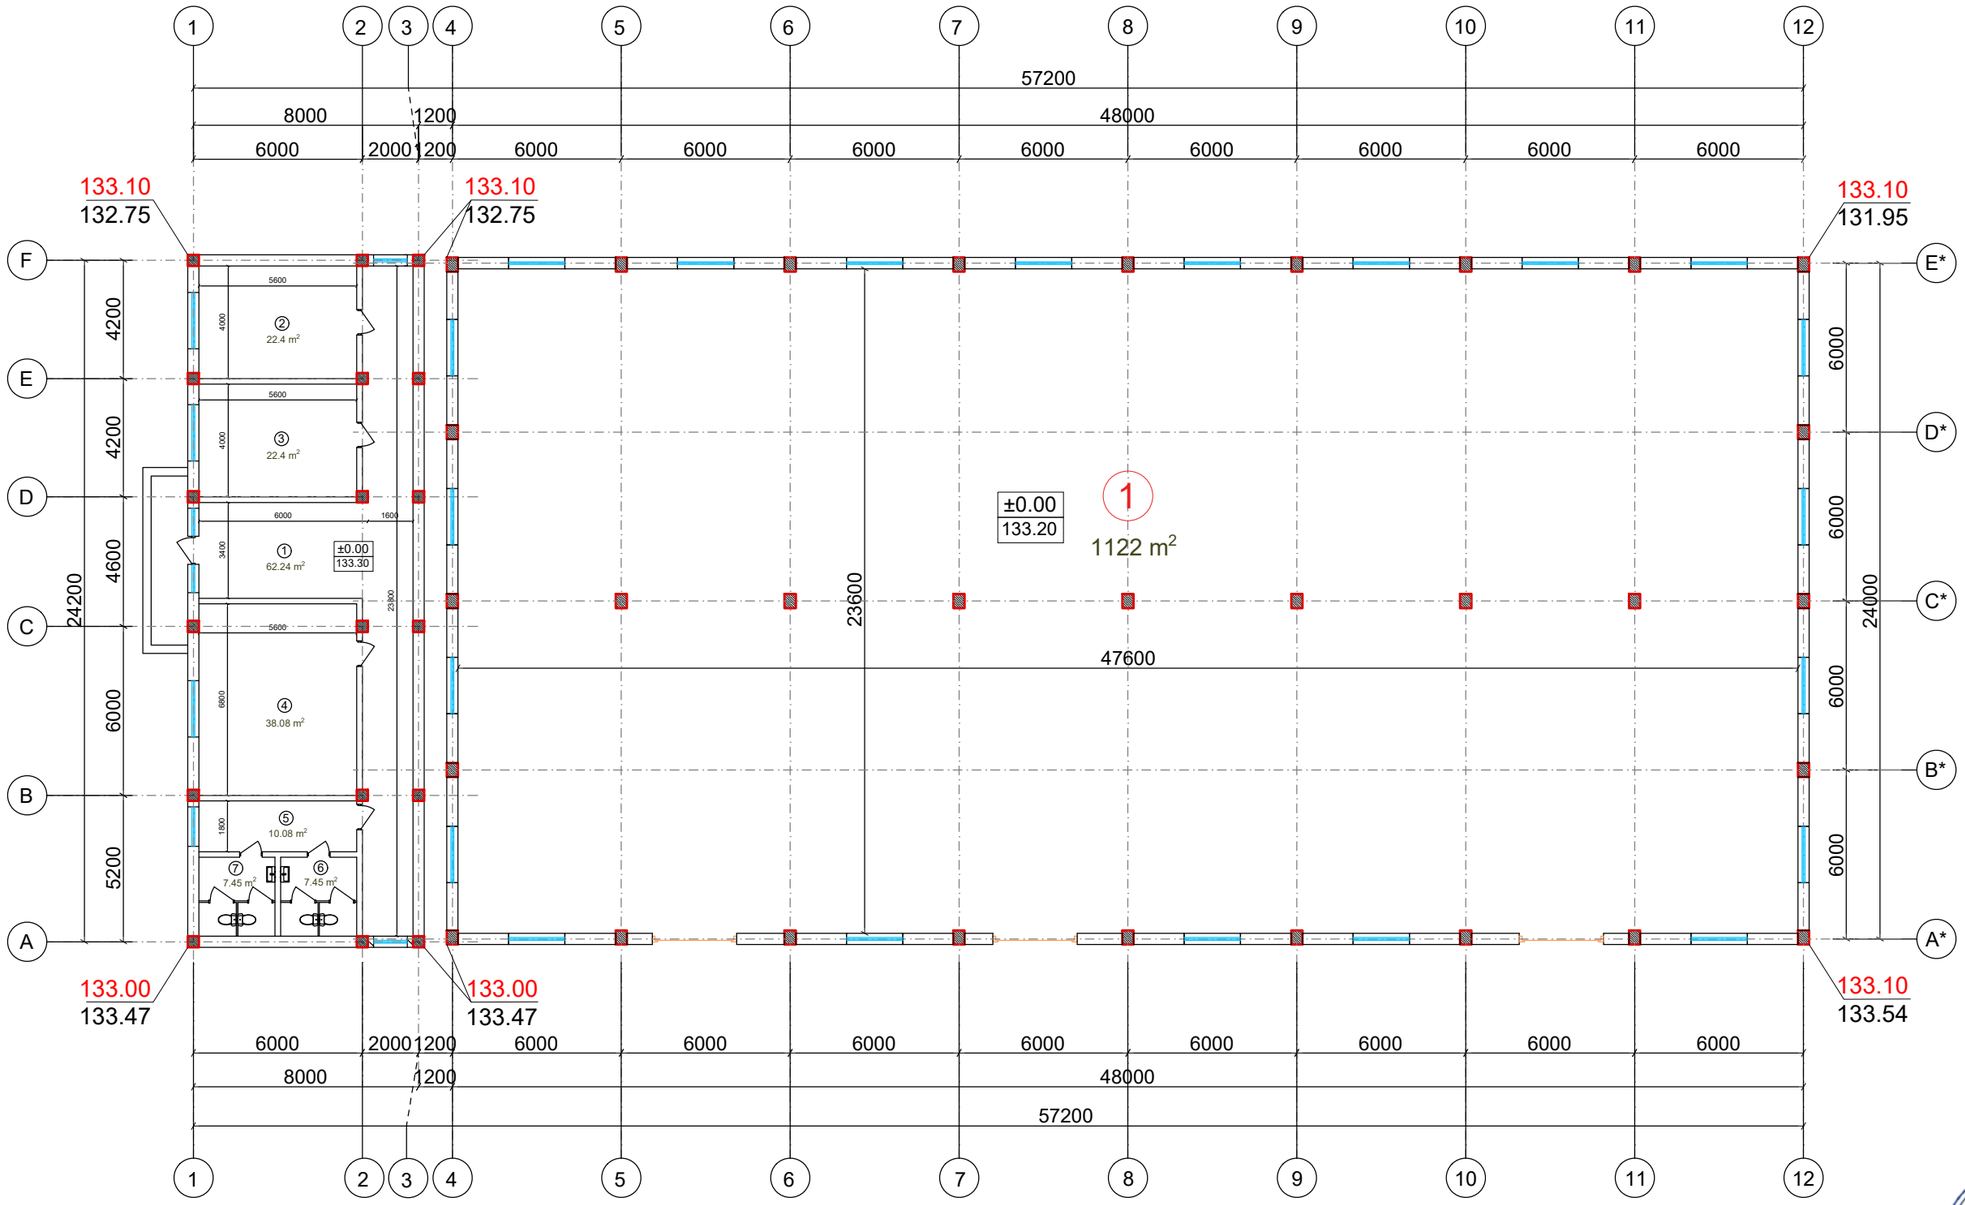

Bloklaşma sxemi

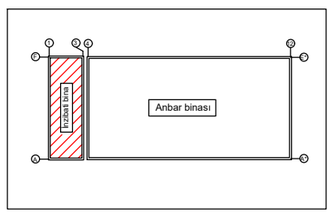

Dəyiş.	Sh.sən	Vərəq	Inv.№	İmza	Tarix
LBM		G.Musayeva			
Memar		G.Abdullayeva			
Yoxladı		S.Şükürova			

Sifarişçi: Cəfərov Mədət İslam oğlu

Abşeron rayonu, Qobu qəsəbəsində yerləşən torpaq sahəsində tikintisi nəzərdə tutulan anbar və inzibati binası

Inzibati bina

Mərhələ	Vərəq	Vərəqlər
İ.L	3	16

Anbar və inzibati binanın ±0.000 səviyyəsinin planı

"STORM BUİLDİNG" MMC

AZƏRBAYCAN RESPUBLİKASI MƏHDUD MƏSULİYYƏTLİ CƏMİYYƏTİ STORM BUİLDİNG LIMITED LIABILITY COMPANY

Razılaşdırılıb


İnv.№ əvəzinə

İmza və tarix

İnv.№ əslin

A3


±0.000 səviyyəsinin planı

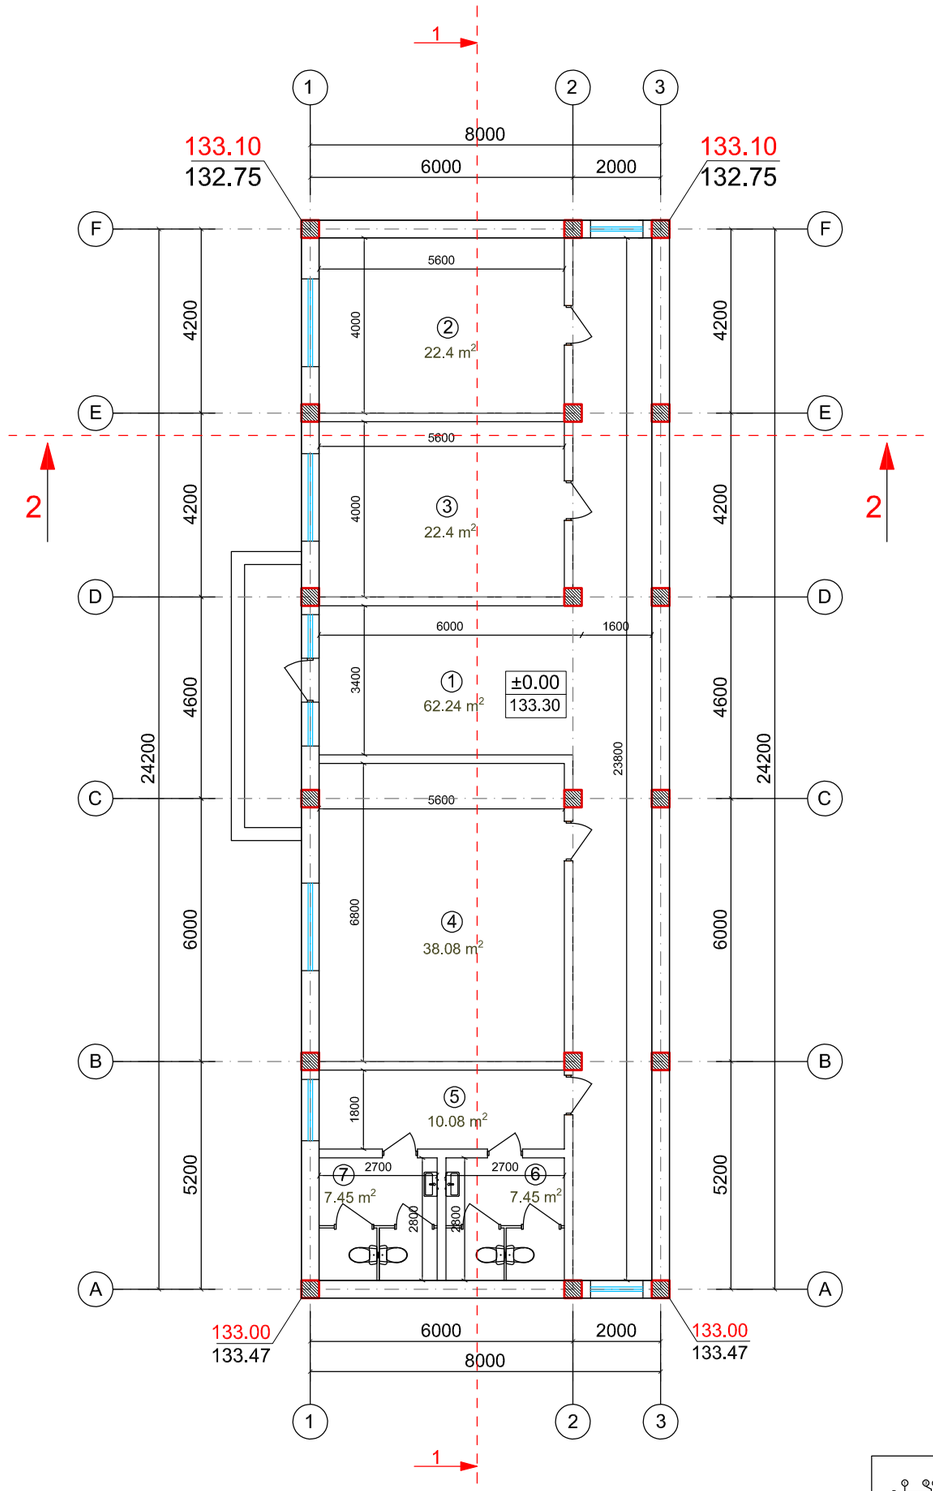

YERLƏŞQƏLƏRİN EKSPLİKASİYASI

Otağın nömrəsi	Adı	Sahəsi (m^2)	Otağın kateqoriyası
1	Dəhliz	62.24	
2	İşçi otağı	22.4	
3	Nəzarətçi otağı	22.4	
4	İclas otağı	38.08	
5	Tambur	10.08	
6	Sanitar qovşağı (kişi üçün)	7.45	
7	Sanitar qovşağı (qadın üçün)	7.45	
	Cəmi	170.1	

Bloklaşma sxemi

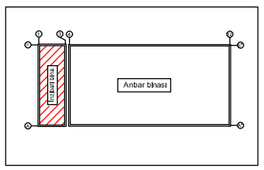

Dəyiş.	Sh.sən	Vərəq	İnv.№	İmza	Tarix
LBM		G.Musayeva			
Memar		G.Abdullayeva			
Yoxladı		S.Şükürova			

Sifarişçi: Cəfərov Mədət İslam oğlu

Abşeron rayonu, Qobu qəsəbəsində yerləşən torpaq sahəsində tikintisi nəzərdə tutulan anbar və inzibati binası

İnzibati bina

Mərhələ	Vərəq	Vərəqlər
İ.L	4	16

±0.000 səviyyəsinin planı

"STORM BUİLDİNG" MMC

Razılaşdırılıb


İnv.№ əvəzinə

İmza və tarix

İnv.№ əslin

A3


±0.000 səviyyəsinin divar markalanması (hörgü planı)

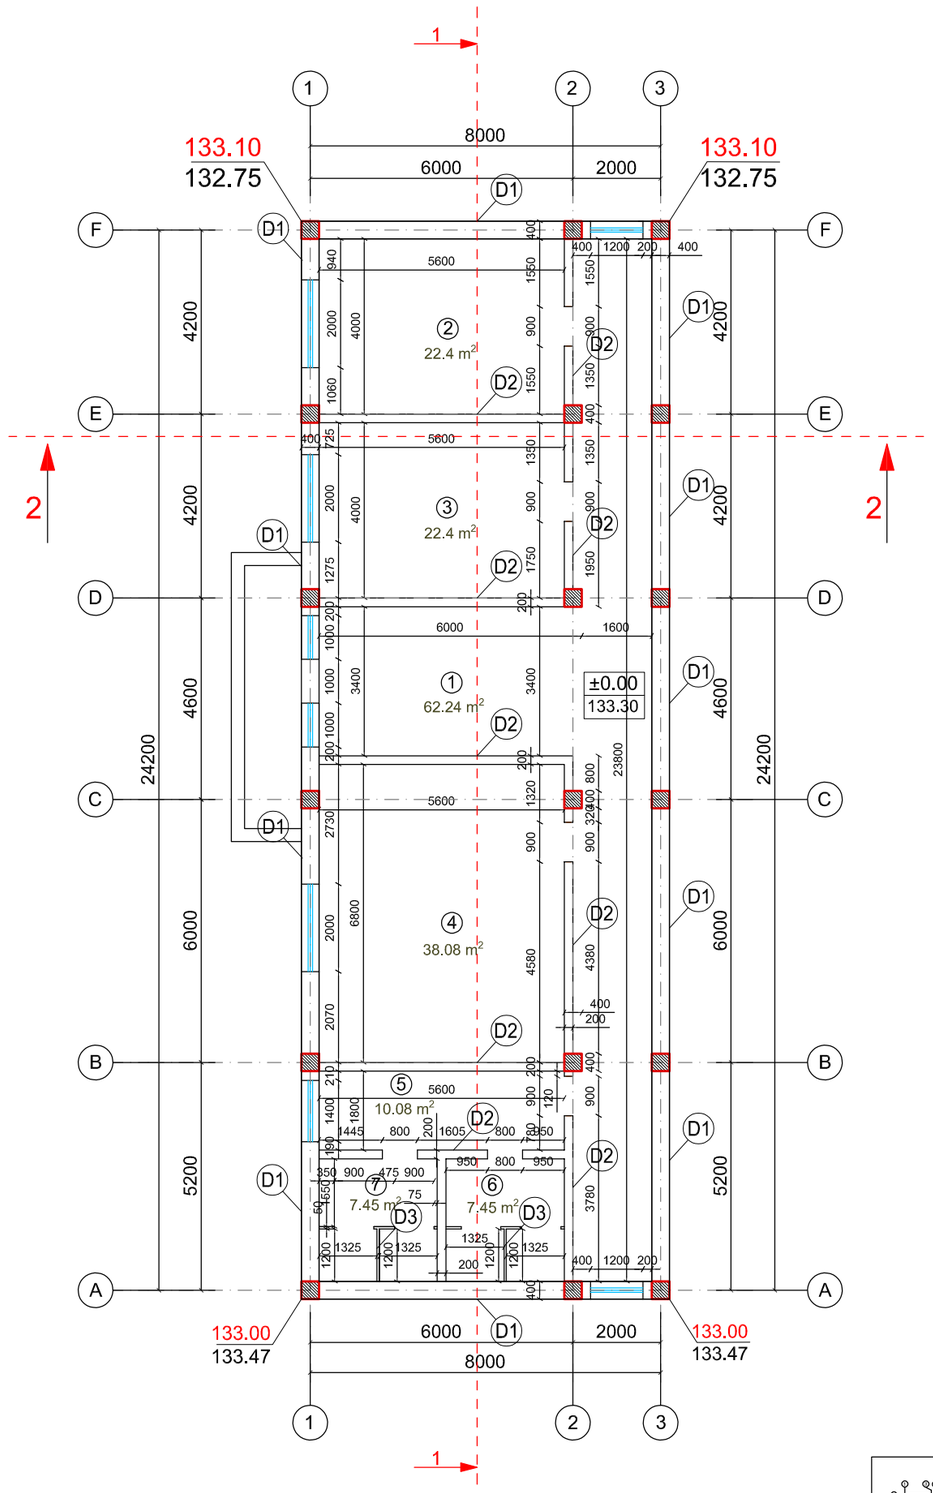

Tikinti işlərinin cədvəli

№	Adları	Eni (m)	Uzunluğu (m)	Hündürlüyü (m)	Ölçü vahidi (m^2)
D1	Xarici divarların (mişarlanmış əhəng daşı) quraşdırılması	0.4	64.3	3.25	187.73
D2	Arakəsmələrin (kərpic) quraşdırılması	0.2	49.45	3.25	149.27
D3	Arakəsmələrin (kərpic) quraşdırılması	0.05	4.19	3.25	13.7

Bloklaşma sxemi

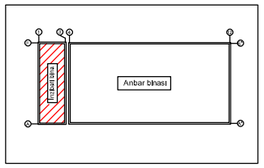

Dəyiş.	Sh.sən	Vərəq	İnv.№	İmza	Tarix
LBM		G.Musayeva			
Memar		G.Abdullayeva			
Yoxladı		S.Şükürova			

Sifarişçi: Cəfərov Mədət İslam oğlu

Abşeron rayonu, Qobu qəsəbəsində yerləşən torpaq sahəsində tikintisi nəzərdə tutulan anbar və inzibati binası

İnzibati bina

Mərhələ	Vərəq	Vərəqlər
İ.L	5	16

±0.000 səviyyəsinin divar markalanması (hörgü planı)


"STORM BUİLDİNG" MMC

A3

Razılaşdırılıb


İnv.№ əslin | İmza və tarix | İnv.№ əvəzinə

±0.000 səviyyəsinin döşəmə markalanması (bəzək planı)

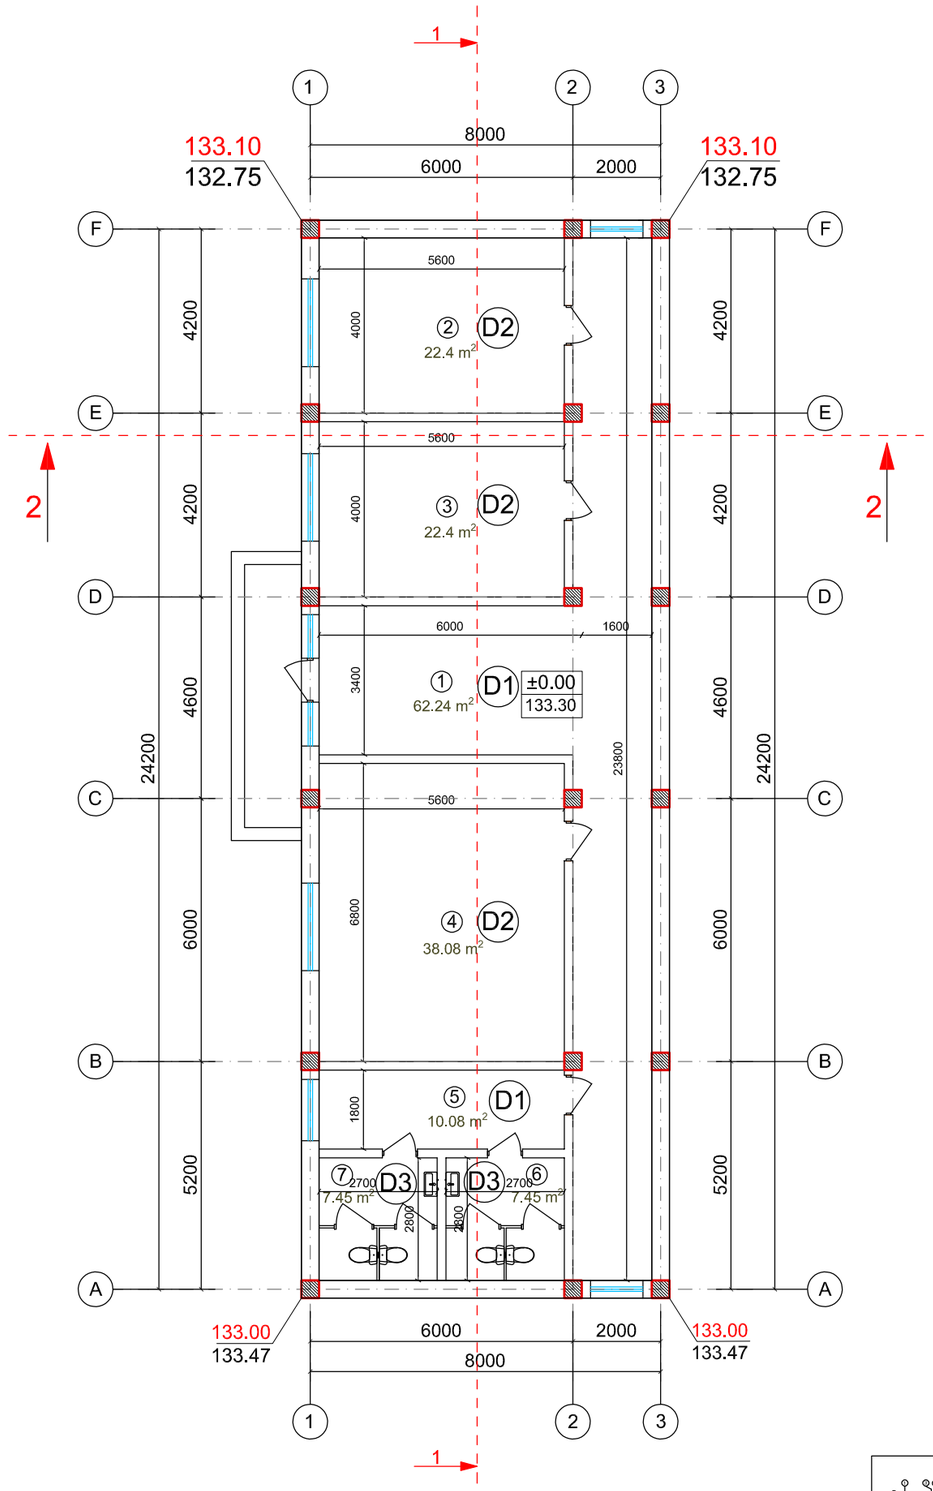

YERLƏŞQƏLƏRİN EKSPLİKASİYASI			
Otağın nömrəsi	Adı	Sahəsi (m^2)	Otağın kateqoriyası
1	Dəhliz	62.24	
2	İşçi otağı	22.4	
3	Nəzarətçi otağı	22.4	
4	İclas otağı	38.08	
5	Tambur	10.08	
6	Sanitar qovşağı (kişi üçün)	7.45	
7	Sanitar qovşağı (qadın üçün)	7.45	
	Cəmi	170.1	

Bloklaşma sxemi

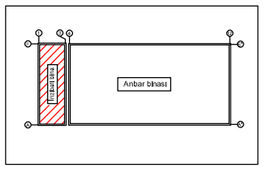

Razılaşdırılıb

İnv.№ əvəzinə

İmza və tarix

İnv.№ əslin

Dəyiş.	Sh.sən	Vərəq	İnv.№	İmza	Tarix
LBM		G.Musayeva			
Memar		G.Abdullayeva			
Yoxladı		S.Şükürova			

Sifarişçi: Cəfərov Mədət İslam oğlu

Abşeron rayonu, Qobu qəsəbəsində yerləşən torpaq sahəsində tikintisi nəzərdə tutulan anbar və inzibati binası

İnzibati bina


Mərhələ	Vərəq	Vərəqlər
İ.L	6	16

±0.000 səviyyəsinin döşəmə markalanması (bəzək planı)

"STORM BUİLDİNG" MMC


A3

±0.000 səviyyəsinin tavan markalanması (bəzək planı)

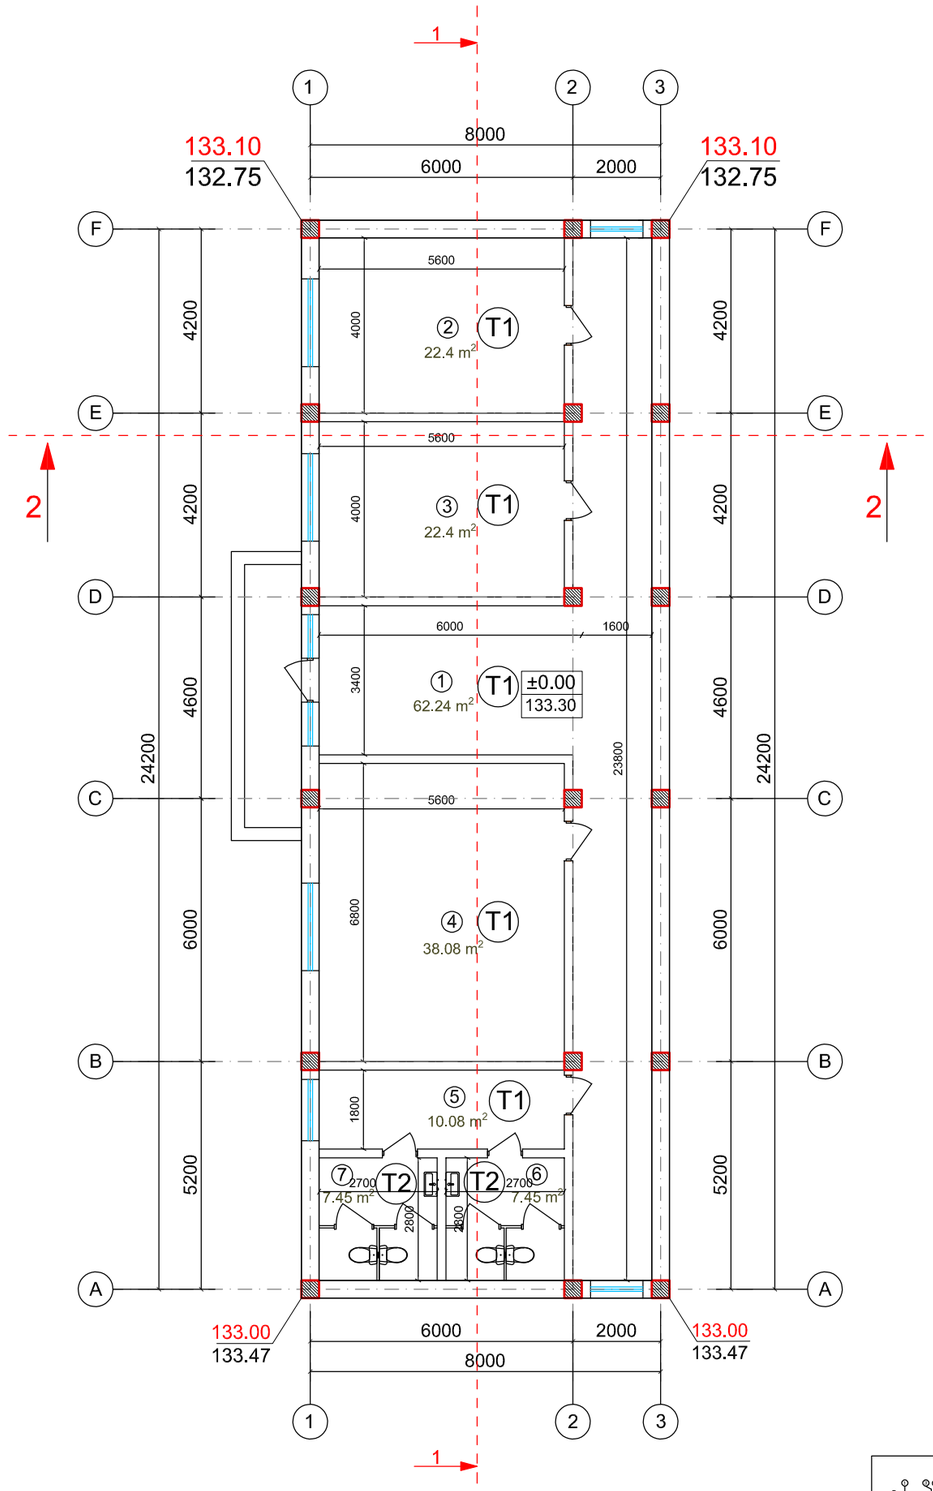

YERLƏŞQƏLƏRİN EKSPLİKASİYASI			
Otağın nömrəsi	Adı	Sahəsi (m^2)	Otağın kateqoriyası
1	Dəhliz	62.24	
2	İşçi otağı	22.4	
3	Nəzarətçi otağı	22.4	
4	İclas otağı	38.08	
5	Tambur	10.08	
6	Sanitar qovşağı (kişi üçün)	7.45	
7	Sanitar qovşağı (qadın üçün)	7.45	
	Cəmi	170.1	

Bloklaşma sxemi

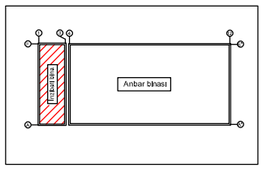

Razılaşdırılıb

İnv.№ əvəzinə

İmza və tarix

İnv.№ əslin

Dəyiş.	Sh.sən	Vərəq	İnv.№	İmza	Tarix
LBM		G.Musayeva			
Memar		G.Abdullayeva			
Yoxladı		S.Şükürova			

Sifarişçi: Cəfərov Mədət İslam oğlu

Abşeron rayonu, Qobu qəsəbəsində yerləşən torpaq sahəsində tikintisi nəzərdə tutulan anbar və inzibati binası

İnzibati bina

Mərhələ	Vərəq	Vərəqlər
İ.L	7	16


±0.000 səviyyəsinin tavan markalanması (bəzək planı)

"STORM BUİLDİNG" MMC

AZƏRBAYCAN RESPUBLİKASI MƏHDUD MƏSULİYYƏTLİ CƏMİYYƏTİ STORM BUİLDİNG


A3

±0.000 səviyyəsinin qapı-pəncərələrin markalanması (bəzək planı)

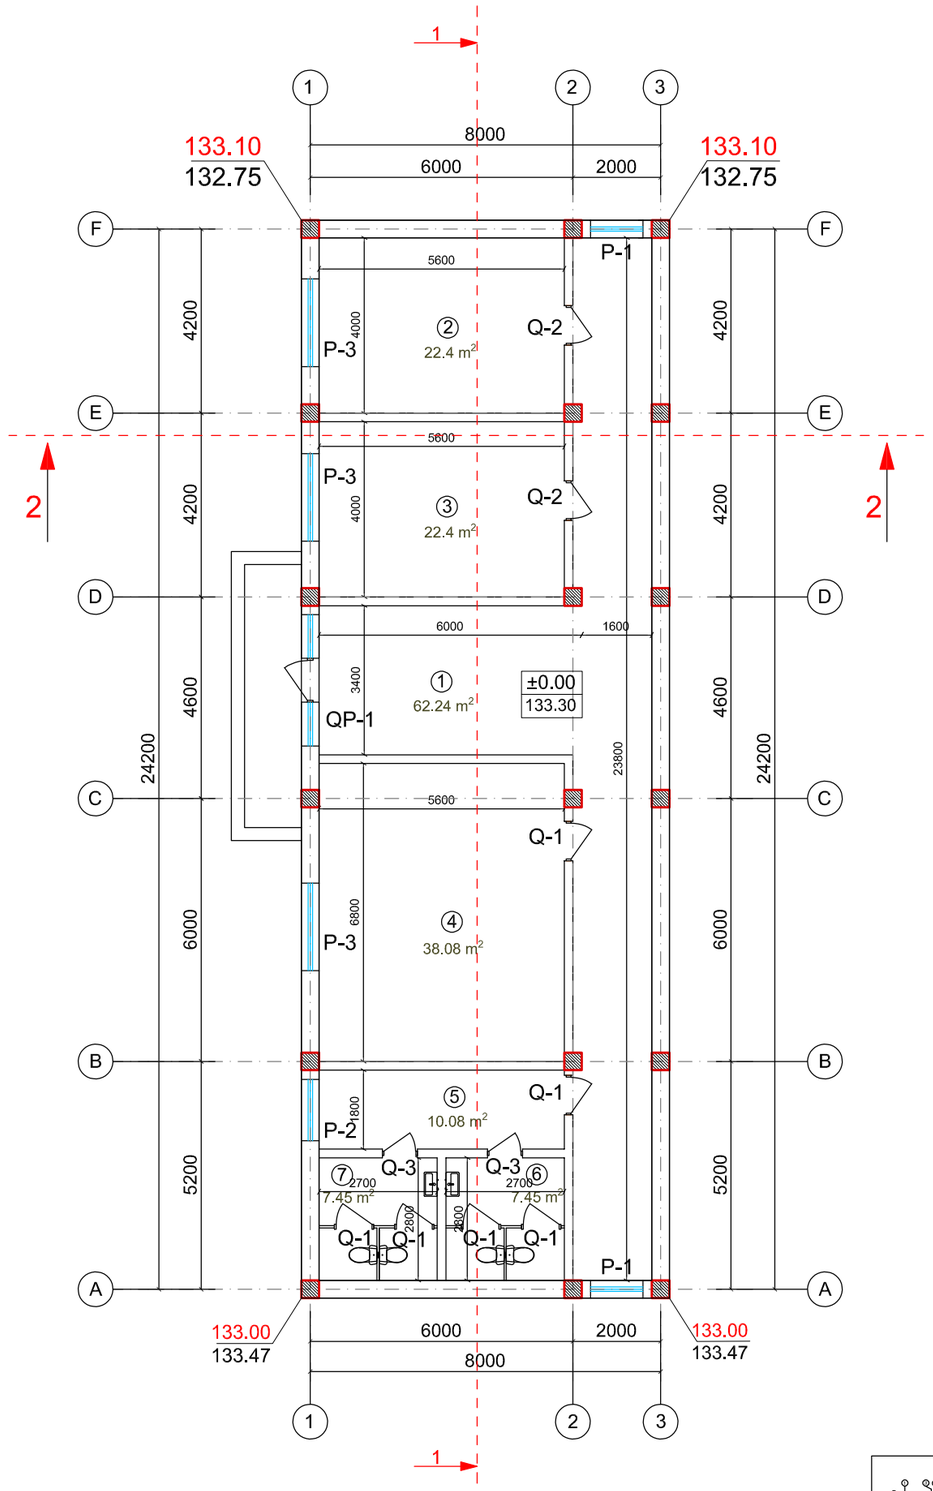

YERLƏŞQƏLƏRİN EKSPLİKASİYASI			
Otağın nömrəsi	Adı	Sahəsi (m^2)	Otağın kateqoriyası
1	Dəhliz	62.24	
2	İşçi otağı	22.4	
3	Nəzarətçi otağı	22.4	
4	İclas otağı	38.08	
5	Tambur	10.08	
6	Sanitar qovşağı (kişi üçün)	7.45	
7	Sanitar qovşağı (qadın üçün)	7.45	
	Cəmi	170.1	

Bloklaşma sxemi

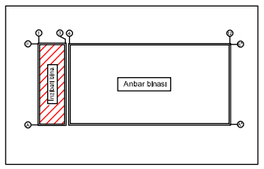

Razılaşdırılıb

İnv.№ əvəzinə

İmza və tarix

İnv.№ əslin

Dəyiş.	Sh.sən	Vərəq	İnv.№	İmza	Tarix
LBM		G.Musayeva			
Memar		G.Abdullayeva			
Yoxladı		S.Şükürova			

Sifarişçi: Cəfərov Mədət İslam oğlu

Abşeron rayonu, Qobu qəsəbəsində yerləşən torpaq sahəsində tikintisi nəzərdə tutulan anbar və inzibati binası

İnzibati bina

Mərhələ	Vərəq	Vərəqlər
İ.L	8	16


±0.000 səviyyəsinin qapı-pəncərə markalanması (bəzək planı)

"STORM BUİLDİNG" MMC

AZƏRBAYCAN RESPUBLİKASI MƏHDUD MƏSULİYYƏTLİ CƏMİYYƏTİ STORM BUİLDİNG


A3

±0.000 səviyyəsinin mebel planı

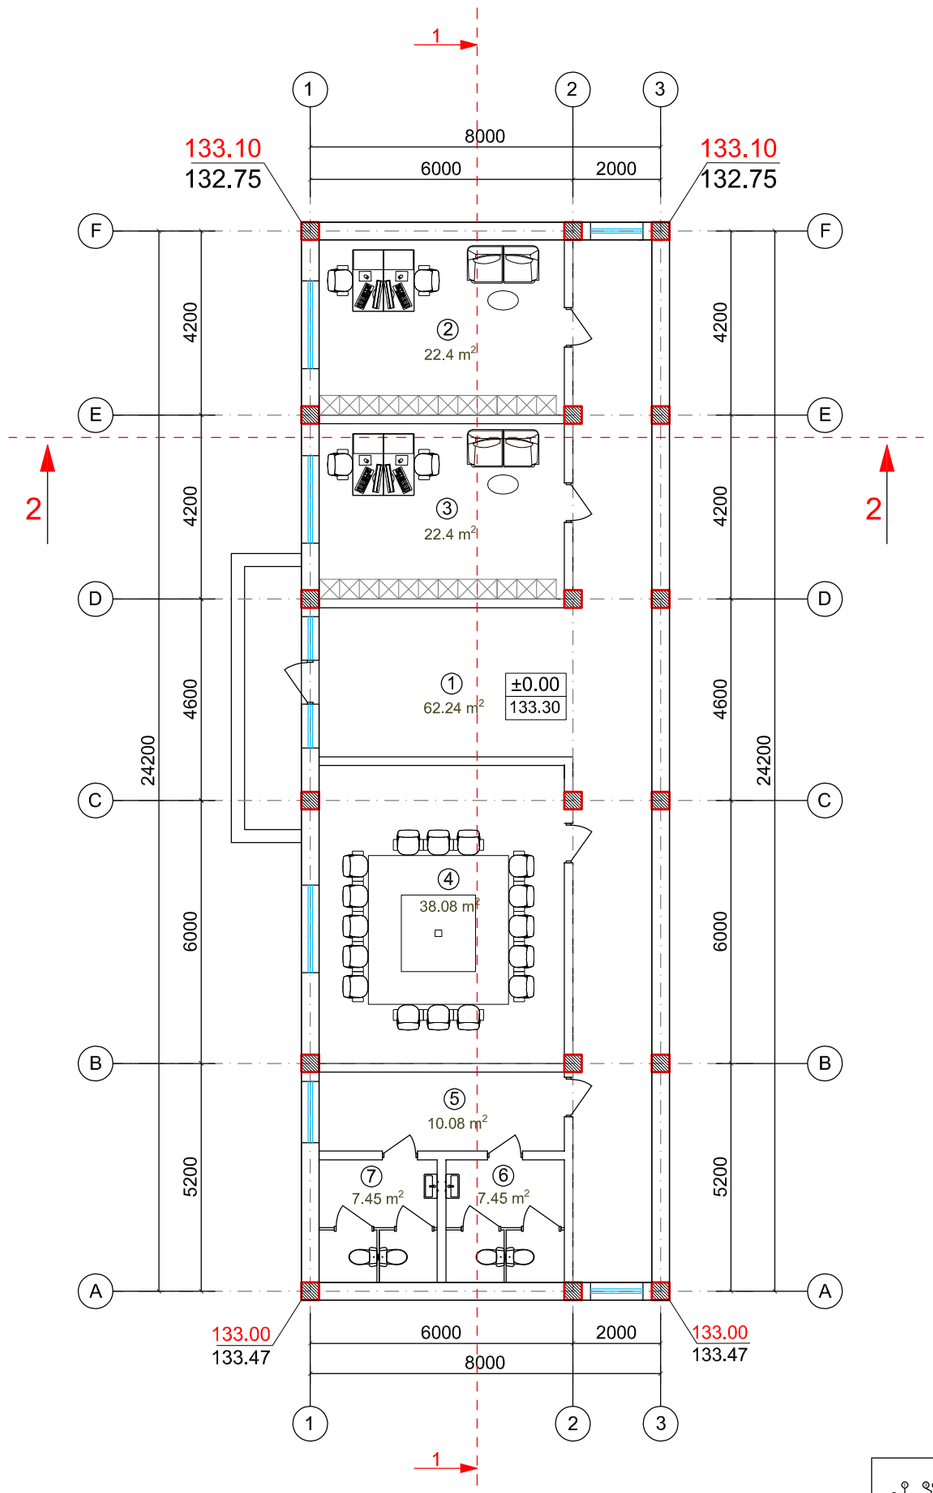

YERLƏŞQƏLƏRİN EKSPLİKASİYASI			
Otağın nömrəsi	Adı	Sahəsi (m^2)	Otağın kateqoriyası
1	Dəhliz	62.24	
2	İşçi otağı	22.4	
3	Nəzarətçi otağı	22.4	
4	İclas otağı	38.08	
5	Tambur	10.08	
6	Sanitar qovşağı (kişi üçün)	7.45	
7	Sanitar qovşağı (qadın üçün)	7.45	
	Cəmi	170.1	

Bloklaşma sxemi

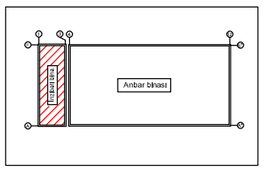

Razılaşdırılıb

İnv.№ əvəzinə

İmza və tarix

İnv.№ əslin

Dəyiş.	Sh.sən	Vərəq	İnv.№	İmza	Tarix
LBM		G.Musayeva			
Memar		G.Abdullayeva			
Yoxladı		S.Şükürova			

Sifarişçi: Cəfərov Mədət İslam oğlu

Abşeron rayonu, Qobu qəsəbəsində yerləşən torpaq sahəsində tikintisi nəzərdə tutulan anbar və inzibati binası

İnzibati bina

Mərhələ	Vərəq	Vərəqlər
İ.L	9	16


±0.000 səviyyəsinin mebel planı

"STORM BUİLDİNG" MMC


AZƏRBAYCAN RESPUBLİKASI MƏHDUD MƏSULİYYƏTLİ CƏMİYYƏTİ STORM BUİLDİNG LIMITED LIABILITY COMPANY

A3

Damın planı

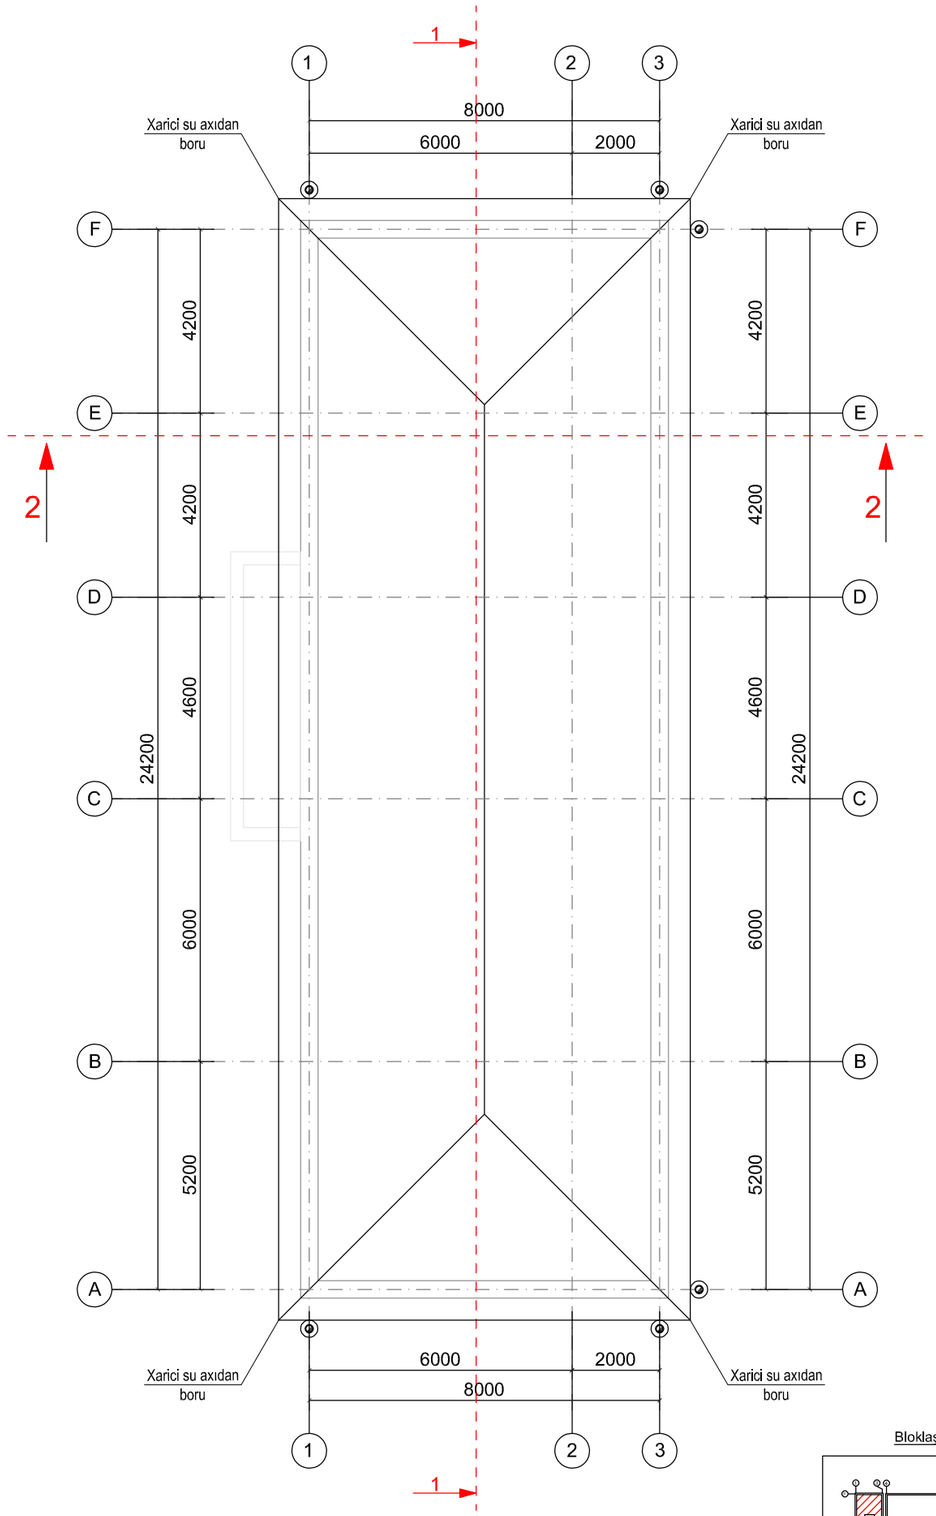

Bloklaşma sxemi

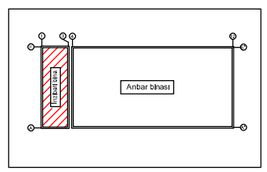

Mövqe	MATERİALLARIN TƏSNİFATI			
	Adı	Ölçü vahidi	Miqdarı 1 ədəd üçün	Miqdarı bina üzrə
1	Boru Ø100	m		21.8
2	Dirsək Ø100	ədəd		6
3	Su qəbul edici qıf	ədəd	1	6
4	Metal xamut 100x150	ədəd		30

Dəyiş.	Sh.sən	Vərəq	İnv.№	İmza	Tarix
LBM		G.Musayeva			
Memar		G.Abdullayeva			
Yoxladı		S.Şükürova			

Sifarişçi: Cəfərov Mədət İslam oğlu

Abşeron rayonu, Qobu qəsəbəsində yerləşən torpaq sahəsində tikintisi nəzərdə tutulan anbar və inzibati binası

İnzibati bina	Mərhələ	Vərəq	Vərəqlər
	İ.L	10	16
Damın planı	"STORM BUİLDİNG" MMC		

A3


Razılaşdırılıb

İnv.№ əvəzinə


İmza və tarix

İnv.№ əslin

Kəsik 1-1

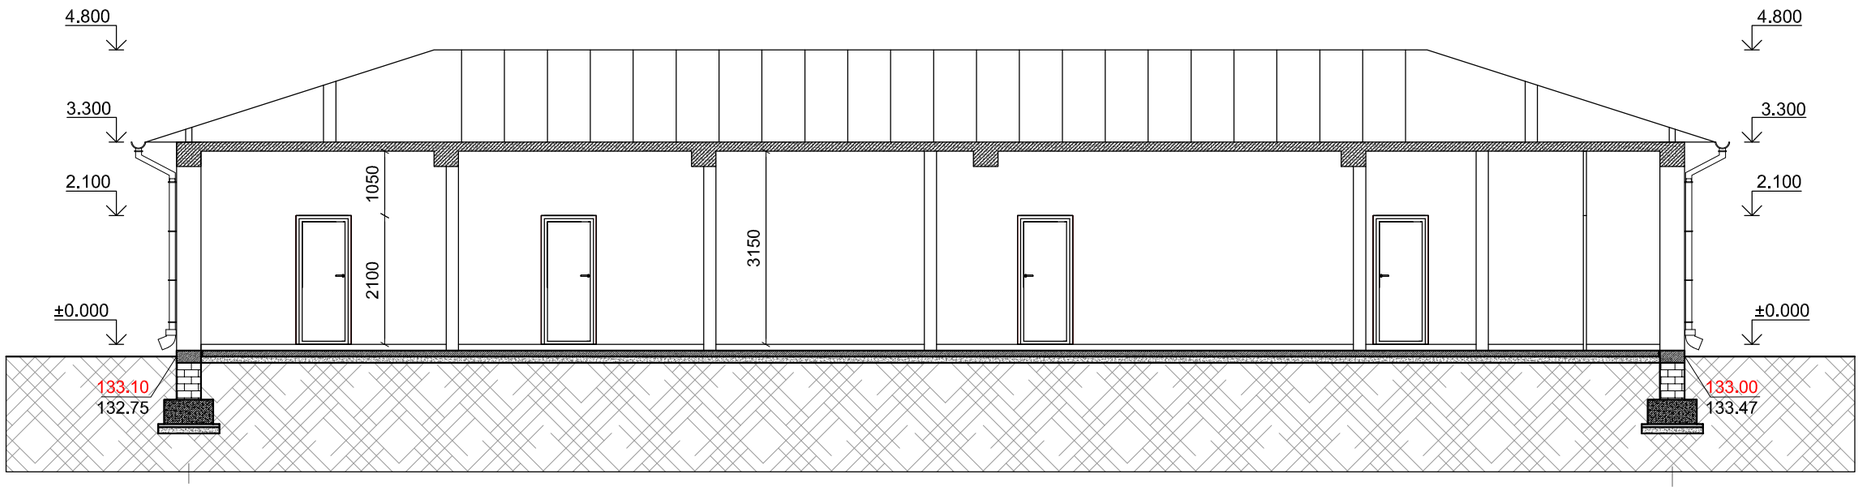

Bloklaşma sxemi

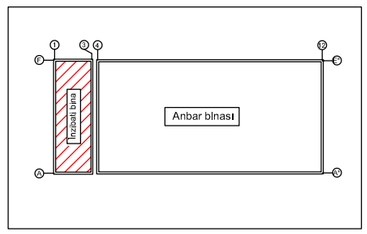

Dəyiş.	Sh.sən	Vərəq	İnv.№	İmza	Tarix
LBM		G.Musayeva			
Memar		G.Abdullayeva			
Yoxladı		S.Şükürova			

Sifarişçi: Cəfərov Mədət İslam oğlu

Abşeron rayonu, Qobu qəsəbəsində yerləşən torpaq sahəsində tikintisi nəzərdə tutulan anbar və inzibati binası

İnzibati bina	Mərhələ	Vərəq	Vərəqlər
	İ.L	11	16
Kəsik 1-1	"STORM BUİLDİNG" MMC		

AZƏRBAYCAN RESPUBLİKASI MƏHDUD MƏSULİYYƏTLİ CƏMİYYƏTİ STORM BUİLDİNG LIMITED LIABILITY COMPANY AZERBAIJAN REPUBLIC

Razılaşdırılıb


İnv.№ əvəzinə

İmza və tarix


İnv.№ əslin

A3

Kəsik 2-2

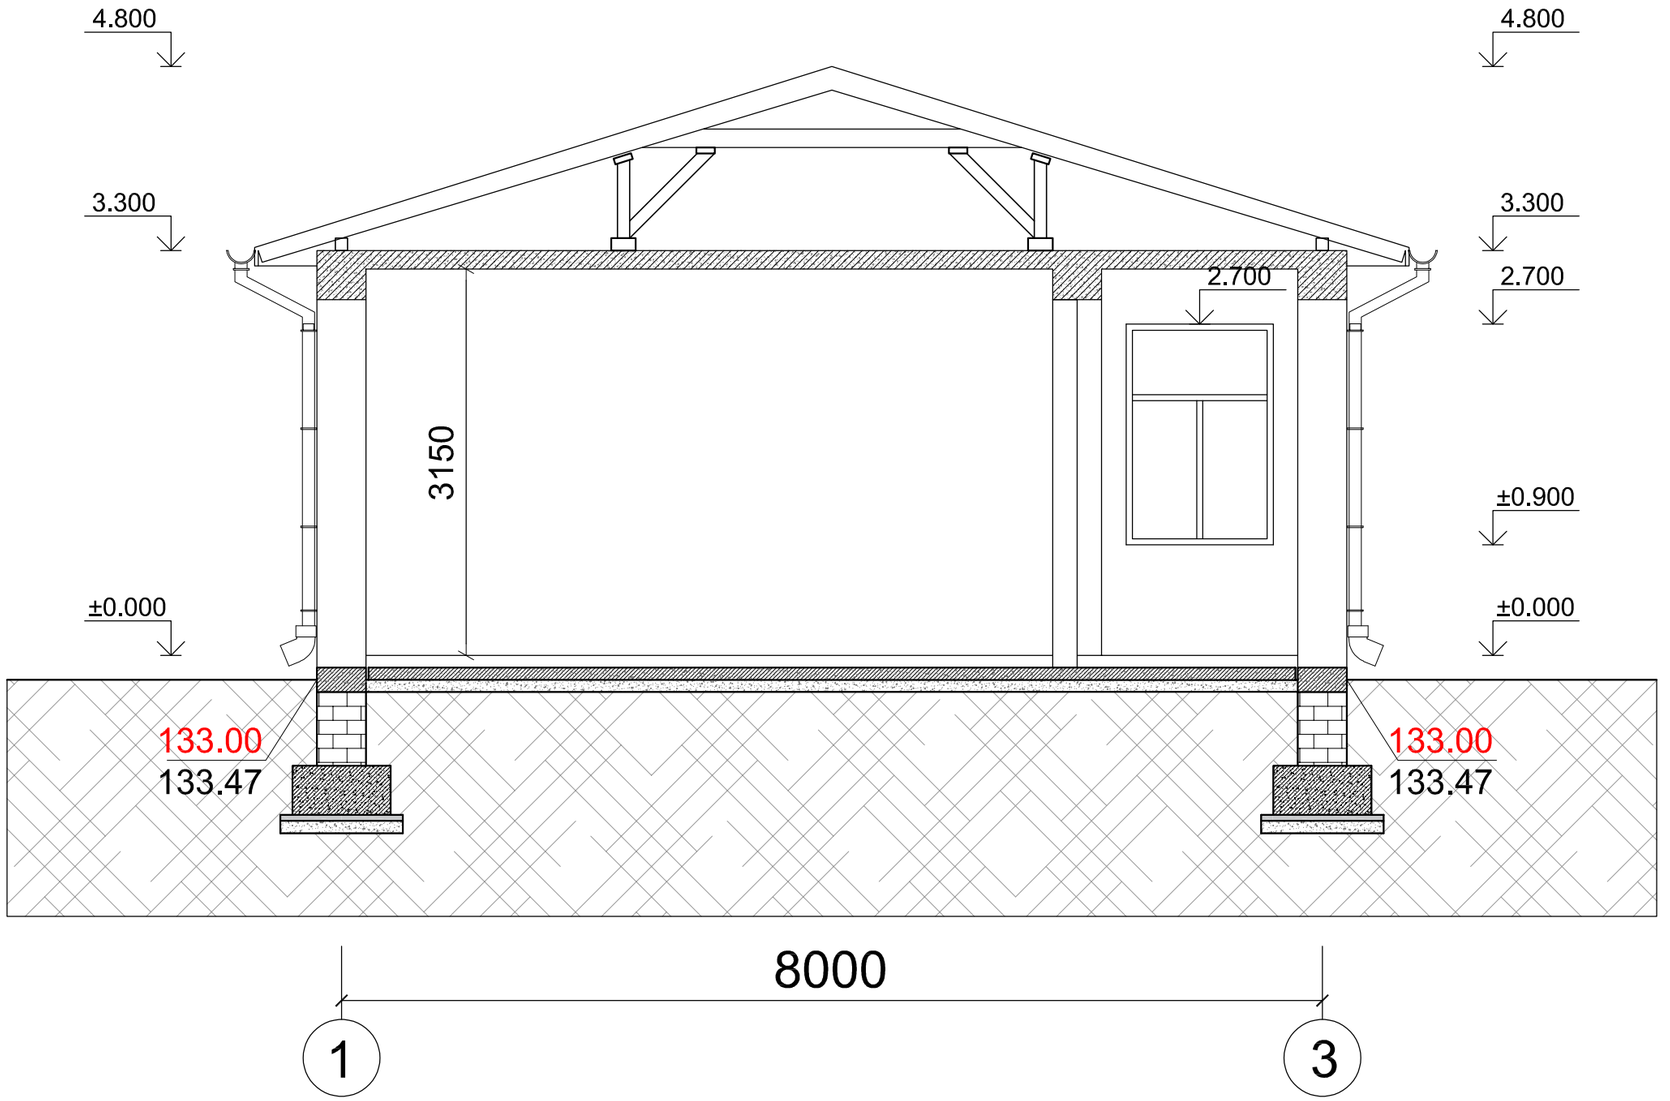

Bloklaşma sxemi

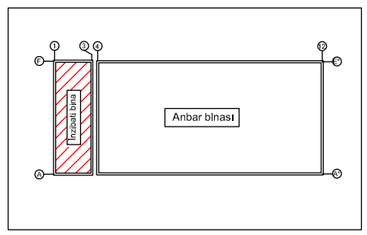

Dəyiş.	Sh.sən	Vərəq	Inv.№	İmza	Tarix
LBM		G.Musayeva			
Memar		G.Abdullayeva			
Yoxladı		S.Şükürova			

Sifarişçi: Cəfərov Mədət İslam oğlu

Abşeron rayonu, Qobu qəsəbəsində yerləşən torpaq sahəsində tikintisi nəzərdə tutulan anbar və inzibati binası

İnzibati bina	Mərhələ	Vərəq	Vərəqlər
	İ.L	12	16
Kəsik 2-2	"STORM BUİLDİNG" MMC		

AZƏRBAYCAN RESPUBLİKASI MƏHDUD MƏSULİYYƏTLİ CƏMİYYƏTİ STORM BUİLDİNG LIMITED LIABILITY COMPANY

Razılaşdırılıb


İnv.№ əvəzinə

İmza və tarix


İnv.№ əslin

A3

Fasad F-A

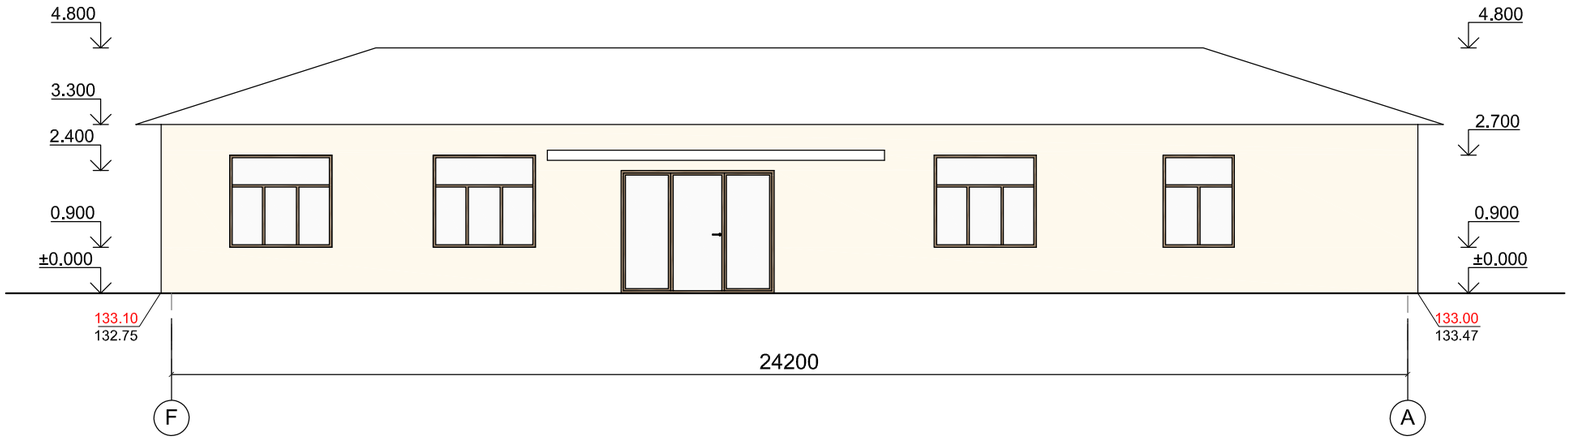

Fasad A-F

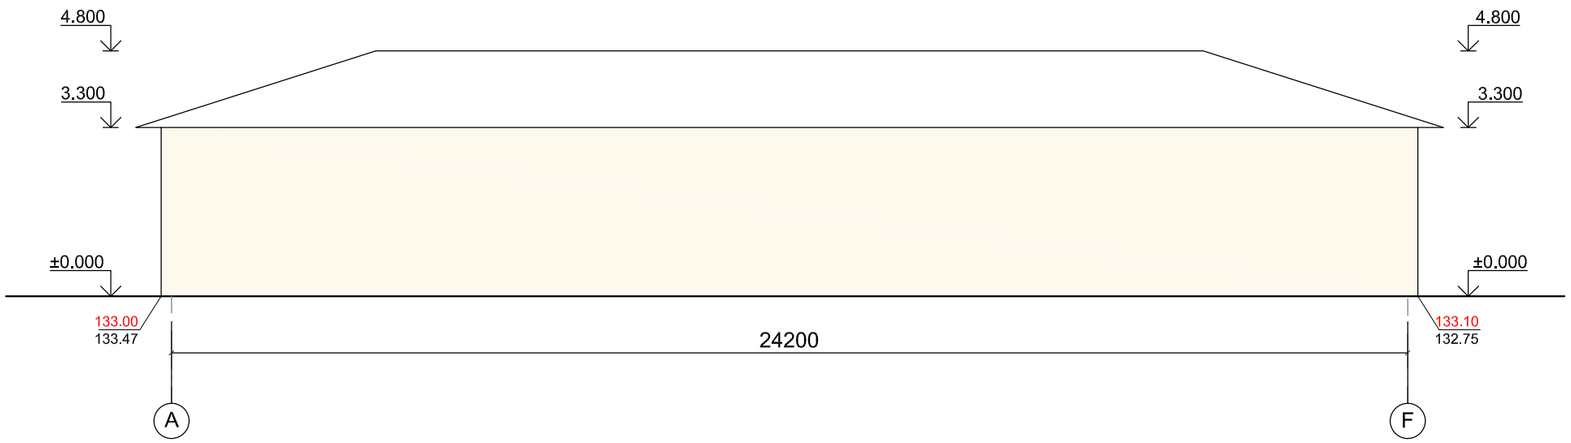


Razılaşdırılıb

İnv.№ əvəzinə


İmza və tarix

İnv.№ əslin

Fasad materiallarının spesifikasiyası

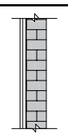Fasad materiallarının adı	Sahə m^2	Düyün
1. Mişarlanmış əhəng daşı 2. Suvaq 3. 3 qat boya	140.5	

Bloklaşma sxemi

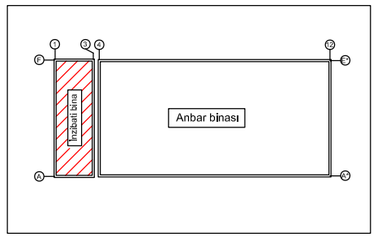

Dəyiş.	Sh.sən	Vərəq	Inv.№	İmza	Tarix
LBM		G.Musayeva			
Memar		G.Abdullayeva			
Yoxladı		S.Şükürova			

Sifarişçi: Cəfərov Mədət İslam oğlu

Abşeron rayonu, Qobu qəsəbəsində yerləşən torpaq sahəsində tikintisi nəzərdə tutulan anbar və inzibati binası

İnzibati bina

Mərhələ	Vərəq	Vərəqlər
İ.L	13	16


Fasad F-A, Fasad A-F

"STORM BUİLDİNG" MMC


AZƏRBAYCAN RESPUBLİKASI MƏHDUD MƏSULİYYƏTLİ CƏMİYYƏTİ STORM BUİLDİNG

A3


Fasad 1-3

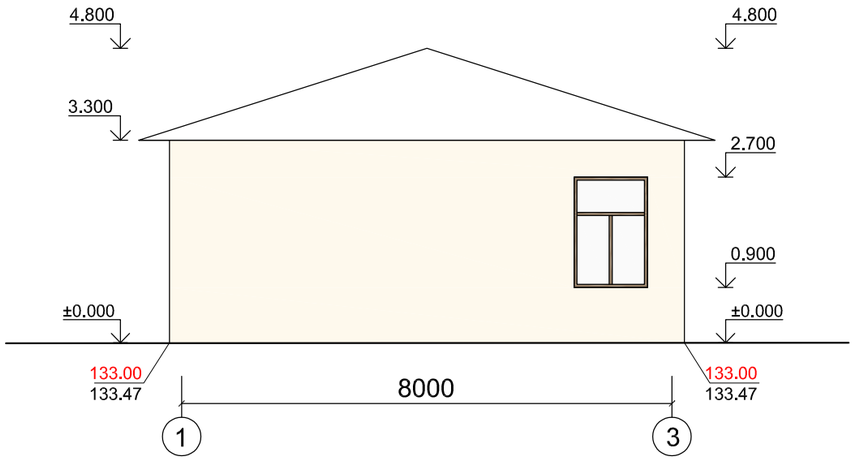


Fasad 3-1

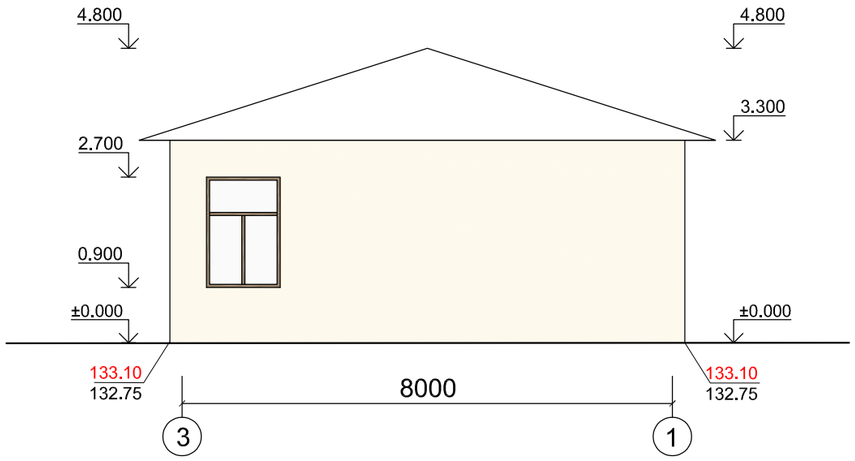

Fasad materiallarının spesifikasiyası

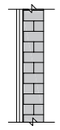Fasad materiallarının adı	Sahə m^2	Düyün
1. Mişarlanmış əhəng daşı 2. Suvaq 3. 3 qat boya	51.2	

Bloklaşma sxemi

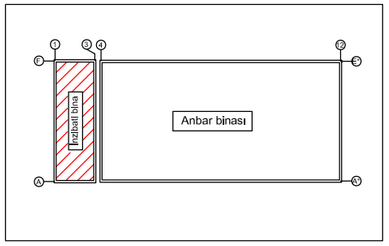

Dəyiş.	Sh.sən	Vərəq	Inv.№	İmza	Tarix
LBM		G.Musayeva			
Memar		G.Abdullayeva			
Yoxladı		S.Şükürova			

Sifarişçi: Cəfərov Mədət İslam oğlu

Abşeron rayonu, Qobu qəsəbəsində yerləşən torpaq sahəsində tikintisi nəzərdə tutulan anbar və inzibati binası

İnzibati bina	Mərhələ	Vərəq	Vərəqlər
	İ.L	14	16
Fasad 1-3, 3-1	"STORM BUİLDİNG" MMC		

A3






Razılaşdırılıb

İnv.№ əvəzinə


İmza və tarix

İnv.№ əslin

Döşəmə, tavan və divarın təsnifatı

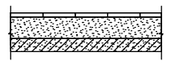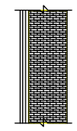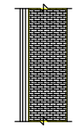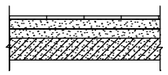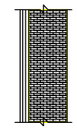Sıra sayı	Otağın adı və ya nömrəsi	Döşəmə	Sahə m²	Həcm m³	Düyün	Tavan	Sahə	Divar və arakəsmə	Sahə	Düyün
	±0.000 səviyyəsi									
1	1,5	**D1** 1.Süni qranit (keramoqranit) -10 mm 2.Yapışdırıcı - 10 mm 3.Sement-qum məhlulu - 50 mm 4.D/beton örtük tavası - 150 mm	 72.32 72.32 72.32	 10.84		**T1** Alçipan (alçipan+şpaklovka+2 qat suya davamlı boya)	72.32	1. Divar 2.Suvaq 3.Şpaklovka 4.Rənglənən divar kağızı 5.3 qat boya	257.08	
2	2,3,4	**D2** 1.Laminat - 8 mm 2.Dikt - 15 mm 3.Reyka (laqa) - 50 mm 4. Tol - 2 qat 5. Düzləndirici qat - 60 mm 6. D/ beton örtük tavası - 150 mm	 82.88 82.88 82.88 82.88	 4.14 12.43		**T1** Alçipan (alçipan+şpaklovka+2 qat suya davamlı boya)	82.88	1. Divar 2.Suvaq 3.Şpaklovka 4.Rənglənən divar kağızı 5.3 qat boya	209.56	
3	6,7	**D3** 1. Metlax - 8 mm 2.Sement-qum məhlulu - 50 mm 3.D/beton örtük tavası - 150 mm	 14.9 14.9	 2.23		**T2** Metal asma tavan(armstronq)	14.9	1.Divar 2.Suvaq 3.Kafel	123.76	

Bloklaşma sxemi

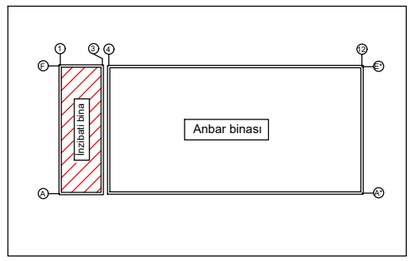

Dəyiş.	Sh.sən	Vərəq	Inv.№	İmza	Tarix
LBM		G.Musayeva			
Memar		G.Abdullayeva			
Yoxladı		S.Şükürova			

Sifarişçi: Cəfərov Mədət İslam oğlu

Abşeron rayonu, Qobu qəsəbəsində yerləşən torpaq sahəsində tikintisi nəzərdə tutulan anbar və inzibati binası

Inzibati bina	Mərhələ	Vərəq	Vərəqlər
	İ.L	15	16
Döşəmə, tavan və divar təsnifatı	"STORM BUİLDİNG" MMC		

Razılaşdırılıb

İnv.№ əvəzinə

İmza və tarix


İnv.№ əslin

A3


Qapı və pəncərələrin spesifikasiyası

Mövqe	İşarə	Adı		Sayı	Sahəsi m²	Qeyd
Q-1	MDF qapı	Qapı	900x2100 (h)	6	11.3	
Q-2	MDF qapı	Qapı	900x2100 (h)	2	3.8	
Q-3	Plastik (PVC) qapı	Qapı	800x2100 (h)	2	3.4	
P-1	Plastik (PVC) pəncərə	Pəncərə	1200 x 1800(h)	2	4.3	
P-2	Plastik (PVC) pəncərə	Pəncərə	1400 x 1800(h)	1	2.5	
P-3	Plastik (PVC) pəncərə	Pəncərə	2000 x 1800(h)	3	10.8	
QP-1	Alüminium qapı-pəncərə	Pəncərə-Qapı	3000 x 2400(h)	1	7.2	


Q-1 MARKALI QAPI (SAĞ)

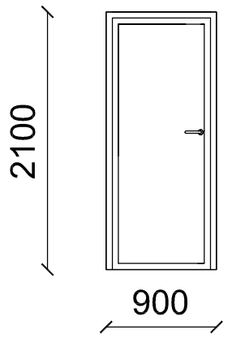


Q-2 MARKALI QAPI (SOL)

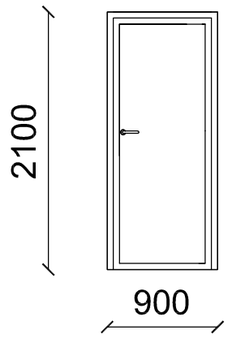


Q-3 MARKALI QAPI

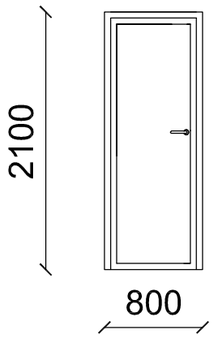


QP-1 MARKALI QAPI - PƏNCƏRƏ

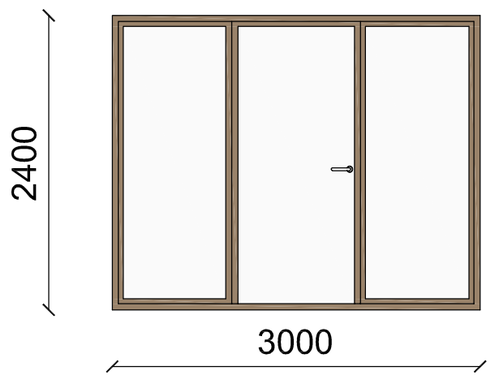


P-1 MARKALI PƏNCƏRƏ

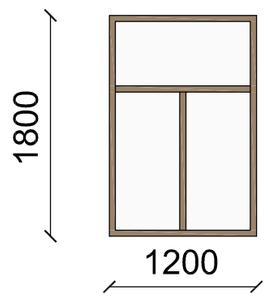


P-2 MARKALI PƏNCƏRƏ

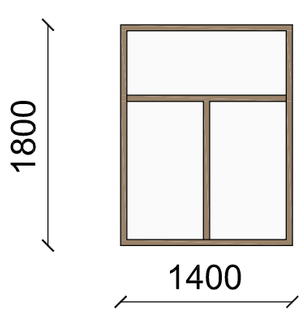

P-3 MARKALI PƏNCƏRƏ

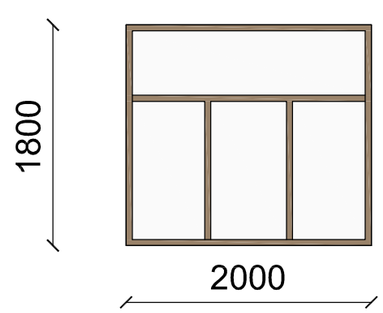

Bloklaşma sxemi

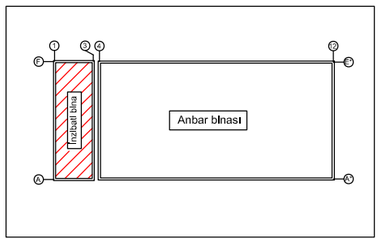

Dəyiş.	Sh.sən	Vərəq	Inv.№	İmza	Tarix
LBM		G.Musayeva			
Memar		G.Abdullayeva			
Yoxladı		S.Şükürova			

Sifarişçi: Cəfərov Mədət İslam oğlu

Abşeron rayonu, Qobu qəsəbəsində yerləşən torpaq sahəsində tikintisi nəzərdə tutulan anbar və inzibati binası

İnzibati bina

Mərhələ	Vərəq	Vərəqlər
İ.L	16	16

Qapı və pəncərələrin spesifikasiyası

"STORM BUİLDİNG" MMC

Razılaşdırılıb

İnv.№ əvəzinə

İmza və tarix

İnv.№ əslin

A3