A Z Ə R B A Y C A N  R E S P U B L İ K A S I

"S T O R M  B U İ L D İ N G"

M ə h d u d  M ə s u l i y y ə t l i  C ə m i y y ə t

# ABŞERON RAYONU, QOBU QƏSƏBƏSİNDƏ YERLƏŞƏN TORPAQ SAHƏSİNDƏ TİKİNTİSİ NƏZƏRDƏ TUTULAN ANBAR VƏ İNZİBATİ BİNASI

## Konstruksiya hissəsi
## (Anbar və inzibati bina)

Bakı-2026

A Z Ə R B A Y C A N  R E S P U B L İ K A S I

"S T O R M  B U İ L D İ N G"

M ə h d u d  M ə s u l i y y ə t l i  C ə m i y y ə t

# ABŞERON RAYONU, QOBU QƏSƏBƏSİNDƏ YERLƏŞƏN TORPAQ SAHƏSİNDƏ TİKİNTİSİ NƏZƏRDƏ TUTULAN ANBAR VƏ İNZİBATİ BİNASI

## Konstruksiya hissəsi
## (Anbar binası)

Direktor: A. Cahangiroğlu

L.B.M.: G. Musayeva

Bakı-2026

## Konstruksiya hissələrinin əsas cizgiləri

| Vərəq | Adı | Qeyd |
|---|---|---|
| | Dəmir beton konstruksiya cizgilərinin siyahisi | Dk-Mk |
| 1 | Ümumi verilənlər | Dk |
| 2 | Çalanın yerləşmə yerləşmə planı | Dk |
| 3 | Kəsik A-A | Dk |
| 4 | Kəsik B-B | Dk |
| 5 | Monolit d/b lentvari bünövrə və başmaqların yerləşmə planı | Dk |
| 6 | Bünövrə kəsikləri : Kəsik A-A, B-B | Dk |
| 7 | Monolit d/b lentvari bünövrə. Başmaq BM-1 | Dk |
| 8 | "±0.00" Səviyyəsində monolit d/b döşəmə və kəmər "Mk-1"-in yerləşmə planı | Dk |
| 9 | "±0.00" Səviyyəsində monolit d/b döşəmə və kəmər "Mk-1"-in konstruksiyasi | Dk |
| 10 | "-0.70" Səviyyəsində monolit d/b sütunların yerləşmə planı | Dk |
| 11 | "0.00" Səviyyəsində monolit d/b sütunların yerləşmə planı | Dk |
| 12 | "+7.00" Səviyyəsində monolit d/b sütunların yerləşmə planı | Dk |
| 13 | Monolit d/b sütun "Ms-1"-in konstruksiyası. | Dk |
| 14 | Monolit d/b sütun "Ms-2"-nin konstruksiyası. | Dk |
| 15 | Monolit d/b sütun "Ms-3"-ün konstruksiyası. | Dk |
| 16 | Monolit d/b sütun "Ms-4"-ün konstruksiyası. | Dk |
| 17 | "+3.70" Səviyyəsində monolit d/b kəmərlərin yerləşmə planı | Dk |
| 18 | "+7.00" Səviyyəsində monolit d/b rigellərin yerləşmə planı | Dk |
| 19 | "+8.00" Səviyyəsində monolit d/b rigellərin yerləşmə planı | Dk |
| 20 | Monolit d/b kəmər "Mk-2"-nin konstruksiyası | Dk |
| 21 | Monolit d/b rigel "Mr-1"-in konstruksiyası | Dk |
| 22 | Monolit d/b rigel "Mr-2"-nin konstruksiyası | Dk |
| 23 | Monolit d/b rigel "Mr-3"-ün konstruksiyası | Dk |
| 24 | Fermaların yerləşməsi | Mk |
| 25 | Ferma F-1 | Mk |
| 26 | Düyün "D-01" və "D-02" | Mk |
| 27 | Düyün "D-03" ;"D-04" ; "D-05" ; "D-06" və "D-07" | Mk |
| 28 | Düyün "D-08" | Mk |
| 29 | Ferma F-1 üçün material sərfi | Mk |
| 30 | Şaquli rabitə Şr-01 | Mk |
| 31 | Şaquli rabitə Şr-02 | Mk |
| 32 | Fermaların alt kəməri üzrə üfüqi rabitələrin və dartqıların yerləşmə planı | Mk |
| 33 | Alt kəmər üzrə üfüqi rabitə və dartqıların düyünləri | Mk |
| 34 | Fermaların üst kəməri üzrə üfüqi rabitələrin yerləşmə planı | Mk |
| 35 | Üst kəmər üzrə üfüqi rabitələrin düyünləri | Mk |
| 36 | Metal praqonların yerləşmə planı. Material sərfi | Mk |

## Ümumi məlumatlar :

1. Binanın konstruksiya hissəsinin cizgiləri baş plan və memarlıq hissəsinin layihəsinə əsasən yerinə yetirilmişdir.
2. Binanın konstruktiv sxemi çərçivəli sxem qəbul edilmişdir. Bünövrə , sütunlar , rigeller dəmir-beton. Binanın örtüyü isə metal fermalardan qəbul edilmişdir
3. Şərti olaraq "±0.000" səviyyəsi 1-ci mərtəbənin təmiz döşəmə səviyyəsinə uyğun olaraq götürülmüşdür. "±0.000 = 133.20"
4. İstehsalat işləri yerinə yetirilərkən "SNİP III - 4 - 80", "SNİP 3.02.01 - 87", "SNİP 3.03.01 - 87", "SNİP 3.04.01 - 87" və "SNİP 3.04.03 - 85" tikinti normaları tələblərinə riayət olunmuşdur.
5. Bünövrə əsasını bərk konsistensiyalı gilcə qruntu təşkil edir.

| | |
|---|---|
| Şərti hesabi təzyiq | $R_0$= 2.40 kqq/sm$^2$ |
| İlişmə qüvvəsi | $c^n$= 0.21 kqq/sm$^2$ |
| Daxili sürtünmə bucağı | $\varphi$= 22°30' |
| Deformasiya modulu (təbii) | E = 175.10 kqq/sm$^2$ |
| Həcm çəkisi - təbii | $\gamma$= 1.76 q/sm$^3$ |

6. Qruntun aqressivlik xassələri "SNİP 2.03.11 - 85"-ə sasən dəmir-beton konstruksiyalara qarşı orta aqressiv olduğu üçün torpaqla təmasda olan bütün dəmir-beton konstruksiyaların hazırlanması zamanı sulfatadavamlı portlandsementdən istifadə etmək lazımdır.
7. Bünövrənin oturduğu qrunt M.G.E-1 olduğundan qruntun kateqoriyası II sinfə aiddir.
8. Bünövrənin altında 10 sm qalınlığında beton hazırlıq qatı verilməlidir

## Layihənin tətbiqi şəraiti:

| | | |
|---|---|---|
| Tikinti rayonunun seysmikliyi | -- | 8 ball Az. DTN 2.3-1 |
| Havanın xarici hesabi temperaturu | -- | -4° |
| İqlim şəraiti rayonu | -- | IV B |
| Qar örtüyü | -- | 80,0 kq /m² |
| Külək örtüyü | -- | 73,0 kq/m² |

9. Sahədə qazılmış quyularda yeraltı qrunt suların aşkar edilməmişdir.

İşlənmiş cizgilər fəaliyyətdə olan norma və qaydalara uyğun gəlir və bina , tikili və qurğuların istismarı zamanı partlayış və yanğından mühafizəni təmin edən tədbirləri nəzərdə tutur.

Layihənin baş mühəndisi Musayeva G.

| | | | | | | | |
|---|---|---|---|---|---|---|---|
| | | | | | | Sifarişçi: Cəfərov Mədət İslam oğlu | DK-MK |
| Dəyiş | Sh.sən | Vərəq | Sən.№ | İmza | Tarix | Abşeron rayonu, Qobu qəsəbəsində yerləşən torpaq sahəsində tikintisi nəzərdə tutulan anbar və inzibati binası anbar binası. | |
| L.B.M. | | G. Musayeva | | | | Anbar binası | Mərhələ: İ.L. / Vərəq: 1 / Vərəqlər |
| Konstruktor | | M. Əzizov | | | | | |
| Norm. nəzarət | | S. Şükürova | | | | Ümumi verilənlər | "STORM BUİLDİNG" MMC |

Format A3

Razılaşdırılmışdır

İnvent № Əvəzinə

İmza və Tarix

İnvent № İmza

# Çalanın yerləşmə planı

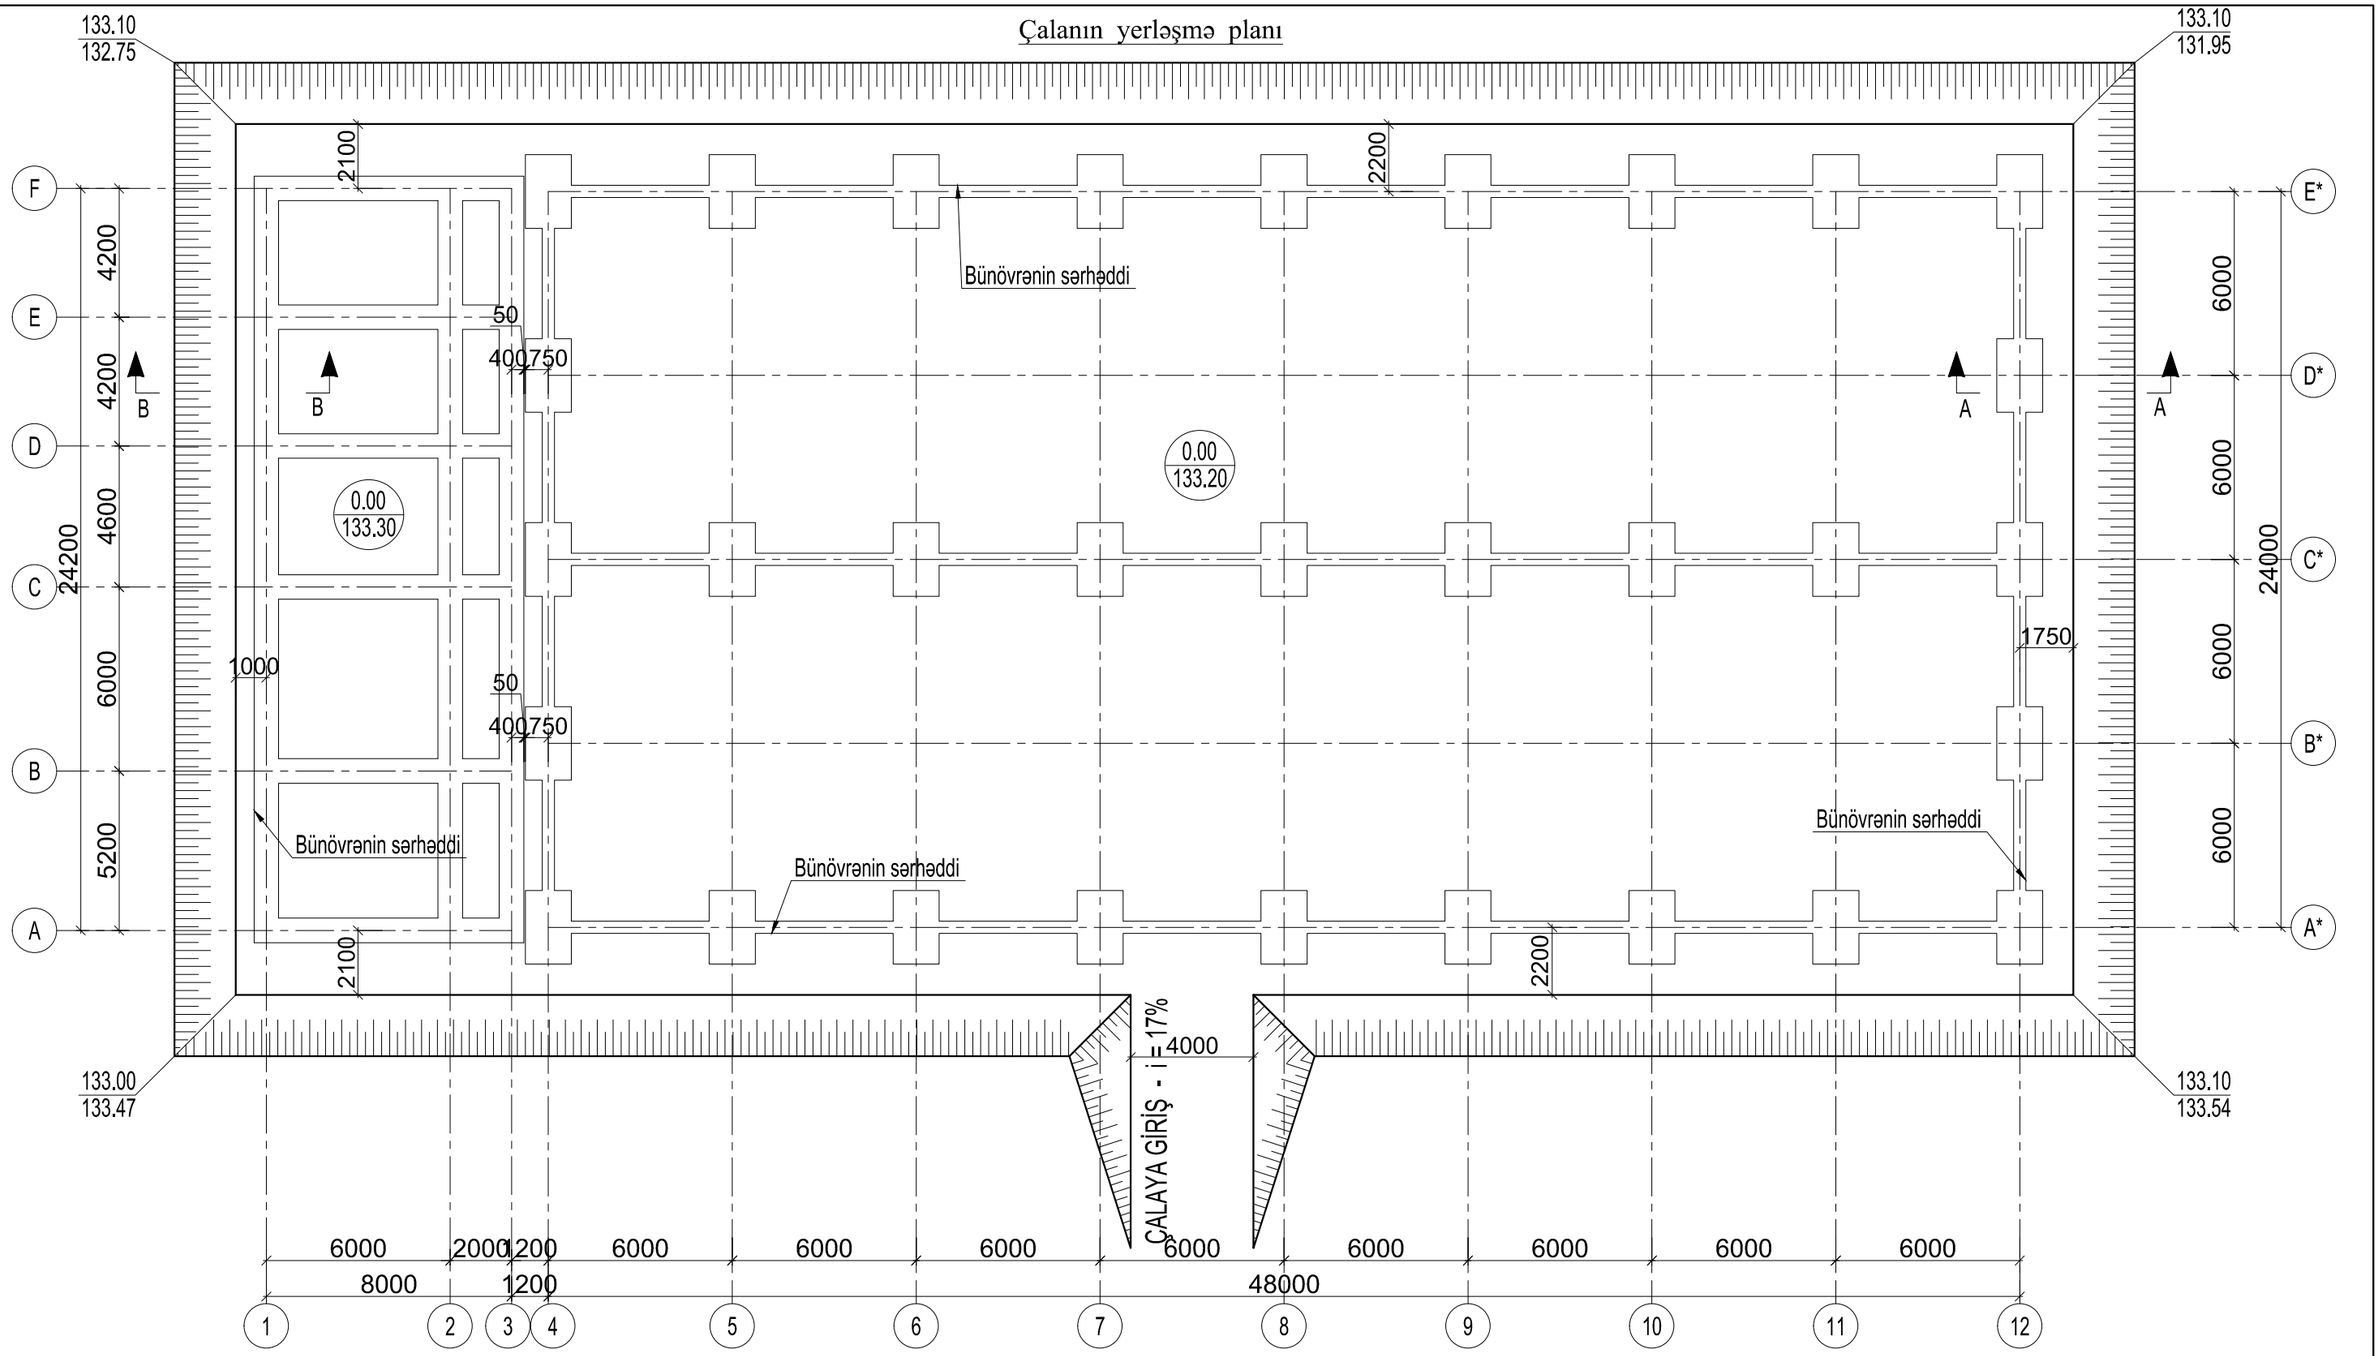


## QEYDLƏR:

1. LAYİHƏ MEMARLIQ CİZGİLƏRİ ƏSASINDA YERİNƏ YETİRİLİB.
2. 0.00 NİSBİ YÜKSƏKLİYİ 1-Cİ MƏRTƏBƏNİN DÖŞƏMƏ SƏVİYYƏSİ KİMİ QƏBUL EDİLİB
3. QRUNT ƏSASININ , GEOLOJİ TƏDQİQATLARIN NƏTİCƏSİNƏ UYĞUNSUZLUĞU OLARSA , ÖZÜL KONSTRUKSİYASI LAYİHƏ İNSTİTUNUN VƏ YA LAYİHƏ FİRMASININ İŞTİRAKI İLƏ YENİDƏN HƏLL EDİLMƏLİDİR.
4. SAHƏNİN SEYSMİKLİYİ 8 BALDIR.
5. ÖZÜL QALINLIĞI 500 mm OLAN MONOLİT D/B BAŞMAQ VƏ QALINLIĞI 400 mm OLAN LENTA ŞƏKLİNDƏ LAYİHƏLƏNDİRİLİB.
6. TİKİNTİ İŞLƏRİNƏ BAŞLAMAZDAN ƏVVƏL ƏLAQƏDAR TƏŞKİLATLARIN VƏ SİFARİŞÇİNİN İŞTİRAKI İLƏ TORPAQ İŞLƏRİNİN APARILMASINA İCAZƏ VERƏN MÜƏYYƏN AKT TƏRTİB EDİLMƏLİDİR.
7. KATLAVANIN DİBİ QAZILARAQ LAYİHƏ SƏVİYYƏSİNƏ ÇATDIRILDIQDAN SONRA KATLAVANIN İÇİNDƏ HƏR 4-5 M-DƏN BİR DƏRİNLİYİ 3 M, DİAMETRİ 150-200 MM OLAN QUYULAR QAZILMALIDIR. SONRADAN KATLAVANIN DİB SƏVİYYƏSİNDƏN 30 SM YUXARI ÇIXMAQ ŞƏRTİ İLƏ SU İLƏ DOLDURULMALIDIR. DOLDURULAN SU QRUNTA HOPDUQDAN SONRA KATLAVAN DİBİNDƏ YARANMIŞ PALÇIQ (STRULTURUNU İTİRMİŞ GİL), LİLLİ PALÇIQ KATLAVANDAN TƏMİZLƏNMƏLİDİR. ÜMUMİLİKDƏ BU PROSES 2 DƏFƏ GÖRÜLMƏLİDİR. KATLAVANIN DİBİ LAYİHƏ SƏVİYYƏSİNƏ ÇATDIRILMAQ ÜÇÜN QIRMADAŞ VƏ ŞİŞMƏYƏN GİL QARIŞIĞI (70 / 30 NİSBƏTİNDƏ) İLƏ HƏR 200 MM-DƏN BİR KİPLƏŞDİRİLƏRƏK YAYILMALIDIR.

| Dəyiş | Sh.sən | Vərəq | Sən.№ | İmza | Tarix |
|---|---|---|---|---|---|
| L.B.M. | | G. Musayeva | | | |
| Konstruktor | | M. Əzizov | | | |
| Norm. nəzarət | | S. Şükürova | | | |

Sifarişçi: Cəfərov Mədət İslam oğlu — DK-MK

Abşeron rayonu, Qobu qəsəbəsində yerləşən torpaq sahəsində tikintisi nəzərdə tutulan anbar və inzibati binası anbar binası.

| Anbar binası | Mərhələ | Vərəq | Vərəqlər |
|---|---|---|---|
| | İ.L. | 2 | |

Çalanın yerləşmə planı — "STORM BUİLDİNG" MMC

Format A3

Razılaşdırılmışdır

İnvent № Əvəzinə

İmza və Tarix

İnvent № İmza

# Kəsik A-A

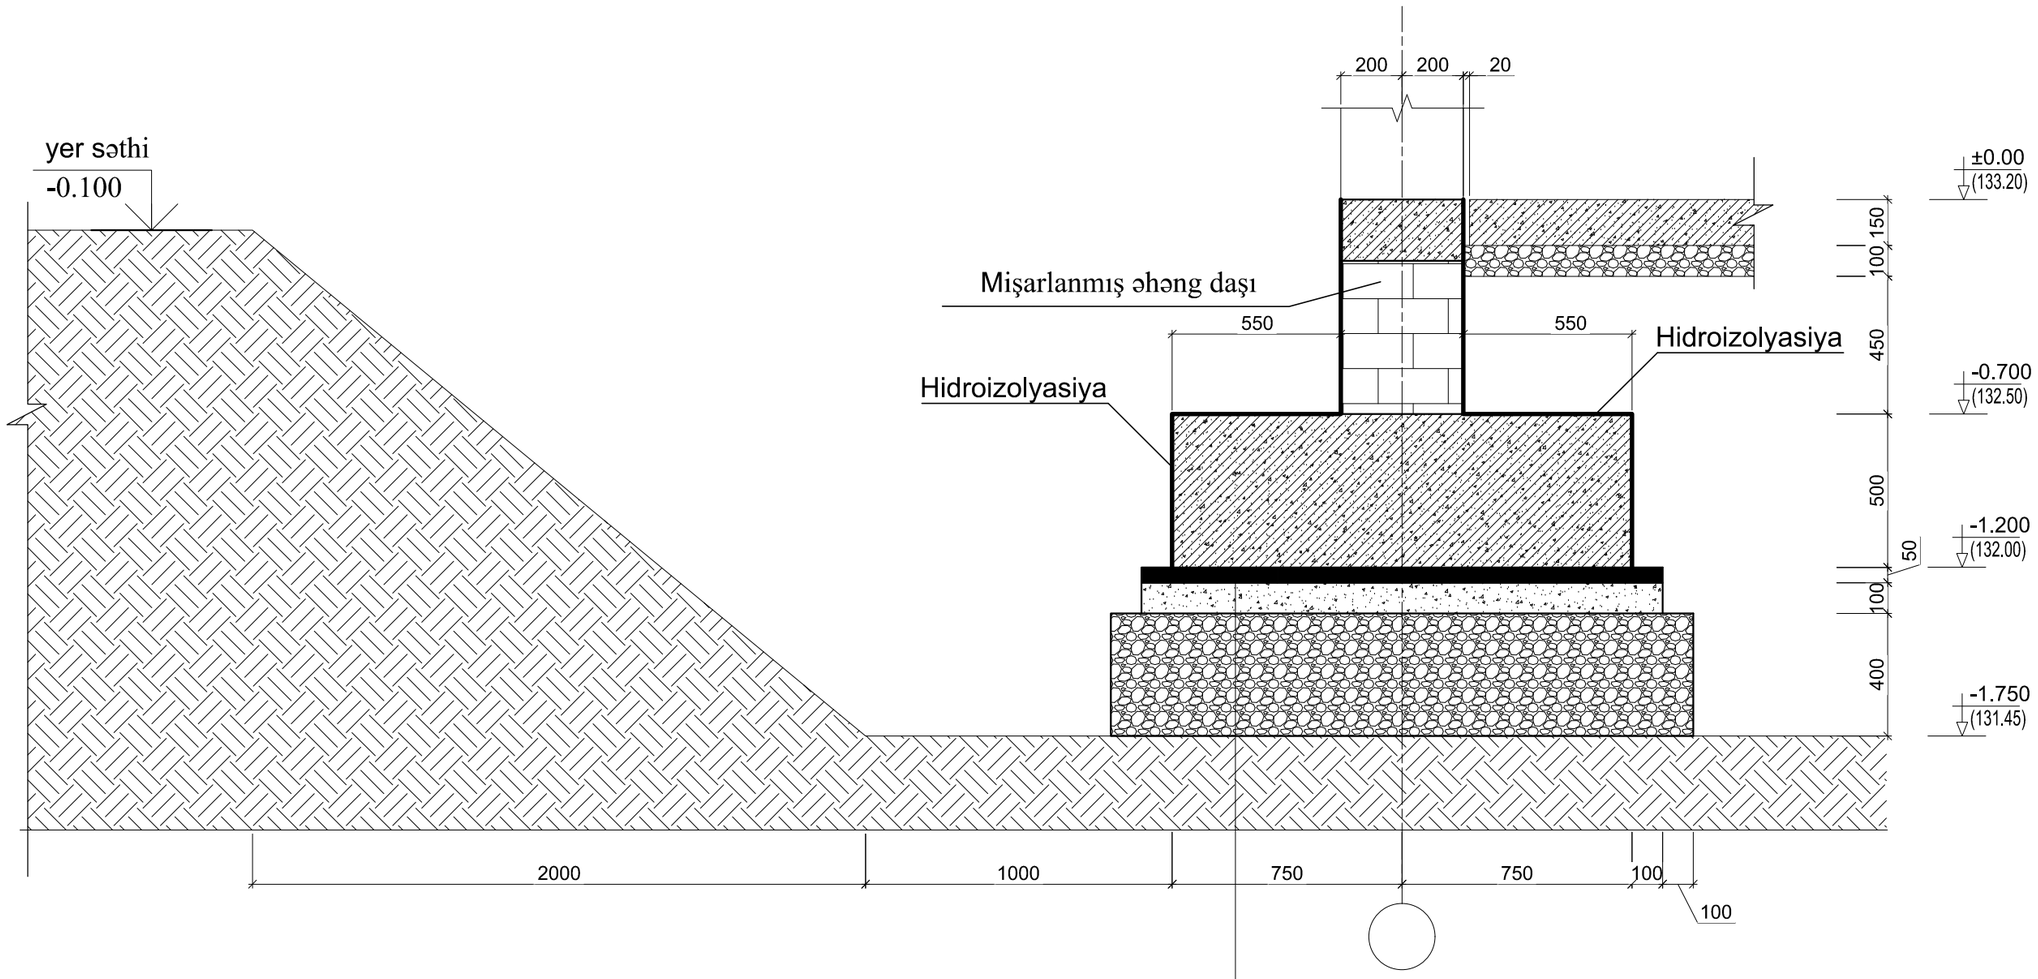


Monolit d/b bünövrə (Başmaq tipli). h=500 mm

Sementdən mühafizə qatı. h=50mm

Hidroizolyasiya 2 qat ruberoid yapışdırma yolu ilə.

Beton hazıqlıq qatı betonun sinfi B7.5 h=100mm

Qrunta toxaclanmış çaqıl-çınqıl qatı. h=400 mm

Kipləşdirilmiş qrunt.

**Qeyd :** 1. Bu vərəq "DK - 2 " vərəqi ilə birgə oxunmalıdır.

| Dəyiş | Sh.sən | Vərəq | Sən.№ | İmza | Tarix |
|---|---|---|---|---|---|
| L.B.M. | | G. Musayeva | | | |
| Konstruktor | | M. Əzizov | | | |
| Norm. nəzarət | | S. Şükürova | | | |

Sifarişçi: Cəfərov Mədət İslam oğlu — DK-MK

Abşeron rayonu, Qobu qəsəbəsində yerləşən torpaq sahəsində tikintisi nəzərdə tutulan anbar və inzibati binası anbar binası.

| Anbar binası | Mərhələ | Vərəq | Vərəqlər |
|---|---|---|---|
| | İ.L. | 3 | |

Kəsik A-A — "STORM BUİLDİNG" MMC

Format A3

Razılaşdırılmışdır

İnvent № Əvəzinə

İmza və Tarix

İnvent № İmza

# Kəsik B-B

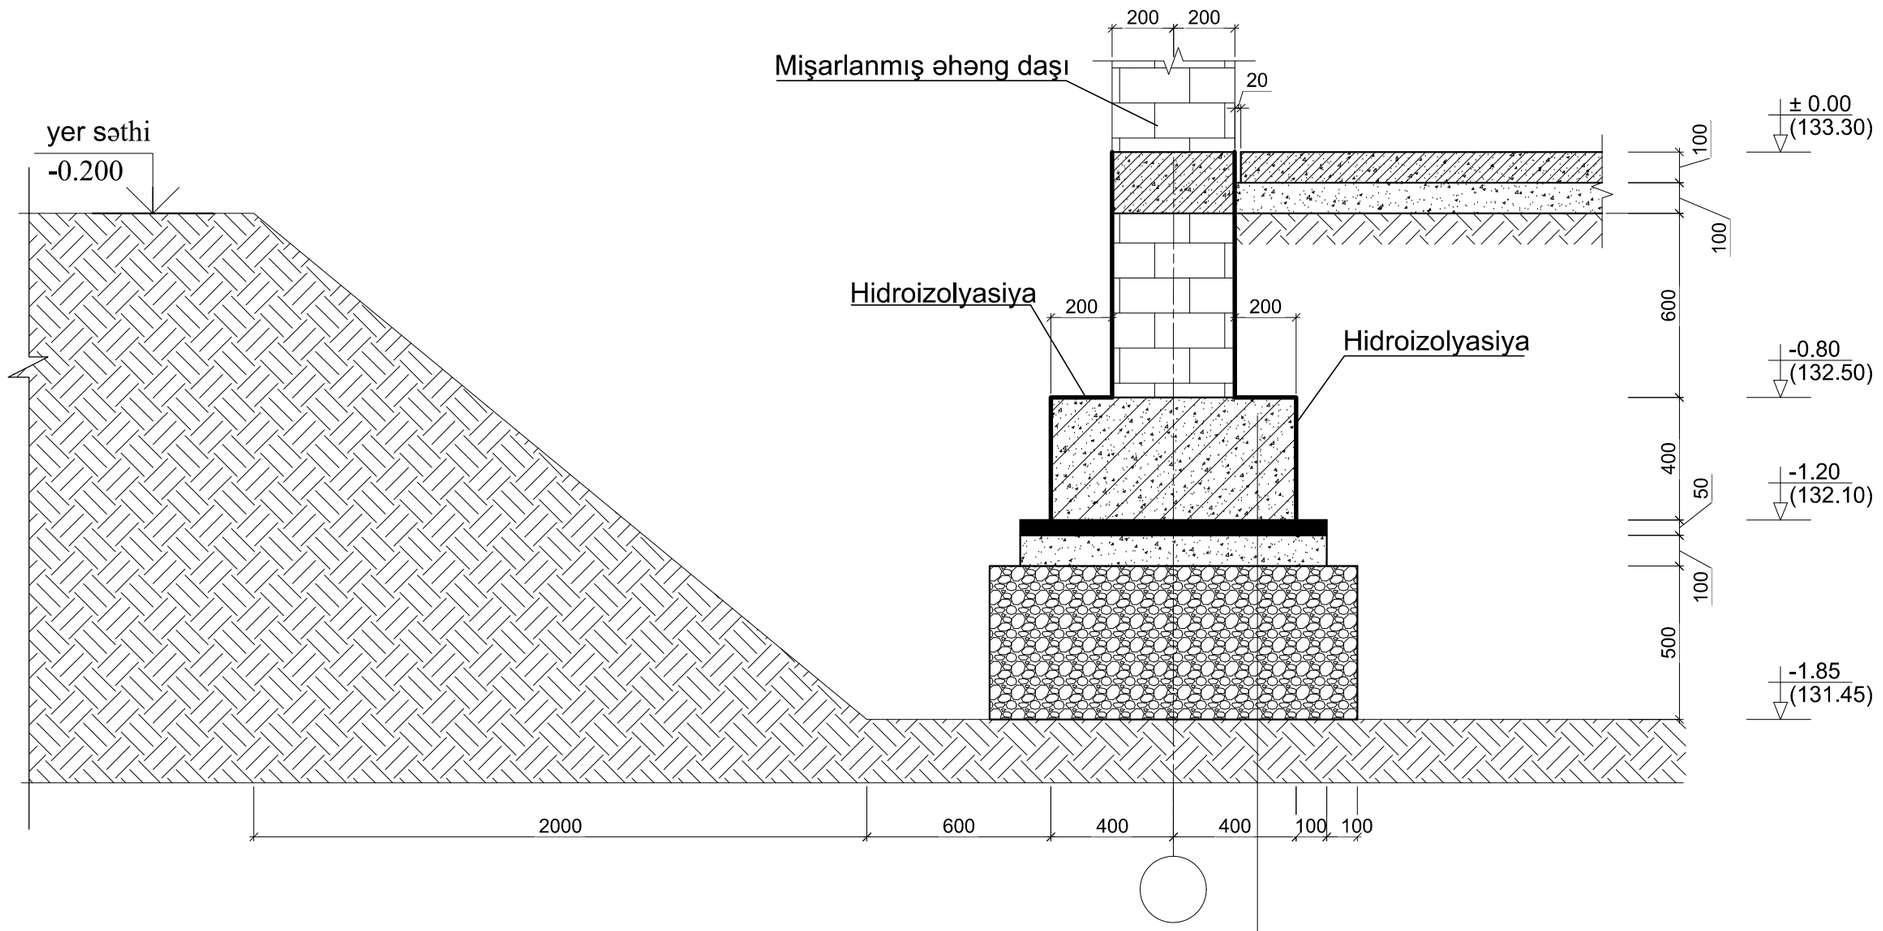


Monolit d/b bünövrə (Lentvari). h=400 mm

Sementdən mühafizə qatı. h=50mm

Hidroizolyasiya 2 qat ruberoid yapışdırma yolu ilə.

Beton hazıqlıq qatı betonun sinfi B7.5 h=100mm

Qrunta toxaclanmış çaqıl-çınqıl qatı. h=500 mm

Kipləşdirilmiş qrunt.

**Qeyd :** 1. Bu vərəq "DK - 2 " vərəqi ilə birgə oxunmalıdır.

| Dəyiş | Sh.sən | Vərəq | Sən.№ | İmza | Tarix |
|---|---|---|---|---|---|
| L.B.M. | | G. Musayeva | | | |
| Konstruktor | | M. Əzizov | | | |
| Norm. nəzarət | | S. Şükürova | | | |

Sifarişçi: Cəfərov Mədət İslam oğlu — DK-MK

Abşeron rayonu, Qobu qəsəbəsində yerləşən torpaq sahəsində tikintisi nəzərdə tutulan anbar və inzibati binası anbar binası.

| Anbar binası | Mərhələ | Vərəq | Vərəqlər |
|---|---|---|---|
| | İ.L. | 4 | |
| Kəsik B-B | "STORM BUİLDİNG" MMC | | |

Razılaşdırılmışdır

İnvent № Əvəzinə

İmza və Tarix

İnvent № İmza

Format A3

Monolit D/B lentvari bünövrə və başmaqların yerləşmə planı

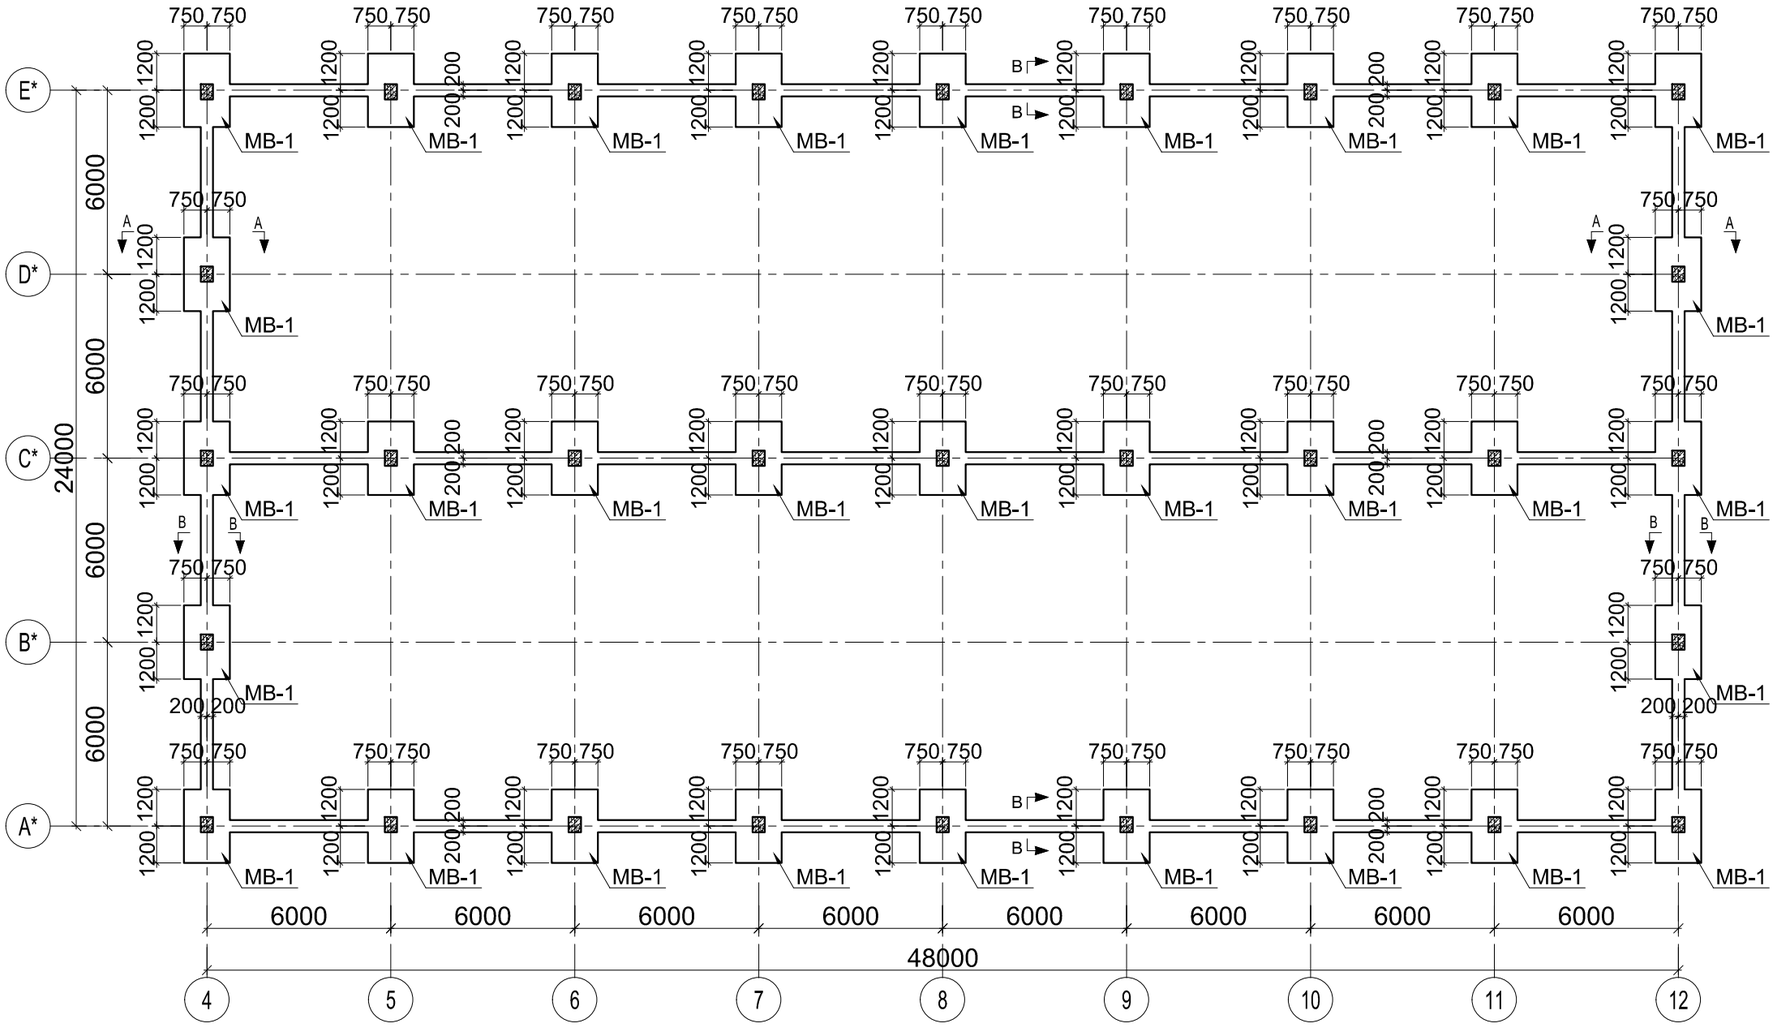


Armaturların əyilməsi

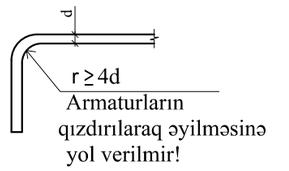


Düyün - 1

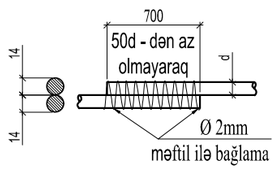


Monolit dəmir - beton elementlərin təsnifatı

| Format | Zona | Mövqe | İşarə | Adı | Miqdarı | Qeyd |
|---|---|---|---|---|---|---|
| Monolit dəmir-beton lentvari bünövrə və başmaqlar | | | | | | |
| | | | | Lentavri bünövrə -"LB-1" (400x500(h)) | - | 192.00 p.m |
| | | | | D/b Başmaq "MB-1" -(1500x2400x500(h)) | 31 | |

| | | | | | | | |
|---|---|---|---|---|---|---|---|
| | | | | | | Sifarişçi: Cəfərov Mədət İslam oğlu | DK-MK |
| Dəyiş | Sh.sən | Vərəq | Sən.№ | İmza | Tarix | Abşeron rayonu, Qobu qəsəbəsində yerləşən torpaq sahəsində tikintisi nəzərdə tutulan anbar və inzibati binası anbar binası. | |
| L.B.M. | | G. Musayeva | | | | Anbar binası | Mərhələ: İ.L. |
| Konstruktor | | M. Əzizov | | | | | Vərəq: 5 |
| Norm. nəzarət | | S. Şükürova | | | | Monolit D/B lentvari bünövrə və başmaqların yerləşmə planı | "STORM BUİLDİNG" MMC |

Razılaşdırılmışdır

İnvent № Əvəzinə

İmza və Tarix

İnvent № İmza

Format A3

## Kəsik A-A

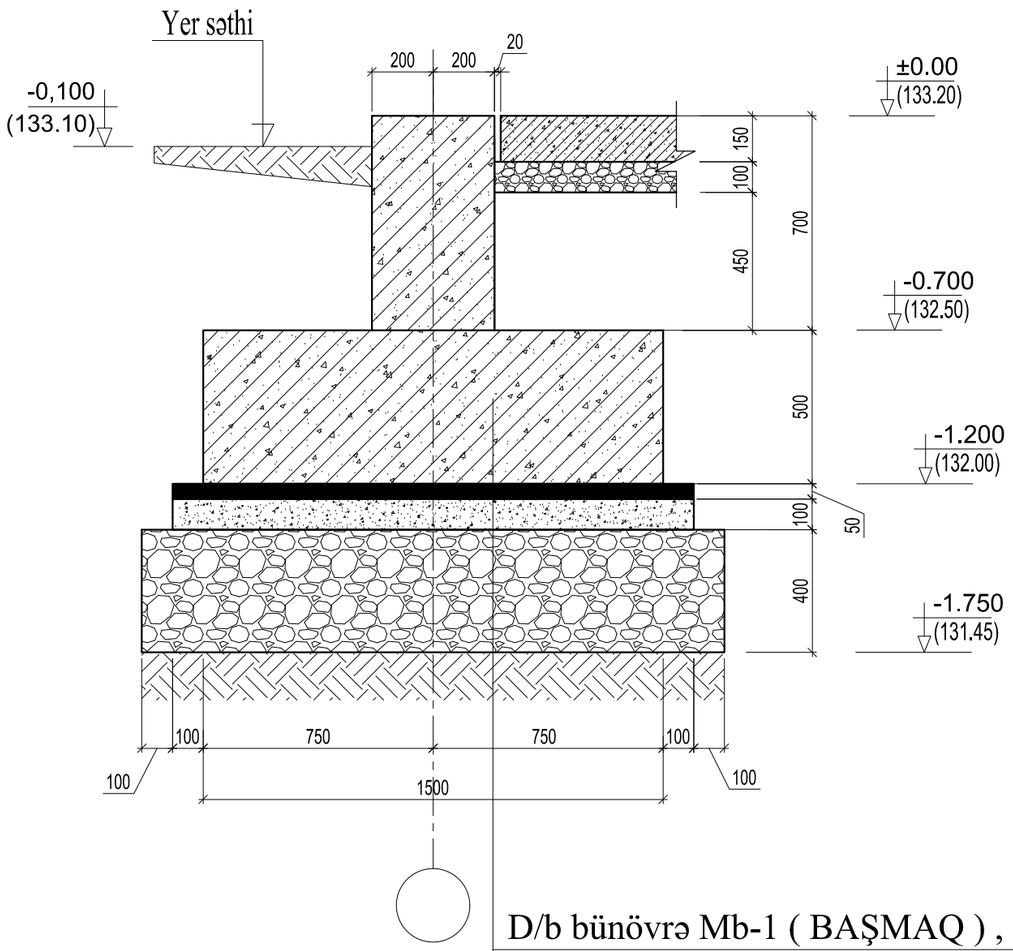


D/b bünövrə Mb-1 ( BAŞMAQ ) , H=500 mm

Sement-qum məhlulu - H=50 mm

İsti bitumla sərt yapişdirilmiş 2 qat ruberoid

Beton hazirliq qati (B7.5) h=100 mm

Çaqıl çınqıl qatı h=400 mm

Kipləşdirilmiş qrunt

## Kəsik B-B

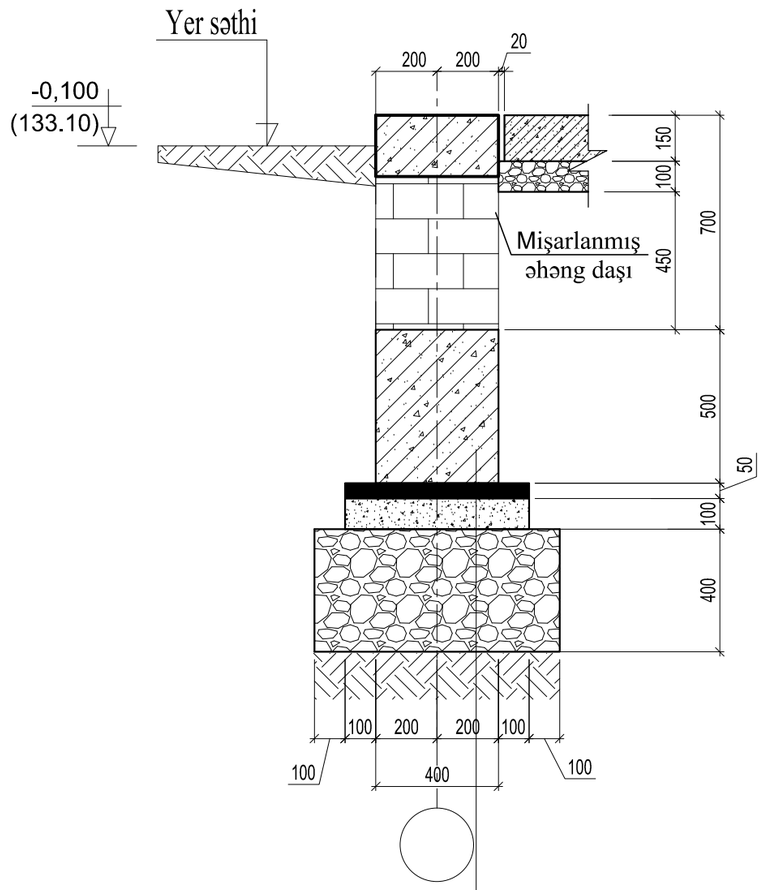


D/b bünövrə Mb-1 , H=500 mm

Sement-qum məhlulu - H=50 mm

İsti bitumla sərt yapişdirilmiş 2 qat ruberoid

Beton hazirliq qati (B7.5) h=100 mm

Çaqıl çınqıl qatı h=400 mm

Kipləşdirilmiş qrunt

| | | | | | | | |
|---|---|---|---|---|---|---|---|
| | | | | | | Sifarişçi: Cəfərov Mədət İslam oğlu | DK-MK |
| Dəyiş | Sh.sən | Vərəq | Sən.№ | İmza | Tarix | Abşeron rayonu, Qobu qəsəbəsində yerləşən torpaq sahəsində tikintisi nəzərdə tutulan anbar və inzibati binası anbar binası. | |
| L.B.M. | | G. Musayeva | | | | Anbar binası | Mərhələ: İ.L. / Vərəq: 6 / Vərəqlər |
| Konstruktor | | M. Əzizov | | | | | |
| Norm. nəzarət | | S. Şükürova | | | | Bünövrə kəsikləri: Kəsik A-A;B-B | "STORM BUİLDİNG" MMC |

Format A3

Razılaşdırılmışdır

İnvent № Əvəzinə

İmza və Tarix

İnvent № İmza

Monolit d/b başmaq MB-1

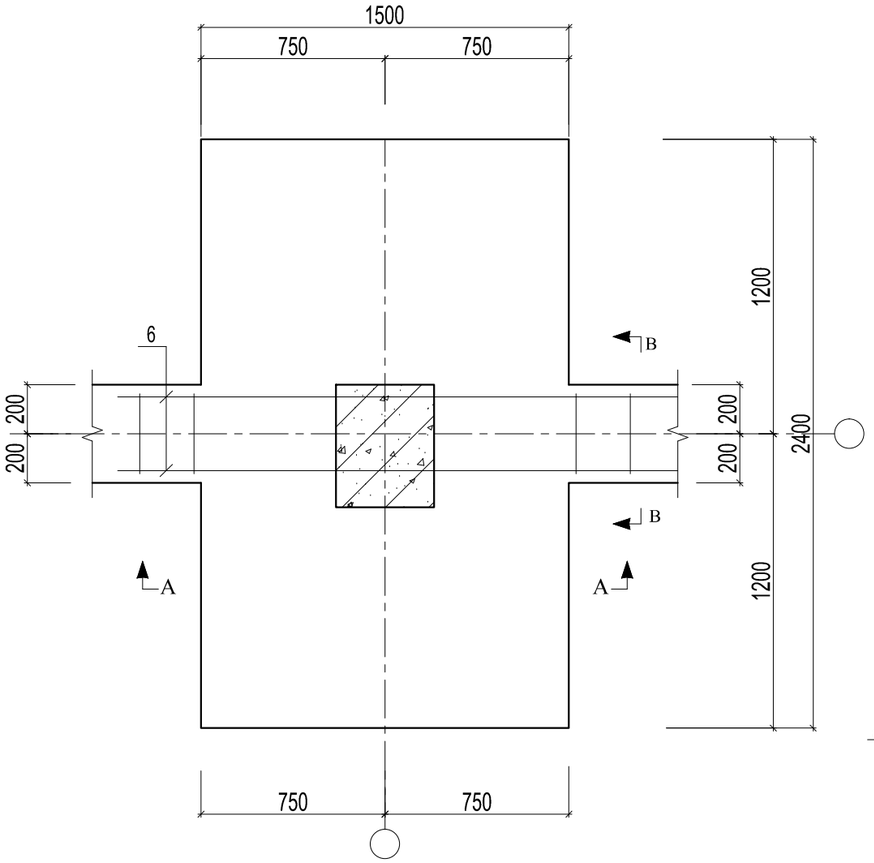


Kəsik B-B

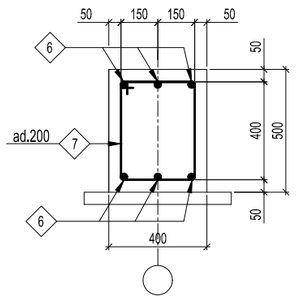


Kəsik A-A

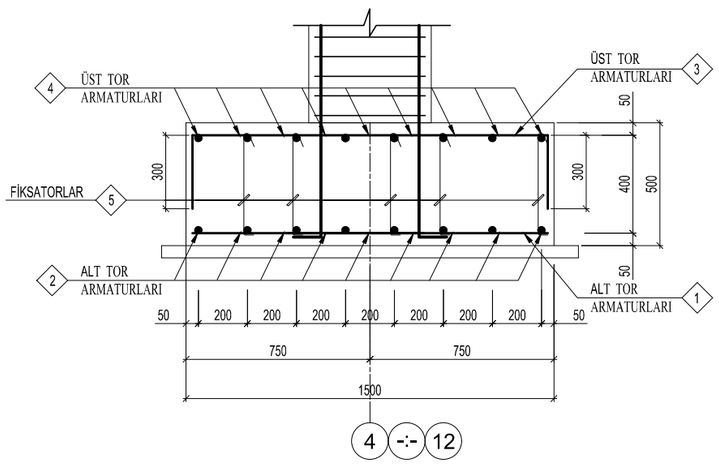


Detallar cədvəli

| MÖVQE | ESKİZ |
|---|---|
| 1,3 | 1400; 300; 300 |
| 2,4 | 2300; 300; 300 |
| 5 | 100; 420; 110 |
| 7 | 450; 450; 550; 350 |

Materialların təsnifatı

| Format | Zona | Mövqe | İşarəsi | Adı | Miq. | Qeyd |
|---|---|---|---|---|---|---|
| | | | | Monolit D/B başmaq MB-1 | 31 | |
| | | 1 | DÜİST 52544-2006 | Ø14A500C , L=2000 mm | 12 | 2.42 / 29.04 |
| | | 2 | DÜİST 52544-2006 | Ø14 A500C , L=2900 mm | 8 | 3.50 / 31.50 |
| | | 3 | DÜİST 52544-2006 | Ø14 A500C , L=2000 mm | 12 | 2.42 / 29.04 |
| | | 4 | DÜİST 52544-2006 | Ø14 A500C , L=2900 mm | 9 | 3.50 / 31.50 |
| | | 5 | DÜİST 52544-2006 | Ø14 A500C , L=730 mm | 23 | 0,9 / 20.70 |
| | | | | Material: Beton B25 | | 1.80 m³ |
| | | | | Lentvari monolit D/B bünövrə | | |
| | | 6 | DÜİST 52544-2006 | Ø14 A500C , $L_{üm}$=1210.00 p.m | -- | ---- / 1461.70 |
| | | 7 | DÜIST 5781-82* | Ø8 A-I (A240), L =1800 mm | 960 | 0.71 / 682.60 |
| | | | | Material: Beton B25 | | 38.40 m³ |

Polad sərfi cədvəli, kq.

| Elementin markası | Armatur məmulatları | | | | | | | | Yekun |
|---|---|---|---|---|---|---|---|---|---|
| | Armaturun sinfi | | | | | | | | |
| | A-I A(240) | | | A500C | | | | | |
| | DÜIST 5781-82* | | | DÜIST 52544-2006 | | | | | |
| | Ø8 | | Cəmi: | Ø14 | Ø16 | Ø18 | Ø22 | Cəmi: | |
| Monolit D/B başmaq MB-1 (31 ədəd üç.) | 0.0 | | 0.0 | 3753.48 | | | | 3753.48 | 3753.48 |
| Monolit D/B Lentavri bünövrə | 682.60 | | 682.60 | 1461.70 | | | | 1461.70 | 2144.30 |

| Dəyiş | Sh.sən | Vərəq | Sən.№ | İmza | Tarix |
|---|---|---|---|---|---|
| L.B.M. | | G. Musayeva | | | |
| Konstruktor | | M. Əzizov | | | |
| Norm. nəzarət | | S. Şükürova | | | |

Sifarişçi: Cəfərov Mədət İslam oğlu

DK-MK

Abşeron rayonu, Qobu qəsəbəsində yerləşən torpaq sahəsində tikintisi nəzərdə tutulan anbar və inzibati binası anbar binası.

Anbar binası

| Mərhələ | Vərəq | Vərəqlər |
|---|---|---|
| İ.L. | 7 | |

Monolit d/b lentvari bünövrə. Başmaq MB-1

"STORM BUİLDİNG" MMC

Format A3

Razılaşdırılmışdır

İnvent № Əvəzinə

İmza və Tarix

İnvent № İmza

"±0.00" Səviyyəsində monolit d/b döşəmə və d/b kəmərin yerləşmə planı

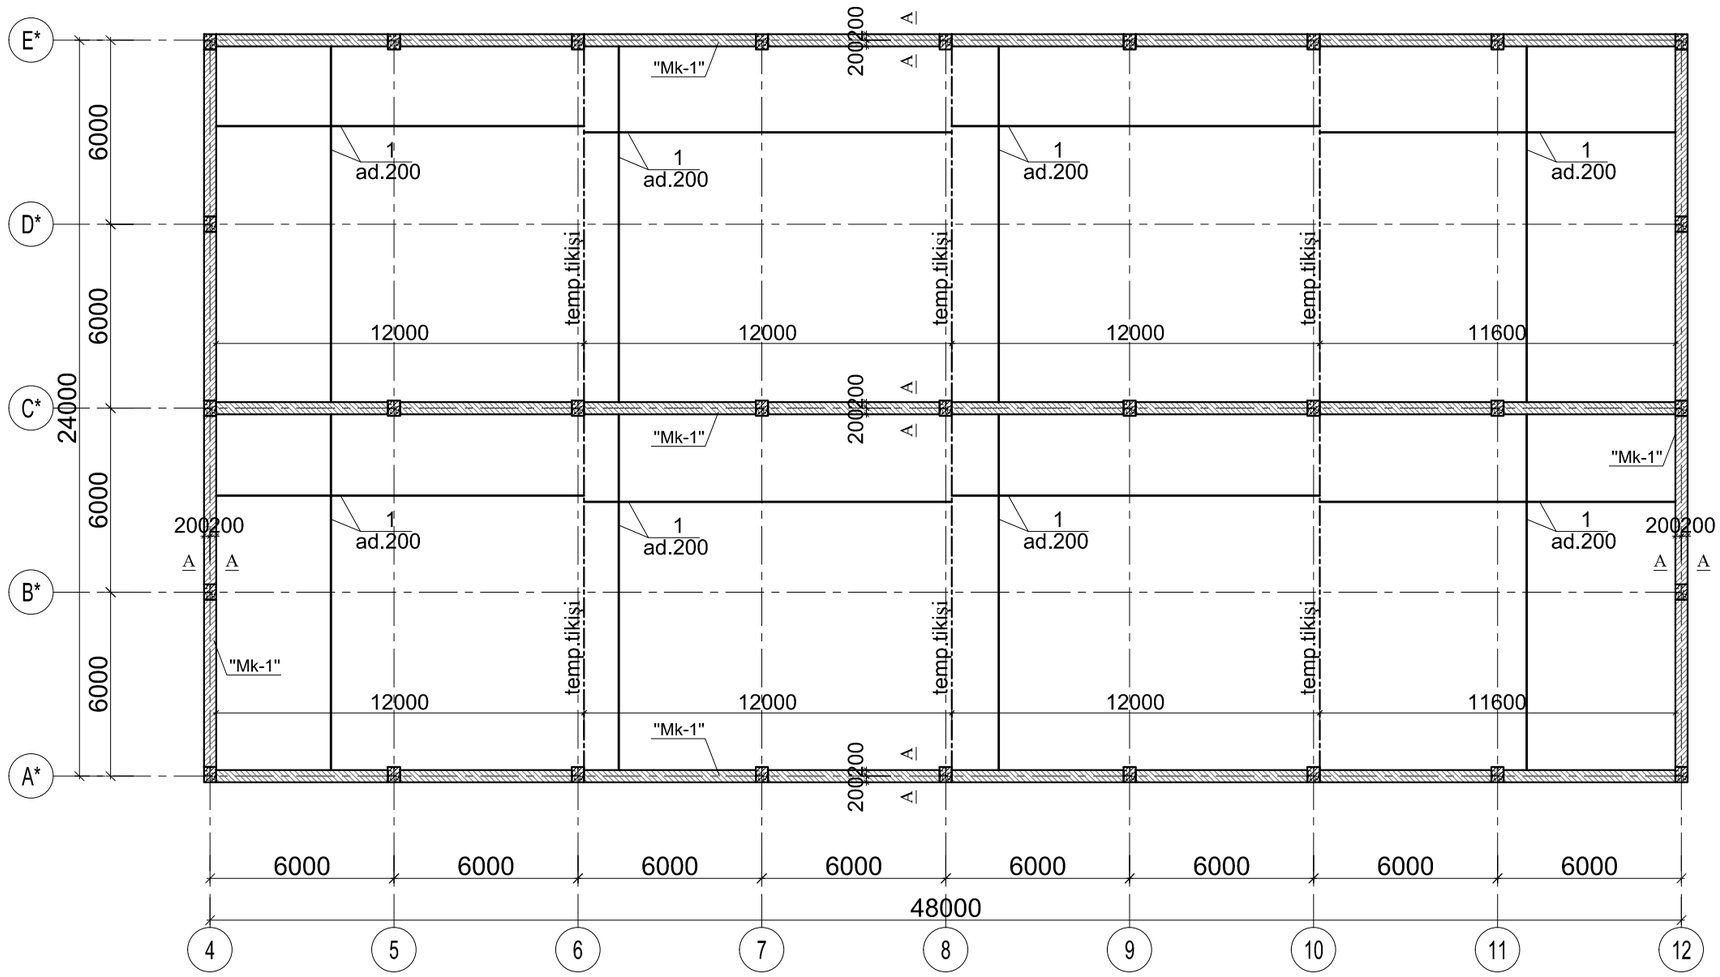


**Armaturların əyilməsi**

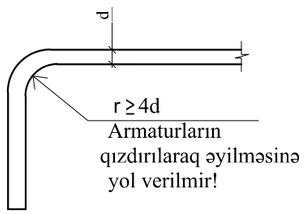


Armaturların calaq fraqmenti

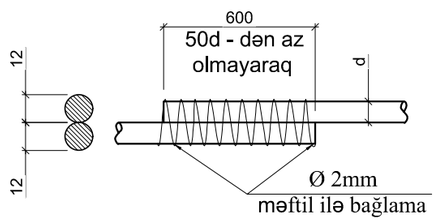


Qeyd.
Döşəmədə 12 m-dən bir temperatur tikişi verilməlidir.

| | | | | | | | |
|---|---|---|---|---|---|---|---|
| | | | | | | Sifarişçi: Cəfərov Mədət İslam oğlu | DK-MK |
| Dəyiş | Sh.sən | Vərəq | Sən.№ | İmza | Tarix | Abşeron rayonu, Qobu qəsəbəsində yerləşən torpaq sahəsində tikintisi nəzərdə tutulan anbar və inzibati binası anbar binası. | |
| L.B.M. | | G. Musayeva | | | | Anbar binası | Mərhələ: İ.L. / Vərəq: 8 / Vərəqlər |
| Konstruktor | | M. Əzizov | | | | | |
| Norm. nəzarət | | S. Şükürova | | | | "±0.00" Səviyyəsində monolit d/b döşəmə və d/b kəmərin yerləşmə planı | "STORM BUİLDİNG" MMC |

Format A3

Razılaşdırılmışdır

İnvent № Əvəzinə

İmza və Tarix

İnvent № İmza

## Monolit d\b döşəmənin armaturlanma kəsiyi

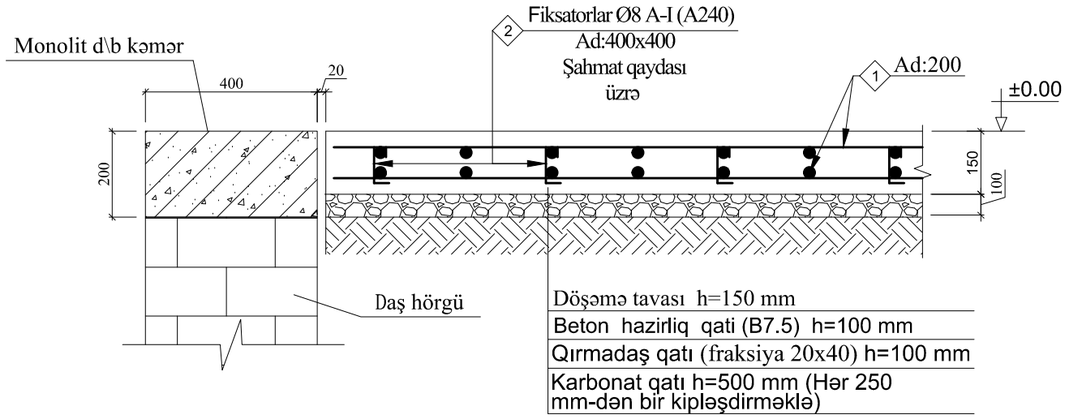


## Monolit d\b kəmər MK-1

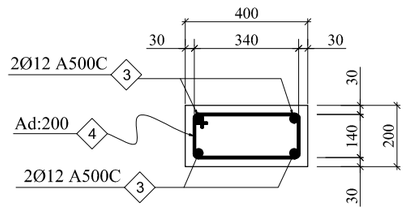


## Armaturların calaq fraqmenti

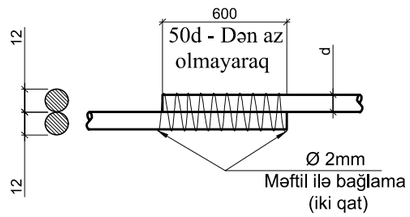


## DETALLAR CƏDVƏLİ.

| MÖVQE | CİZGİ |
|---|---|
| 2 | |
| 4 | 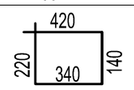  |

QEYD :
Monolit d/b kəmər ştrixlənmiş sahə ilə göstərilmişdir.

## Materialların təsnifatı

| Format | Zona | Mövqe | İşarəsi | Adı | Miq. | Qeyd |
|---|---|---|---|---|---|---|
| | | | | Monolit d/b döşəmə tavası | | 1109.10 $m^2$ |
| | | 1 | DÜİST 52544-2006 | Ø12 A500C , L=23292.00 pm | - | - / 20683.4 |
| | | 2 | DÜİST 5781-82* | Ø8 A-I (A240), L=260 mm | 6932 | 0.103 / 714.00 |
| | | | | Material.Beton B15 | - | 166.37 $m^3$ |
| | | | | Monolit d/b kəmər | | 192.00 m |
| | | 3 | DÜİST 52544-2006 | Ø12 A500C , L=2016.00 pm | | - / 1790.3 |
| | | 4 | DÜİST 5781-82* | Ø8 A-I (A240), L=1120 mm | 960 | 0.44 / 422.40 |
| | | | | Material.Beton B25 | - | 15.36 $m^3$ |

Polad sərfi cədvəli, kq

| Elementin markası | Armatur məmulatları | | | | | | | | |
|---|---|---|---|---|---|---|---|---|---|
| | Armaturun sinfi | | | | | | | | Yekun |
| | A-I A(240) DÜIST 5781-82* | | | A500C DÜIST 52544-2006 | | | | | |
| | Ø8 | | Cəmi: | Ø10 | Ø12 | Ø18 | Ø22 | Cəmi: | |
| Monolit d/b kəmər Mk-1 | 422.40 | | 422.40 | - | 1790.30 | - | - | 1790.30 | 2212.70 |
| Monolit d/b döşəmə tavası | 714.00 | | 714.00 | - | 10341.7 | - | - | 10341.7 | 11055.70 |

| Dəyiş | Sh.sən | Vərəq | Sən.№ | İmza | Tarix |
|---|---|---|---|---|---|
| L.B.M. | | G. Musayeva | | | |
| Konstruktor | | M. Əzizov | | | |
| Norm. nəzarət | | S. Şükürova | | | |

Sifarişçi: Cəfərov Mədət İslam oğlu

DK-MK

Abşeron rayonu, Qobu qəsəbəsində yerləşən torpaq sahəsində tikintisi nəzərdə tutulan anbar və inzibati binası anbar binası.

| Anbar binası | Mərhələ | Vərəq | Vərəqlər |
|---|---|---|---|
| | İ.L. | 9 | |

"±0.00" Səviyyəsində monolit d/b döşəmə və d/b kəmərin konstruksiyası

"STORM BUİLDİNG" MMC

Format A3

Razılaşdırılmışdır

İnvent № Əvəzinə

İmza və Tarix

İnvent № İmza

-0.70 səviyyəsində monolit d/b sütunların yerləşmə planı.

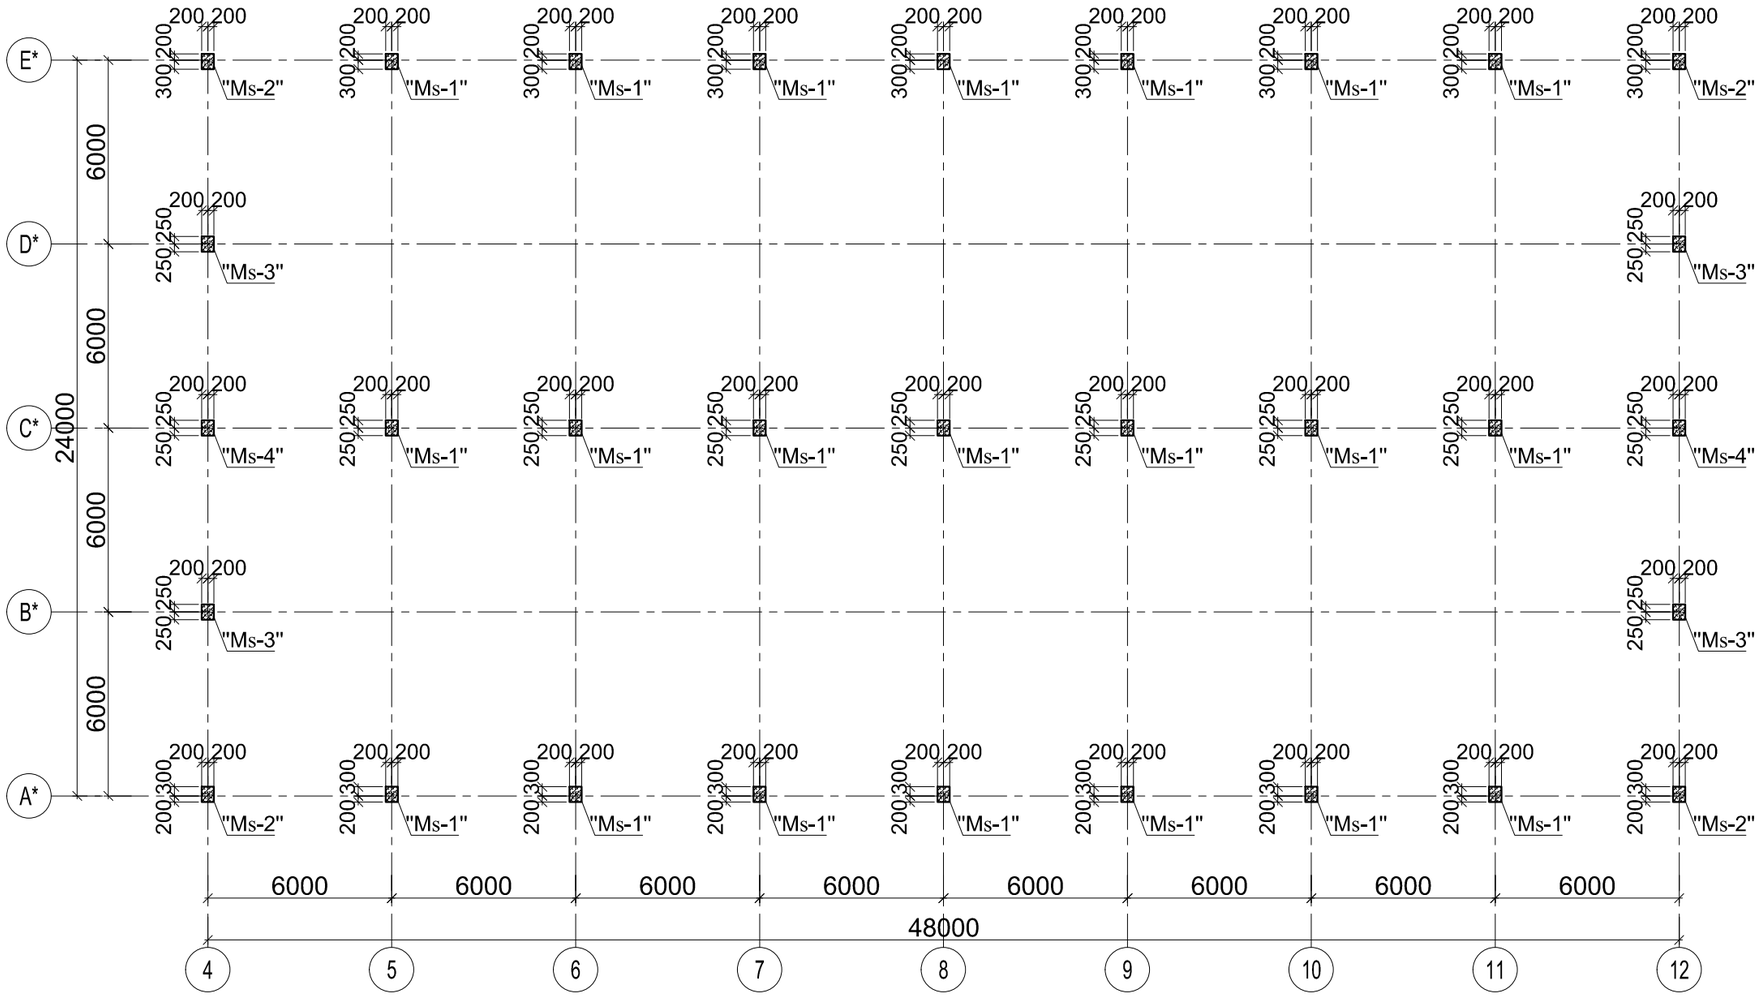


Monolit d/b elementlərin təsnifatı

| Format | Zona | Mövqe | İşarə | Adı | Miqdarı | Qeyd |
|---|---|---|---|---|---|---|
| | | | | Monolit d/b sütunlar | | |
| | | 1 | | Monolit d/b sütun Ms-1 | 21 | |
| | | 2 | | Monolit d/b sütun Ms-2 | 4 | |
| | | 3 | | Monolit d/b sütun Ms-3 | 4 | |
| | | 4 | | Monolit d/b sütun Ms-4 | 2 | |

| Dəyiş | Sh.sən | Vərəq | Sən.№ | İmza | Tarix |
|---|---|---|---|---|---|
| L.B.M. | | G. Musayeva | | | |
| Konstruktor | | M. Əzizov | | | |
| Norm. nəzarət | | S. Şükürova | | | |

Sifarişçi: Cəfərov Mədət İslam oğlu — DK-MK

Abşeron rayonu, Qobu qəsəbəsində yerləşən torpaq sahəsində tikintisi nəzərdə tutulan anbar və inzibati binası anbar binası.

Anbar binası

| Mərhələ | Vərəq | Vərəqlər |
|---|---|---|
| İ.L. | 10 | |

-0.70 səviyyəsində monolit d/b sütunların yerləşmə planı.

"STORM BUİLDİNG" MMC

Format A3

Razılaşdırılmışdır

İnvent № Əvəzinə

İmza və Tarix

İnvent № İmza

±0.00 səviyyəsində monolit d/b sütunların yerləşmə planı.

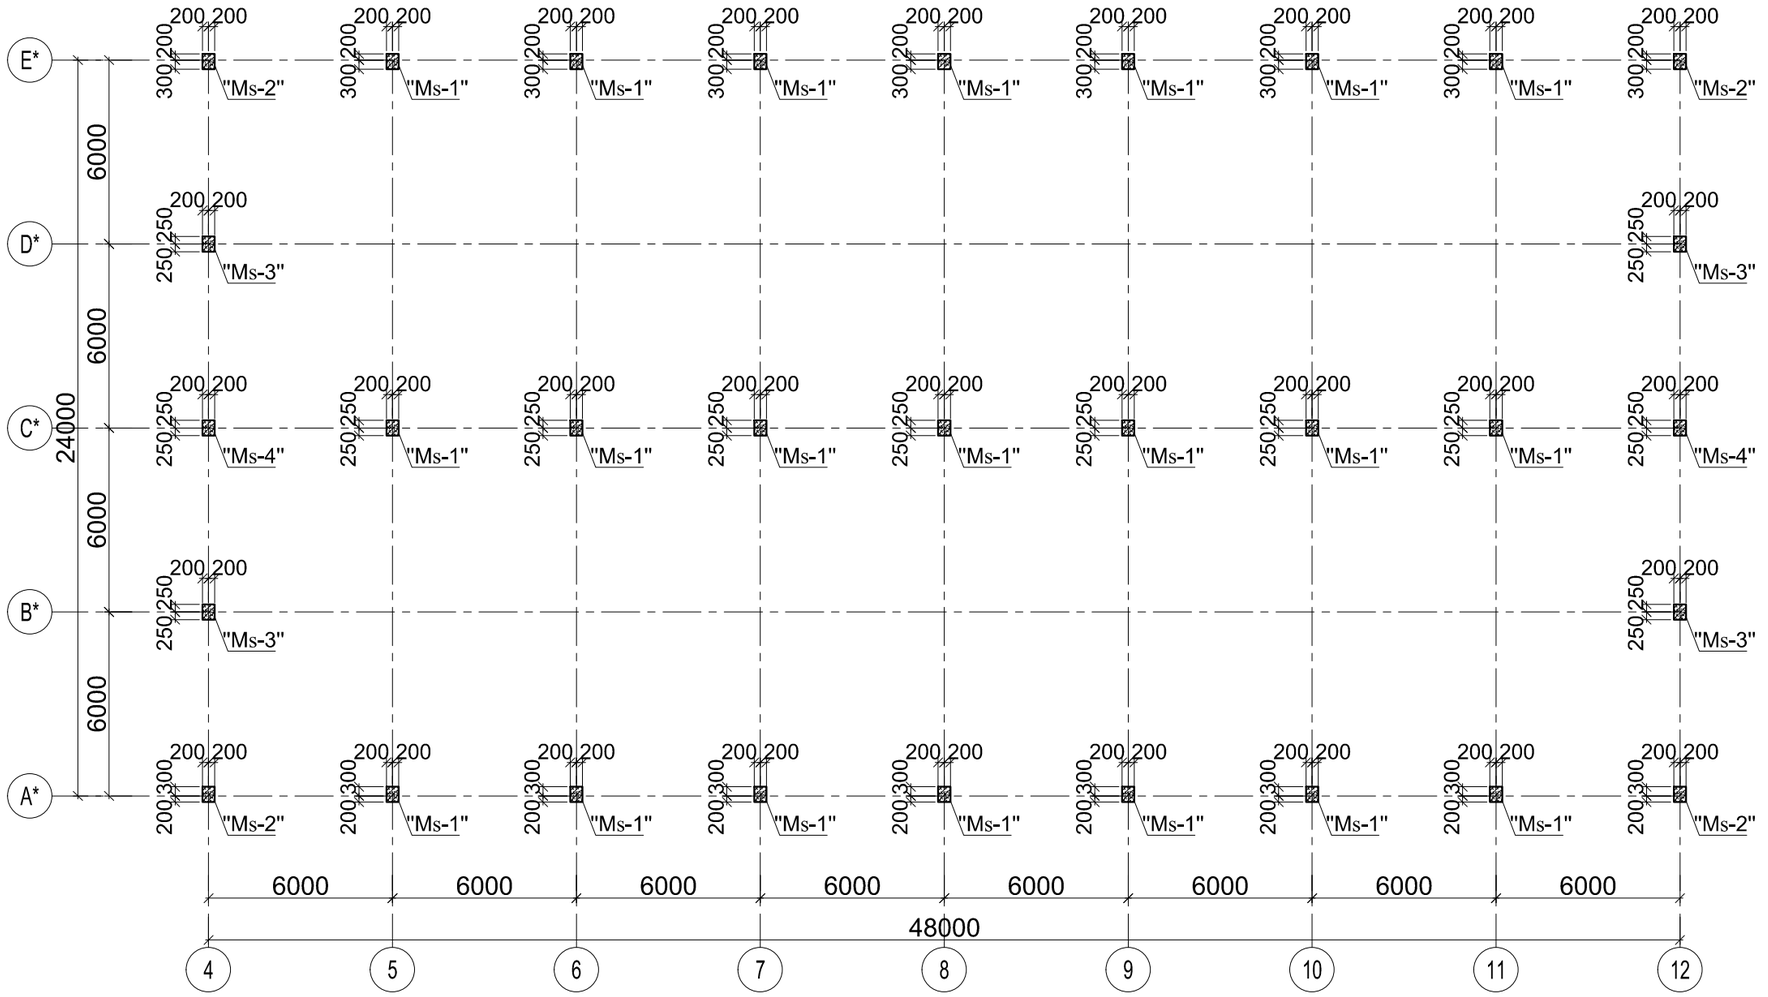


Razılaşdırılmışdır

İnvent № Əvəzinə

İmza və Tarix

İnvent № İmza

| | | | | | | | |
|---|---|---|---|---|---|---|---|
| | | | | | | Sifarişçi: Cəfərov Mədət İslam oğlu | DK-MK |
| Dəyiş | Sh.sən | Vərəq | Sən.№ | İmza | Tarix | Abşeron rayonu, Qobu qəsəbəsində yerləşən torpaq sahəsində tikintisi nəzərdə tutulan anbar və inzibati binası anbar binası. | |
| L.B.M. | | G. Musayeva | | | | Anbar binası | Mərhələ: İ.L. / Vərəq: 11 / Vərəqlər: |
| Konstruktor | | M. Əzizov | | | | | |
| Norm. nəzarət | | S. Şükürova | | | | ±0.00 səviyyəsində monolit d/b sütunların yerləşmə planı. | "STORM BUİLDİNG" MMC |

Format A3

+7.00 səviyyəsində monolit d/b sütunların yerləşmə planı.

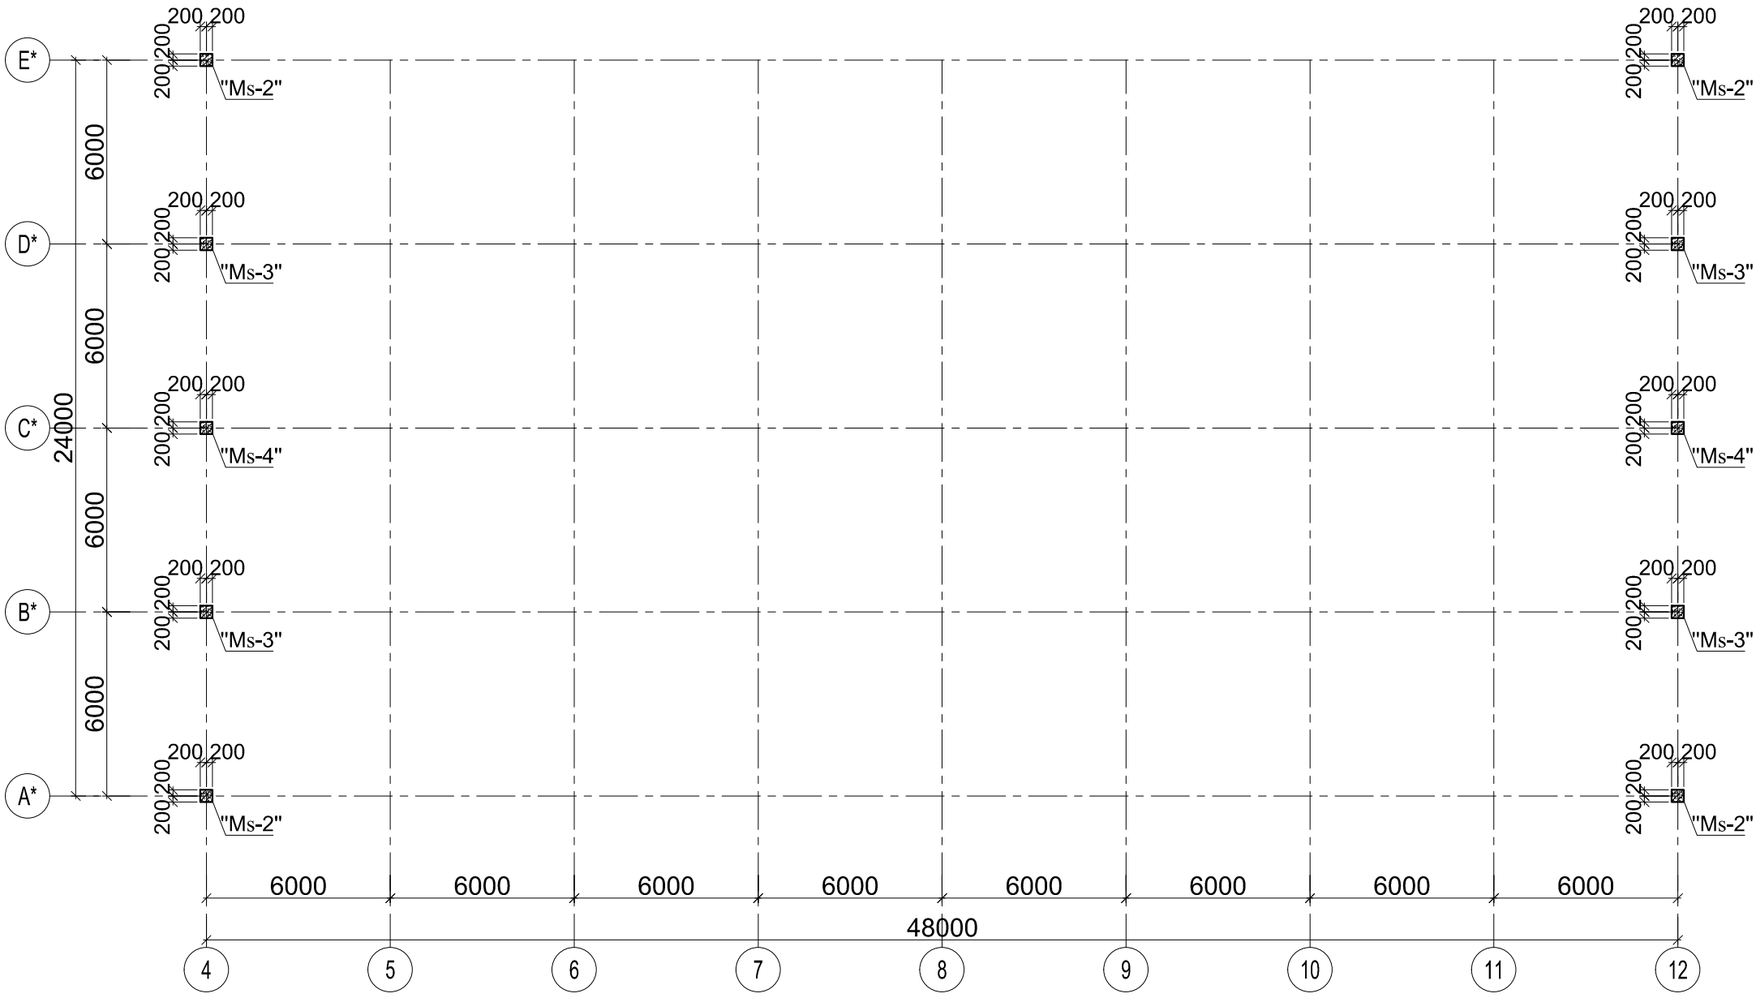


Razılaşdırılmışdır

İnvent № Əvəzinə

İmza və Tarix

İnvent № İmza

| | | | | | | | |
|---|---|---|---|---|---|---|---|
| | | | | | | Sifarişçi: Cəfərov Mədət İslam oğlu | DK-MK |
| Dəyiş | Sh.sən | Vərəq | Sən.№ | İmza | Tarix | Abşeron rayonu, Qobu qəsəbəsində yerləşən torpaq sahəsində tikintisi nəzərdə tutulan anbar və inzibati binası anbar binası. | |
| L.B.M. | | G. Musayeva | | | | Anbar binası | Mərhələ: İ.L. / Vərəq: 12 / Vərəqlər: |
| Konstruktor | | M. Əzizov | | | | | |
| Norm. nəzarət | | S. Şükürova | | | | +7.00 səviyyəsində monolit d/b sütunların yerləşmə planı. | "STORM BUİLDİNG" MMC |

Format A3

## Monolit d/b sütun "Ms-1"-in konstruksiyası.

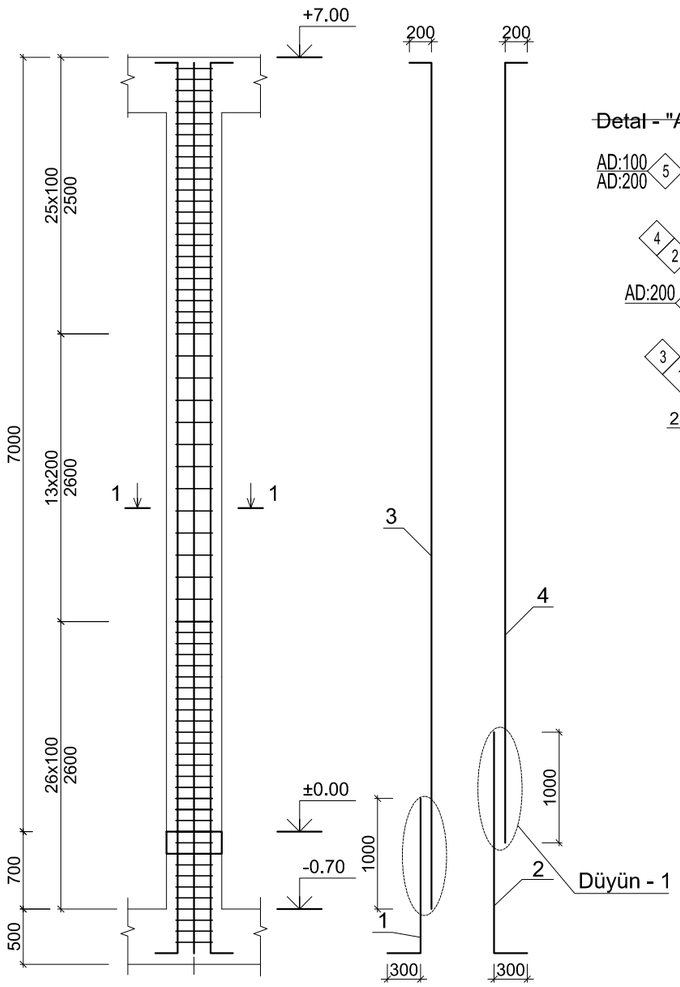


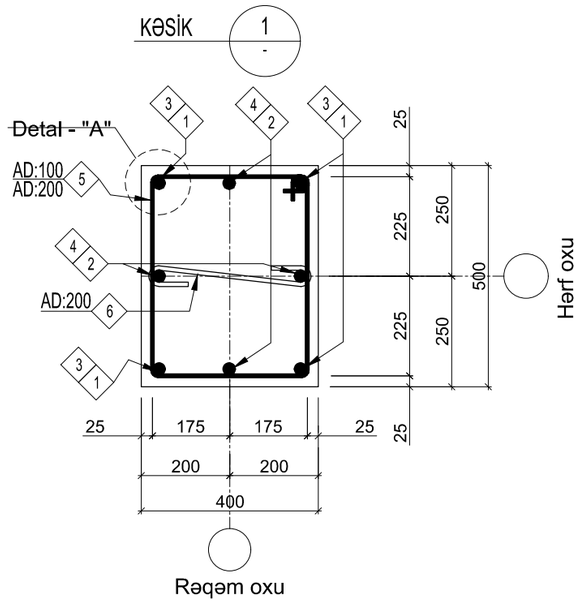


### Materialların təsnifatı. (1 ədəd üçün)

| Format | Zona | Mövqe | İşarəsi | Adı | Miq. | Qeyd |
|---|---|---|---|---|---|---|
| | | | | Monolit d/b sütun "Ms-1" | | |
| | | 1 | DÜİST 52544-2006 | Ø18 A500C , L=1700 mm | 4 | 3.4 / 13.6 |
| | | 2 | ----- // ----- | Ø18 A500C , L=2300 mm | 4 | 4.6 / 18.4 |
| | | 3 | ----- // ----- | Ø18 A500C , L=4150 mm | 4 | 8.3 / 33.2 |
| | | 4 | ----- // ----- | Ø18 A500C , L=3550 mm | 4 | 7.1 / 28.4 |
| | | 5 | DÜİST 5781-82* | Ø8A-I (A240), L=1800 mm | 64 | 0.72 / 46.1 |
| | | 6 | ----- // ----- | Ø8A-I (A240), L=550 mm | 39 | 0.22 / 8.60 |
| | | | | Material: Beton B25 | - | 1.55 $m^3$ |

### Polad sərfi cədvəli, kq. 21 ədəd üçün)

| Elementin markası | Armatur məmulatları | | | | | | | | | Yekun | Beton B25 |
|---|---|---|---|---|---|---|---|---|---|---|---|
| | Armaturun sinfi | | | | | | | | | | |
| | A-I A(240) | | | A500C | | | | | | | |
| | DÜİST 5781-82* | | | DÜİST 52544-2006 | | | | | | | |
| | Ø8 | Ø10 | Cəmi: | Ø12 | Ø14 | Ø16 | Ø18 | Ø20 | Cəmi: | | |
| Monolit d/b sütun "Ms-1" | 1148.7 | | 1148.7 | | | | 1965.6 | | 1965.6 | 3114.3 | 32.55 $m^3$ |

### Detal - "A"

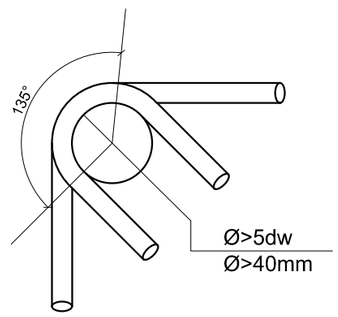


### Armaturların əyilməsi

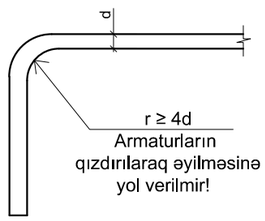


Qeyd:
1. Bu vərəq "DK - 8" vərəqi ilə birgə oxunmalıdır.

### Düyün -1

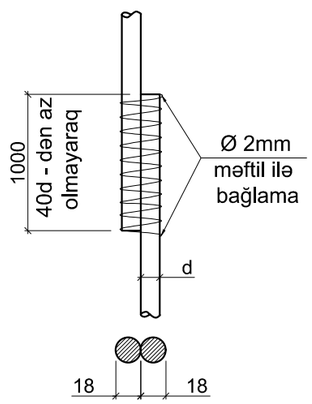


### Detalların cədvəli

| Mövqe | Eskiz |
|---|---|
| 1(2) / 3(4) | 1400 (2000) \| 300 / 3950 (3350) \| 200 |
| 5 | 430; 450; 530; 350 |
| 6 | 100; 350; 100 |

| | | | | | | | |
|---|---|---|---|---|---|---|---|
| | | | | | | Sifarişçi: Cəfərov Mədət İslam oğlu | DK-MK |
| Dəyiş | Sh.sən | Vərəq | Sən.№ | İmza | Tarix | Abşeron rayonu, Qobu qəsəbəsində yerləşən torpaq sahəsində tikintisi nəzərdə tutulan anbar və inzibati binası anbar binası. | |
| L.B.M. | | G. Musayeva | | | | Anbar binası | Mərhələ: İ.L. / Vərəq: 13 / Vərəqlər |
| Konstruktor | | M. Əzizov | | | | | |
| Norm. nəzarət | | S. Şükürova | | | | Monolit d/b sütun "Ms-1"-in konstruksiyası. | "STORM BUİLDİNG" MMC |

Format A3

Razılaşdırılmışdır

İnvent № Əvəzinə

İmza və Tarix

İnvent № İmza

## Monolit d/b sütun "Ms-2"-in konstruksiyası.

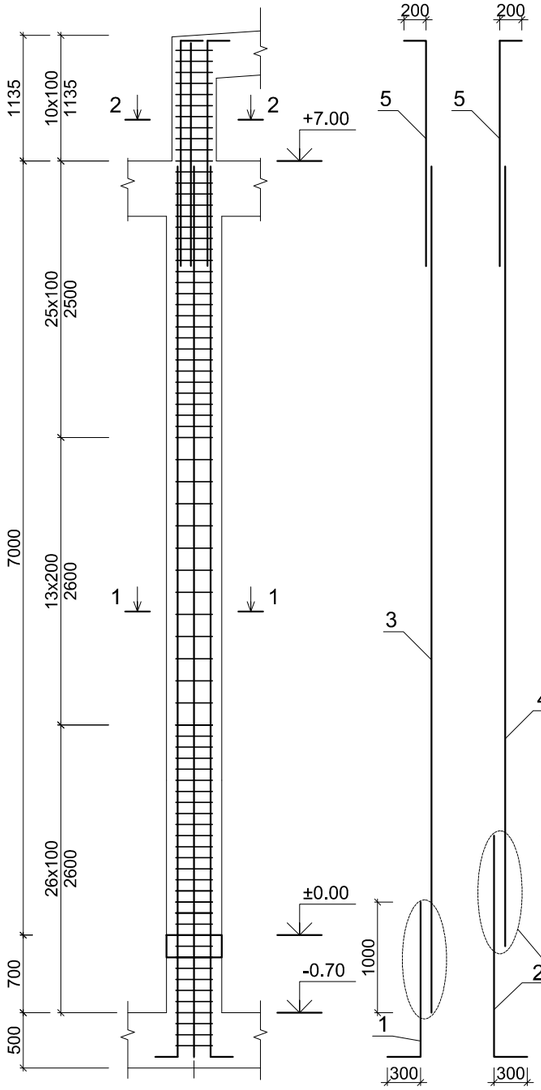


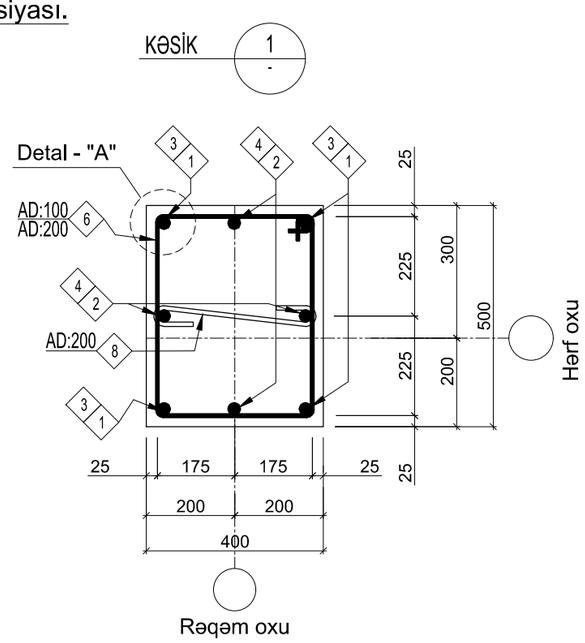


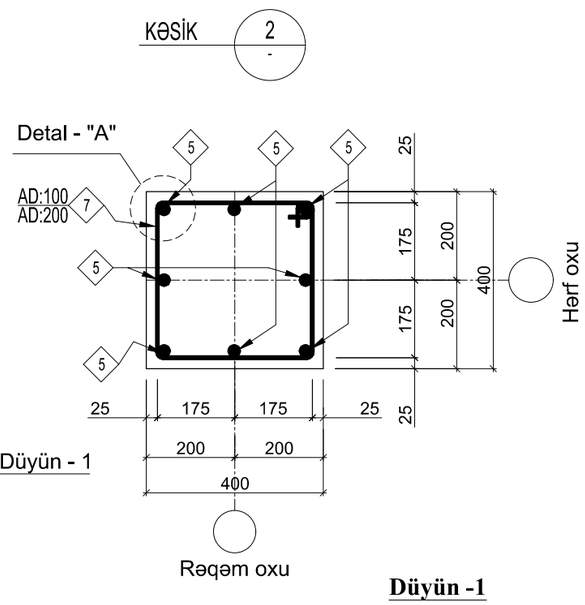


### Materialların təsnifatı. (1 ədəd üçün)

| Format | Zona | Mövqe | İşarəsi | Adı | Miq. | Qeyd |
|---|---|---|---|---|---|---|
| | | | | Monolit d/b sütun "Ms-2" | | |
| | | 1 | DÜİST 52544-2006 | Ø18 A500C , L=1700 mm | 4 | 3.4 / 13.6 |
| | | 2 | ----- // ----- | Ø18 A500C , L=2300 mm | 4 | 4.6 / 18.4 |
| | | 3 | ----- // ----- | Ø18 A500C , L=7650 mm | 4 | 15.3 / 61.2 |
| | | 4 | ----- // ----- | Ø18 A500C , L=7050 mm | 4 | 14.1 / 56.4 |
| | | 5 | ----- // ----- | Ø18 A500C , L=2250 mm | 4 | 4.5 / 18.0 |
| | | 6 | DÜİST 5781-82* | Ø8A-I (A240), L=1800 mm | 64 | 0.72 / 46.1 |
| | | 7 | ----- // ----- | Ø8A-I (A240), L=1600 mm | 10 | 0.64 / 6.4 |
| | | 8 | ----- // ----- | Ø8A-I (A240), L=550 mm | 39 | 0.22 / 8.6 |
| | | | | Material: Beton B25 | - | 1.75 $m^3$ |

### Polad sərfi cədvəli, kq. (4 ədəd üçün)

| Elementin markası | Armatur məmulatları | | | | | | | | | Yekun | Beton B25 |
|---|---|---|---|---|---|---|---|---|---|---|---|
| | Armaturun sinfi | | | | | | | | | | |
| | A-I A(240) | | | A500C | | | | | | | |
| | DÜİST 5781-82* | | | DÜİST 52544-2006 | | | | | | | |
| | Ø8 | Ø10 | Cəmi: | Ø12 | Ø14 | Ø16 | Ø18 | Ø20 | Ø22 | Cəmi: | |
| Monolit d/b sütun "Ms-2" | 244.4 | | 244.4 | | | | 670.4 | | | 670.4 | 914.8 | 7.0 $m^3$ |

### Detal - "A"

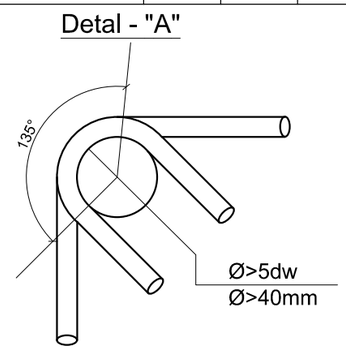


### Armaturların əyilməsi

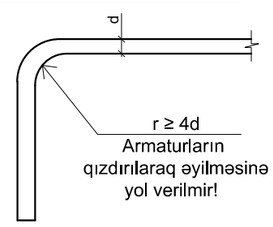


Qeyd:
1. Bu vərəq "DK - 8" vərəqi ilə birgə oxunmalıdır.

### Detalların cədvəli

| Mövqe | Eskiz |
|---|---|
| 1(2) / 5 | 1400 (2000) \| 300 \| 2050 \| 200 |
| 6 / 7 / 8 | 430 / 450 / 530 / 350 ; 430 / 350 / 430 / 350 ; 100 / 350 / 100 |

### Düyün -1

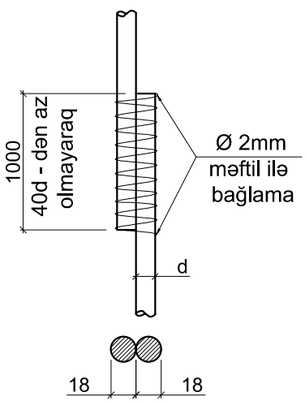


| | | | | | | | |
|---|---|---|---|---|---|---|---|
| | | | | | | Sifarişçi: Cəfərov Mədət İslam oğlu | DK-MK |
| Dəyiş | Sh.sən | Vərəq | Sən.№ | İmza | Tarix | Abşeron rayonu, Qobu qəsəbəsində yerləşən torpaq sahəsində tikintisi nəzərdə tutulan anbar və inzibati binası anbar binası. | |
| L.B.M. | | G. Musayeva | | | | Anbar binası | Mərhələ: İ.L. / Vərəq: 14 / Vərəqlər: |
| Konstruktor | | M. Əzizov | | | | | |
| Norm. nəzarət | | S. Şükürova | | | | Monolit d/b sütun "Ms-2"-nin konstruksiyası. | "STORM BUİLDİNG" MMC |

Razılaşdırılmışdır | İnvent № Əvəzinə | İmza və Tarix | İnvent № İmza

Format A3

## Monolit d/b sütun "Ms-3"-ün konstruksiyası.

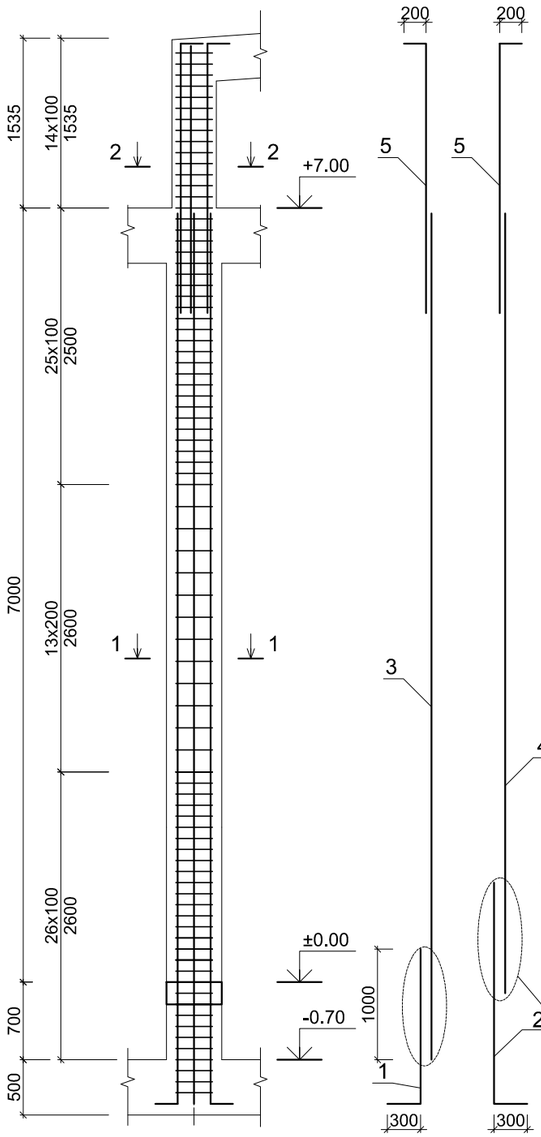


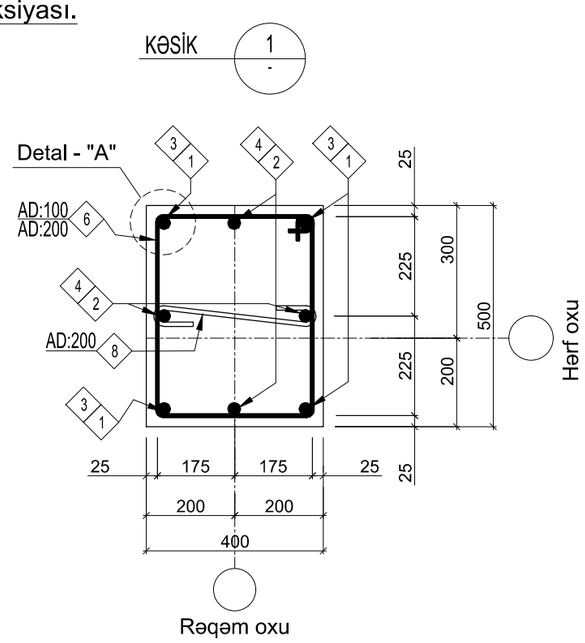


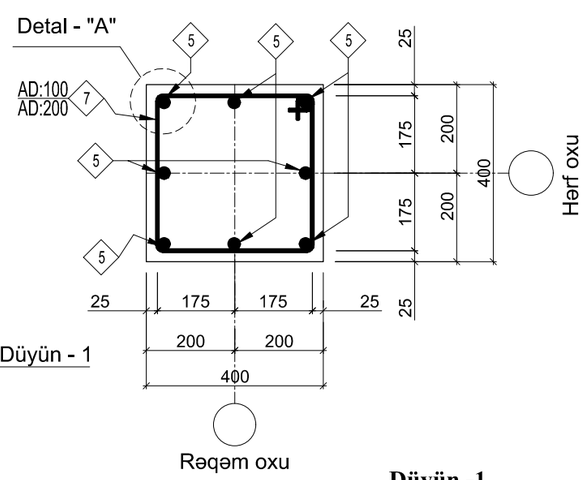


### Materialların təsnifatı. (1 ədəd üçün)

| Format | Zona | Mövqe | İşarəsi | Adı | Miq. | Qeyd |
|---|---|---|---|---|---|---|
| | | | | Monolit d/b sütun "Ms-3" | | |
| | | 1 | DÜİST 52544-2006 | Ø18 A500C , L=1700 mm | 4 | 3.4 / 13.6 |
| | | 2 | ----- // ----- | Ø18 A500C , L=2300 mm | 4 | 4.6 / 18.4 |
| | | 3 | ----- // ----- | Ø18 A500C , L=7650 mm | 4 | 15.3 / 61.2 |
| | | 4 | ----- // ----- | Ø18 A500C , L=7050 mm | 4 | 14.1 / 56.4 |
| | | 5 | ----- // ----- | Ø18 A500C , L=2650 mm | 4 | 5.3 / 21.2 |
| | | 6 | DÜİST 5781-82* | Ø8A-I (A240), L=1800 mm | 64 | 0.72 / 46.1 |
| | | 7 | ----- // ----- | Ø8A-I (A240), L=1600 mm | 14 | 0.64 / 9.0 |
| | | 8 | ----- // ----- | Ø8A-I (A240), L=550 mm | 39 | 0.22 / 8.6 |
| | | | | Material: Beton B25 | - | 1.80 $m^3$ |

### Polad sərfi cədvəli, kq. (4 ədəd üçün)

| Elementin markası | Armatur məmulatları | | | | | | | | | | |
|---|---|---|---|---|---|---|---|---|---|---|---|
| | Armaturun sinfi | | | | | | | | | Yekun | Beton B25 |
| | A-I A(240) | | | A500C | | | | | | | |
| | DÜİST 5781-82* | | | DÜİST 52544-2006 | | | | | | | |
| | Ø8 | Ø10 | Cəmi: | Ø12 | Ø14 | Ø16 | Ø18 | Ø20 | Ø22 | Cəmi: | |
| Monolit d/b sütun "Ms-3" | 254.8 | | 254.8 | | | | 683.2 | | | 683.2 | 938.0 | 7.2 $m^3$ |

### Detal - "A"

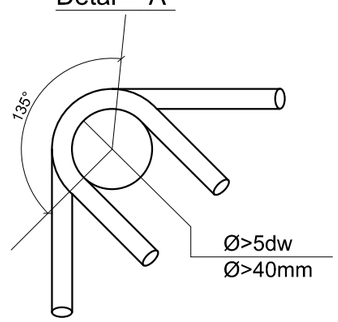


### Armaturların əyilməsi

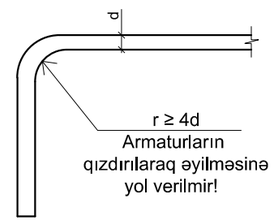


### Detalların cədvəli

| Mövqe | Eskiz |
|---|---|
| 1(2) / 5 | 1400 (2000) \| 300 \| 2450 \| 200 |
| 6 / 7 / 8 | 430 / 450 / 530 / 350 ; 430 / 350 / 350 / 430 ; 100 / 350 / 100 |

### Düyün -1

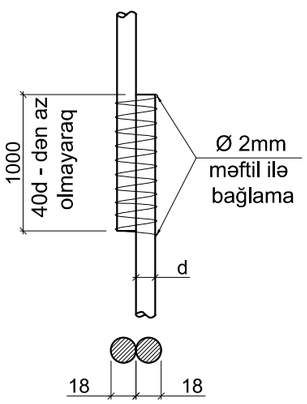


Qeyd:
1. Bu vərəq "DK - 8" vərəqi ilə birgə oxunmalıdır.

| | | | | | | |
|---|---|---|---|---|---|---|
| | | | | | | Sifarişçi: Cəfərov Mədət İslam oğlu |
| Dəyiş | Sh.sən | Vərəq | Sən.№ | İmza | Tarix | Abşeron rayonu, Qobu qəsəbəsində yerləşən torpaq sahəsində tikintisi nəzərdə tutulan anbar və inzibati binası anbar binası. |
| L.B.M. | | G. Musayeva | | | | Anbar binası |
| Konstruktor | | M. Əzizov | | | | |
| Norm. nəzarət | | S. Şükürova | | | | Monolit d/b sütun "Ms-3"-ün konstruksiyası. |

| DK-MK | Mərhələ | Vərəq | Vərəqlər |
|---|---|---|---|
| | İ.L. | 15 | |

"STORM BUİLDİNG" MMC

Razılaşdırılmışdır | İnvent № Əvəzinə | İmza və Tarix | İnvent № İmza

Format A3

## Monolit d/b sütun "Ms-4"-ün konstruksiyası.

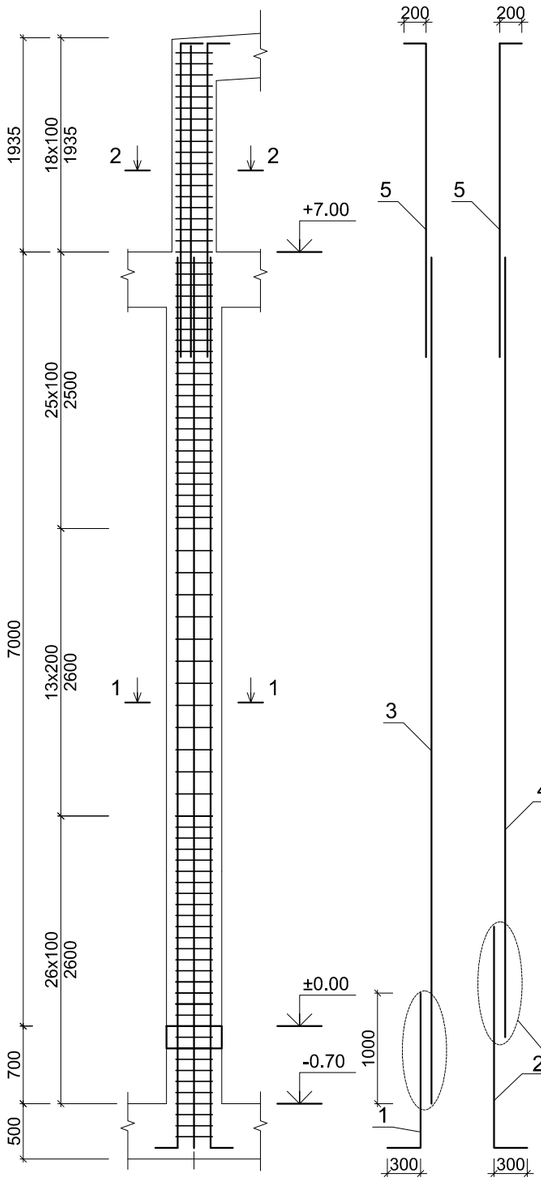


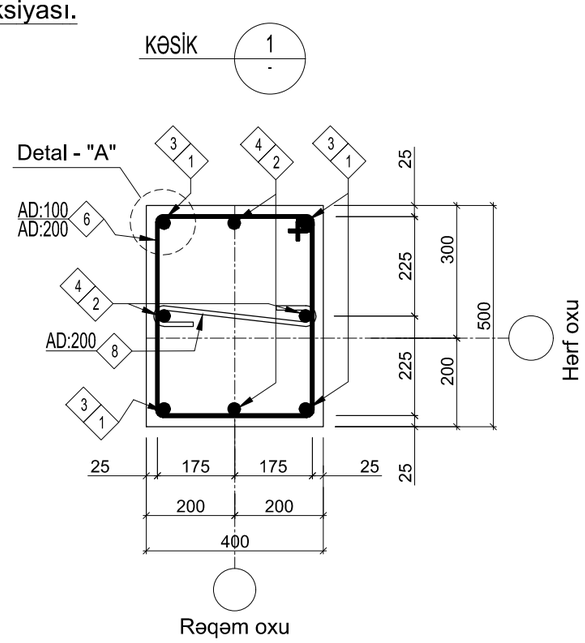


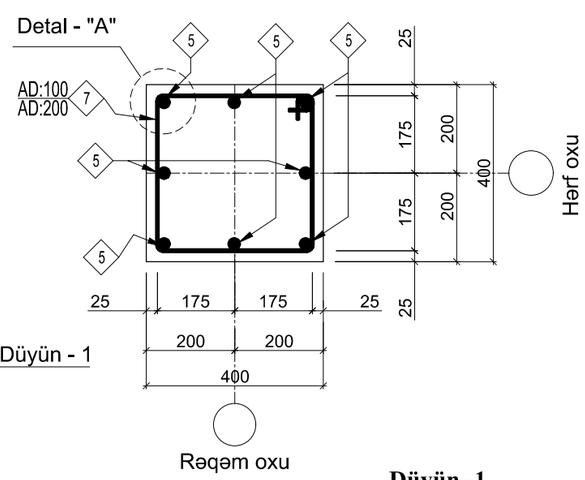


### Detalların cədvəli

| Mövqe | Eskiz |
|---|---|
| 1(2) / 5 | 1400 (2000) \| 300 \| 2850 \| 200 |
| 6 / 7 / 8 | 430, 450, 530, 350 · 430, 350, 430, 350 · 100, 350, 100 |

### Düyün -1

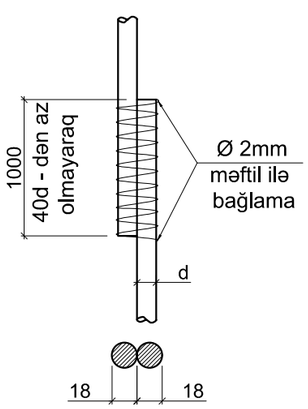


### Materialların təsnifatı. (1 ədəd üçün)

| Format | Zona | Mövqe | İşarəsi | Adı | Miq. | Qeyd |
|---|---|---|---|---|---|---|
| | | | | Monolit d/b sütun "Ms-4" | | |
| | | 1 | DÜİST 52544-2006 | Ø18 A500C , L=1700 mm | 4 | 3.4 / 13.6 |
| | | 2 | ----- // ----- | Ø18 A500C , L=2300 mm | 4 | 4.6 / 18.4 |
| | | 3 | ----- // ----- | Ø18 A500C , L=7650 mm | 4 | 15.3 / 61.2 |
| | | 4 | ----- // ----- | Ø18 A500C , L=7050 mm | 4 | 14.1 / 56.4 |
| | | 5 | ----- // ----- | Ø18 A500C , L=3050 mm | 4 | 6.1 / 24.4 |
| | | 6 | DÜİST 5781-82* | Ø8A-I (A240), L=1800 mm | 64 | 0.72 / 46.1 |
| | | 7 | ----- // ----- | Ø8A-I (A240), L=1600 mm | 18 | 0.64 / 11.6 |
| | | 8 | ----- // ----- | Ø8A-I (A240), L=550 mm | 39 | 0.22 / 8.6 |
| | | | | Material: Beton B25 | - | 1.86 $m^3$ |

### Polad sərfi cədvəli, kq. (2 ədəd üçün)

| Elementin markası | Armatur məmulatları | | | | | | | | | | | |
|---|---|---|---|---|---|---|---|---|---|---|---|---|
| | Armaturun sinfi | | | | | | | | | | Yekun | Beton B25 |
| | A-I A(240) | | | A500C | | | | | | | | |
| | DÜİST 5781-82* | | | DÜİST 52544-2006 | | | | | | | | |
| | Ø8 | Ø10 | Cəmi: | Ø12 | Ø14 | Ø16 | Ø18 | Ø20 | Ø22 | Cəmi: | | |
| Monolit d/b sütun "Ms-4" | 132.6 | | 132.6 | | | | 348.0 | | | 348.0 | 480.6 | 3.72 $m^3$ |

### Detal - "A"

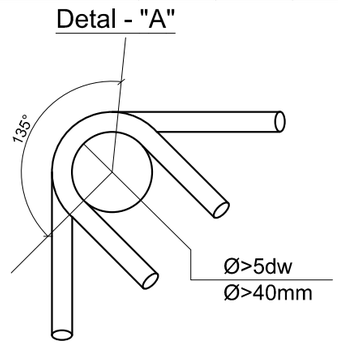


### Armaturların əyilməsi

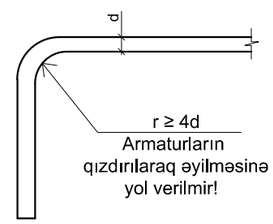


Qeyd:
1. Bu vərəq "DK - 8" vərəqi ilə birgə oxunmalıdır.

| | | | | | | |
|---|---|---|---|---|---|---|
| | | | | | | Sifarişçi: Cəfərov Mədət İslam oğlu |
| Dəyiş | Sh.sən | Vərəq | Sən.№ | İmza | Tarix | Abşeron rayonu, Qobu qəsəbəsində yerləşən torpaq sahəsində tikintisi nəzərdə tutulan anbar və inzibati binası anbar binası. |
| L.B.M. | | G. Musayeva | | | | Anbar binası |
| Konstruktor | | M. Əzizov | | | | |
| Norm. nəzarət | | S. Şükürova | | | | Monolit d/b sütun "Ms-4"-ün konstruksiyası. |

| DK-MK | | | |
|---|---|---|---|
| | Mərhələ | Vərəq | Vərəqlər |
| | İ.L. | 16 | |
| "STORM BUİLDİNG" MMC | | | |

Razılaşdırılmışdır

İnvent № Əvəzinə

İmza və Tarix

İnvent № İmza

Format A3

+3.70 səviyyəsində monolit d/b kəmərlərin yerləşmə planı.

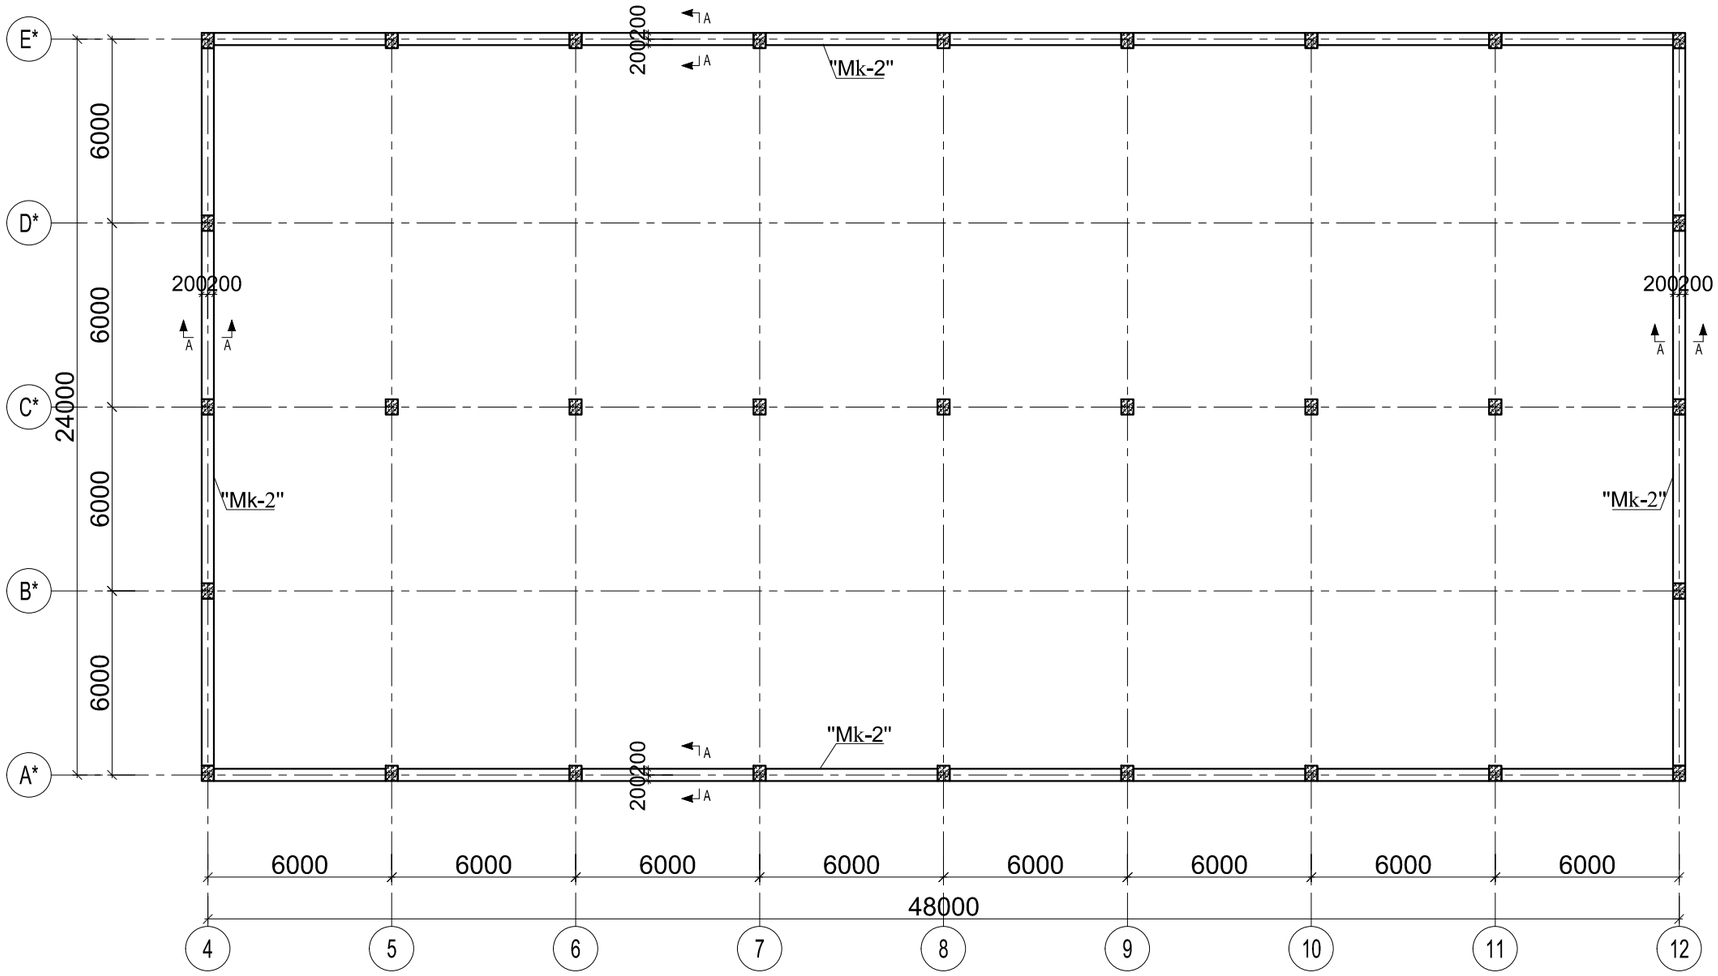


**Kəsik A-A**

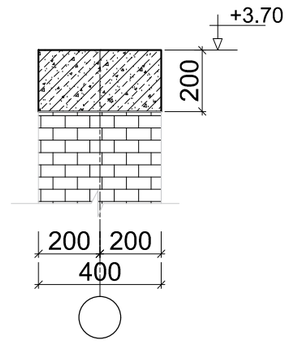


Monolit d/b elementlərin təsnifatı

| Format | Zona | Mövqe | İşarə | Adı | Miqdarı | Qeyd |
|---|---|---|---|---|---|---|
| Monolit d/b kəmər | | | | | | |
| | | | | Monolit d/b kəmər Mk-2 | | 144.00 Pm |

| | | | | | | |
|---|---|---|---|---|---|---|
| | | | | | | Sifarişçi: Cəfərov Mədət İslam oğlu |
| Dəyiş | Sh.sən | Vərəq | Sən.№ | İmza | Tarix | Abşeron rayonu, Qobu qəsəbəsində yerləşən torpaq sahəsində tikintisi nəzərdə tutulan anbar və inzibati binası anbar binası. |
| L.B.M. | | G. Musayeva | | | | Anbar binası |
| Konstruktor | | M. Əzizov | | | | |
| Norm. nəzarət | | S. Şükürova | | | | +3.70 səviyyəsində monolit d/b kəmərlərin yerləşmə planı. |

| DK-MK | | | |
|---|---|---|---|
| | Mərhələ | Vərəq | Vərəqlər |
| | İ.L. | 17 | |
| "STORM BUİLDİNG" MMC | | | |

Razılaşdırılmışdır

İnvent № Əvəzinə

İmza və Tarix

İnvent № İmza

Format A3

+7.00 səviyyəsində monolit d/b rigellərin yerləşmə planı.

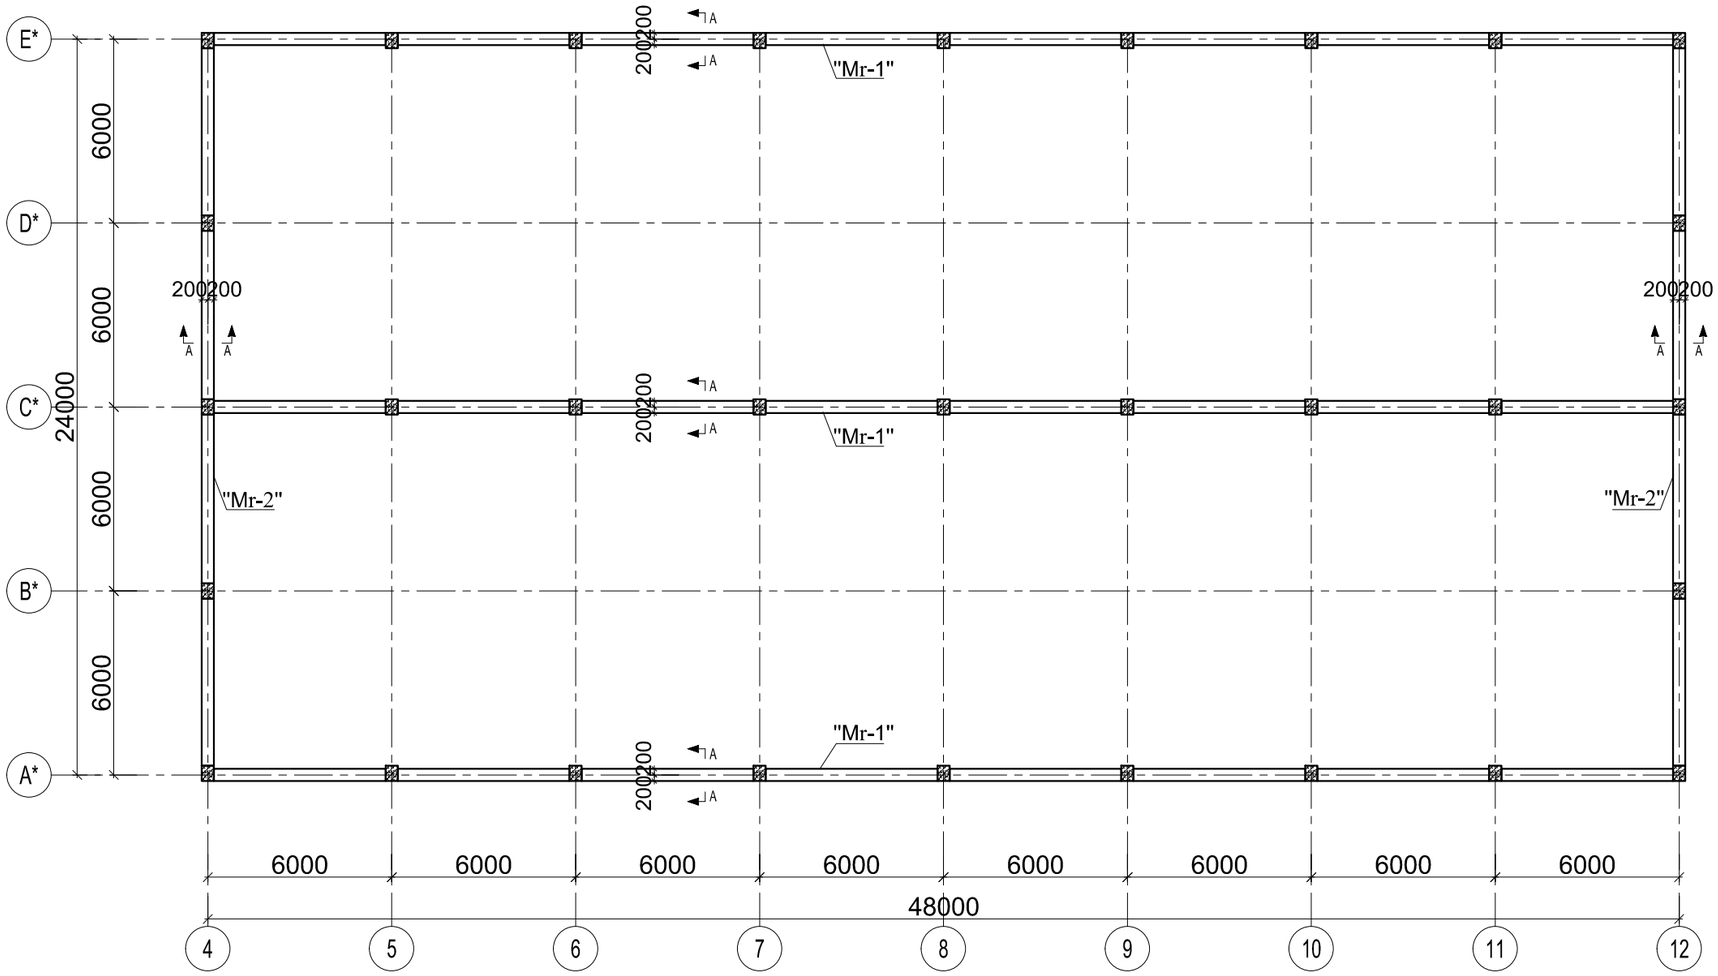


**Kəsik A-A**

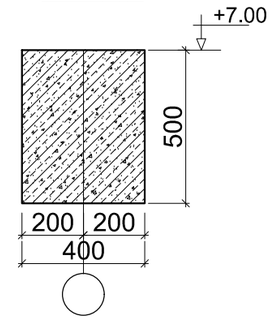


Monolit d/b elementlərin təsnifatı

| Format | Zona | Mövqe | İşarə | Adı | Miqdarı | Qeyd |
|---|---|---|---|---|---|---|
| Monolit d/b rigellər | | | | | | |
| | | | | Monolit d/b rigel Mr-1 | 3 | |
| | | | | Monolit d/b rigel Mr-2 | 2 | |

| Dəyiş | Sh.sən | Vərəq | Sən.№ | İmza | Tarix |
|---|---|---|---|---|---|
| L.B.M. | | G. Musayeva | | | |
| Konstruktor | | M. Əzizov | | | |
| Norm. nəzarət | | S. Şükürova | | | |

Sifarişçi: Cəfərov Mədət İslam oğlu — DK-MK

Abşeron rayonu, Qobu qəsəbəsində yerləşən torpaq sahəsində tikintisi nəzərdə tutulan anbar və inzibati binası anbar binası.

Anbar binası

| Mərhələ | Vərəq | Vərəqlər |
|---|---|---|
| İ.L. | 18 | |

+7.00 səviyyəsində monolit d/b rigellərin yerləşmə planı.

"STORM BUİLDİNG" MMC

Format A3

Razılaşdırılmışdır

İnvent № Əvəzinə

İmza və Tarix

İnvent № İmza

+8.00 səviyyəsində monolit d/b rigellərin yerləşmə planı.

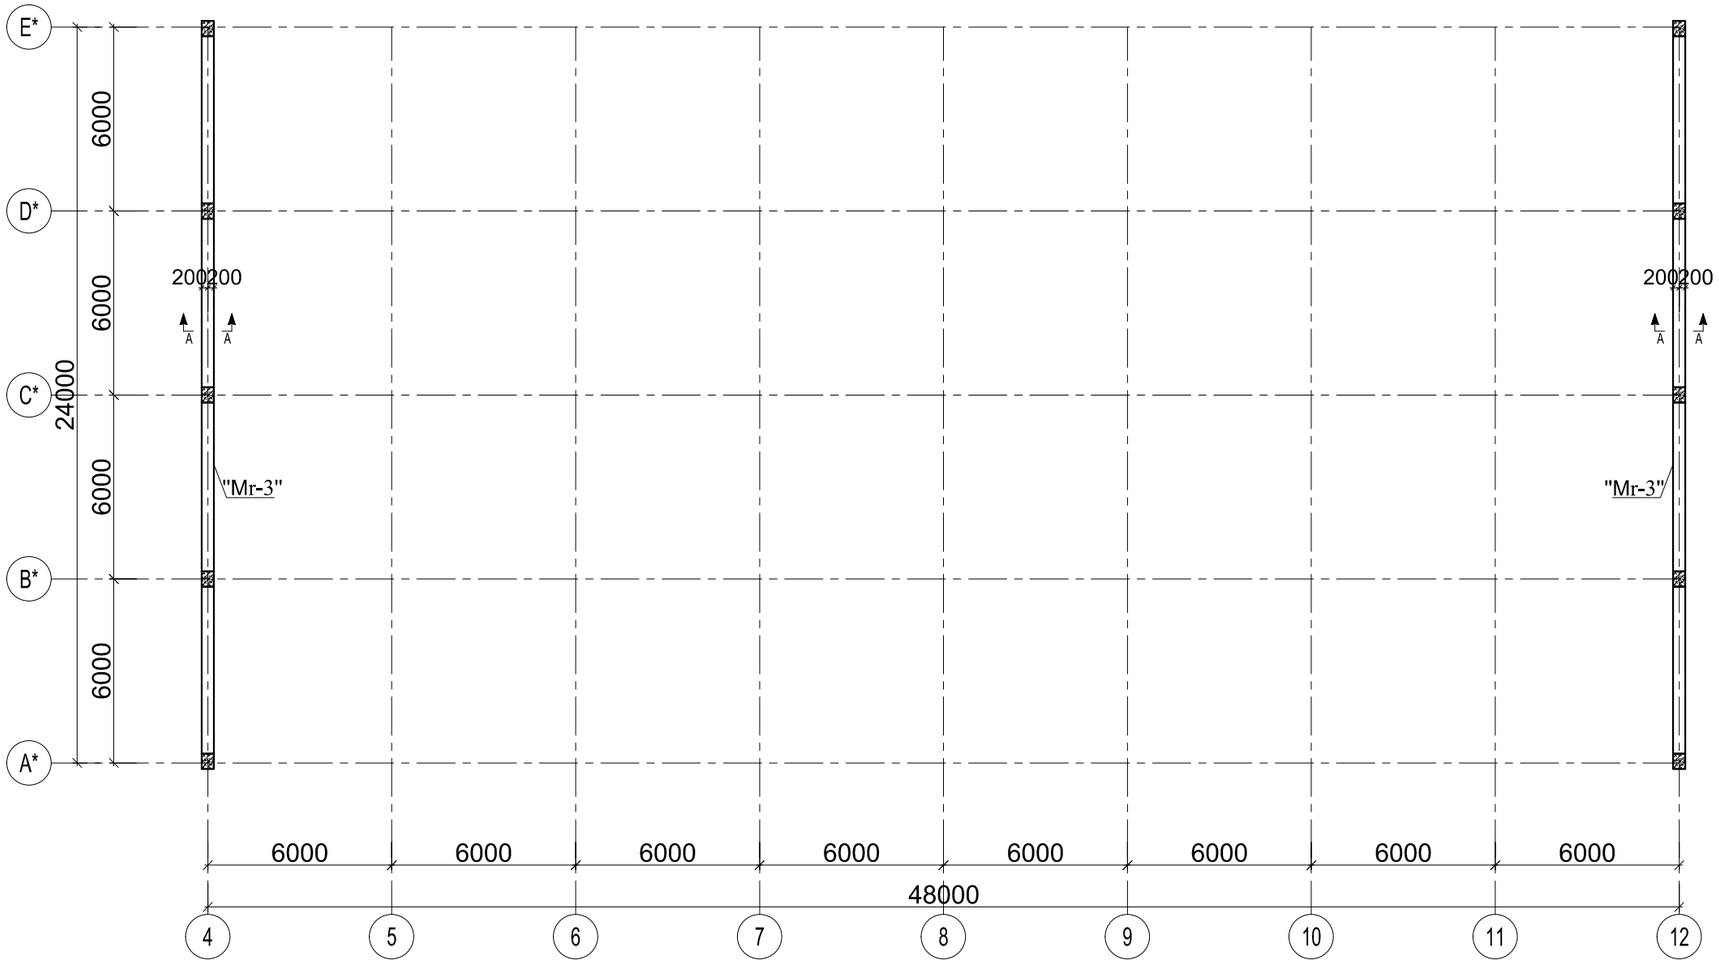


**Kəsik A-A**

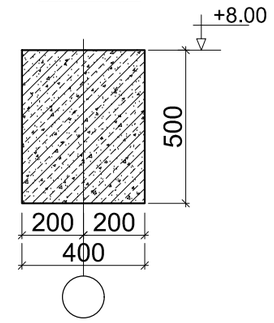


Monolit d/b elementlərin təsnifatı

| Format | Zona | Mövqe | İşarə | Adı | Miqdarı | Qeyd |
|---|---|---|---|---|---|---|
| Monolit d/b rigellər | | | | | | |
| | | | | Monolit d/b rigel Mr-3 | 2 | |

| | | | | | | |
|---|---|---|---|---|---|---|
| | | | | | | Sifarişçi: Cəfərov Mədət İslam oğlu |
| Dəyiş | Sh.sən | Vərəq | Sən.№ | İmza | Tarix | Abşeron rayonu, Qobu qəsəbəsində yerləşən torpaq sahəsində tikintisi nəzərdə tutulan anbar və inzibati binası anbar binası. |
| L.B.M. | | G. Musayeva | | | | Anbar binası |
| Konstruktor | | M. Əzizov | | | | |
| Norm. nəzarət | | S. Şükürova | | | | +8.00 səviyyəsində monolit d/b rigellərin yerləşmə planı. |

| DK-MK | | | |
|---|---|---|---|
| | Mərhələ | Vərəq | Vərəqlər |
| | İ.L. | 19 | |
| "STORM BUİLDİNG" MMC | | | |

Razılaşdırılmışdır

İnvent № Əvəzinə

İmza və Tarix

İnvent № İmza

Format A3

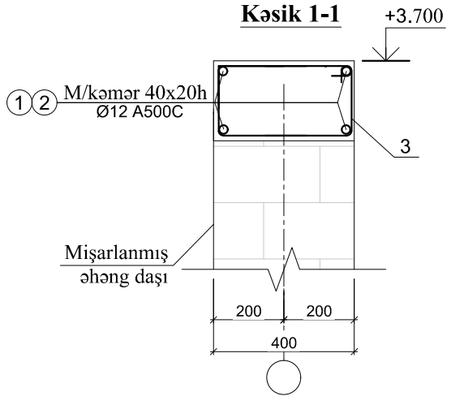


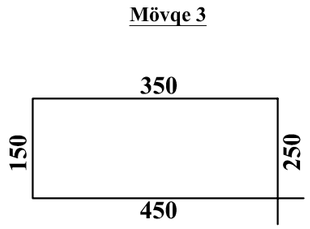


Materialların təsnifatı

| Format | Zona | Mövqe | İşarəsi | Adı | Miq. | Qeyd |
|---|---|---|---|---|---|---|
| | | | | Monolit d/b kəmər Mk-2 | 144.0 p.m | |
| | | 1 | ГОСТ 52544-2006 | Ø12 A500C , $L_{üm}$=303.0 p.m | - | - / 269.10 |
| | | 2 | ГОСТ 52544-2006 | Ø12 A500C , $L_{üm}$=303.0 p.m | - | - / 269.10 |
| | | | | Xamutlar | | |
| | | 3 | DÜİST 5781-82* | Ø8 A-I (A240), L =1200 mm | 720 | 0,48 / 345.60 |
| | | | | Material: Beton B25 | - | 11.52 $m^3$ |

**Polad sərfi cədvəli, kq.**

| Elementin markası | Armatur məmulatları | | | | | | | | | |
|---|---|---|---|---|---|---|---|---|---|---|
| | Armaturun sinfi | | | | | | | | | Yekun |
| | A-I A(240) | | | A500C | | | | | | |
| | DÜİST 5781-82* | | | DÜİST 52544-2006 | | | | | | |
| | Ø8 | Ø10 | Cəmi: | | Ø12 | Ø14 | Ø18 | Ø20 | Cəmi: | |
| Monolit d/b kəmər | 345.6 | 0 | 345.6 | 0 | 538.2 | 0 | 0 | 0 | 538.2 | 883.80 |

Razılaşdırılmışdır

İnvent № Əvəzinə

İmza və Tarix

İnvent № İmza

| Dəyiş | Sh.sən | Vərəq | Sən.№ | İmza | Tarix |
|---|---|---|---|---|---|
| L.B.M. | | G. Musayeva | | | |
| Konstruktor | | M. Əzizov | | | |
| Norm. nəzarət | | S. Şükürova | | | |

Sifarişçi: Cəfərov Mədət İslam oğlu — DK-MK

Abşeron rayonu, Qobu qəsəbəsində yerləşən torpaq sahəsində tikintisi nəzərdə tutulan anbar və inzibati binası anbar binası.

| Anbar binası | Mərhələ | Vərəq | Vərəqlər |
|---|---|---|---|
| | İ.L. | 20 | |
| Monolit d/b kəmər Mk-2 | "STORM BUİLDİNG" MMC | | |

Format A3

MONOLİT D/B RİGEL "MR-1"

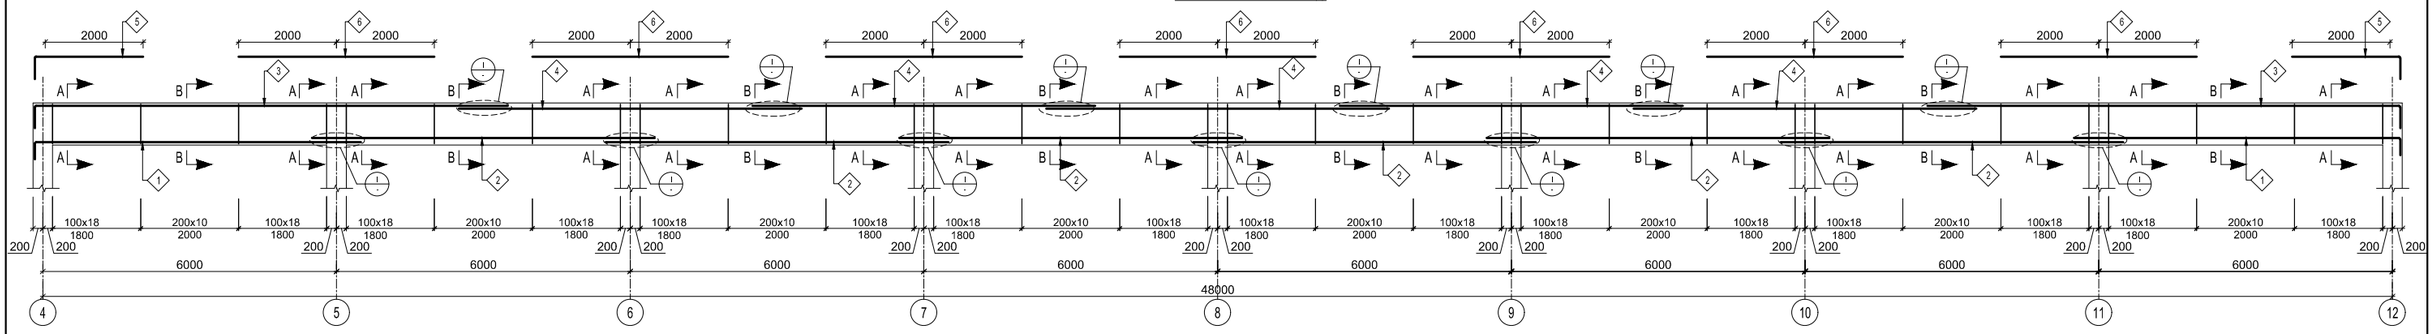


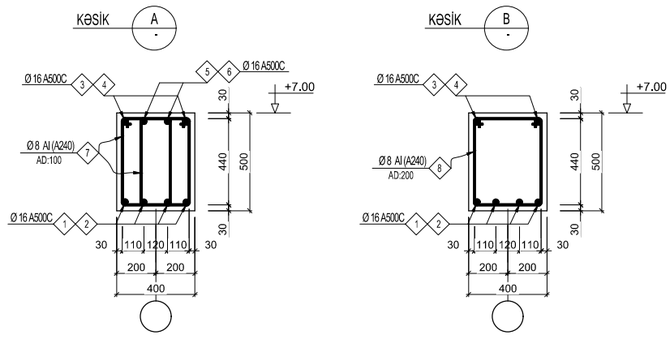


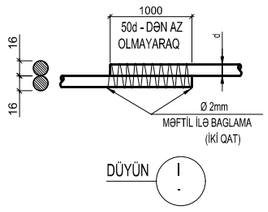


## DETALLAR CƏDVƏLİ

| MÖVQE | ESKİZ |
|---|---|
| 1 / 3 | 400 — 6710; 400 — 9710 |
| 5 | 400 — 2210 |
| 7 / 8 | 320, 520, 440, 240; 430, 440, 520, 350 |

## MATERİALLARIN TƏSNİFATI.

| FORMAT | ZONA | MÖVQE | İŞARƏ | ADI | MİQDARI | KÜTLƏSİ ( kq ) |
|---|---|---|---|---|---|---|
| | | | | MONOLİT RİGEL "MR -1" | 3 | |
| | | 1 | DÜİST 52544-2006 | Ø16 A500C, L=7110 | 8 | 97.40 |
| | | 2 | ---- // ---- | Ø16 A500C, L=7000 | 24 | 265.20 |
| | | 3 | ---- // ---- | Ø16 A500C, L=10110 | 4 | 63.90 |
| | | 4 | ---- // ---- | Ø16 A500C, L=7000 | 10 | 110.50 |
| | | 5 | ---- // ---- | Ø16 A500C, L=2610 | 4 | 16.50 |
| | | 6 | ---- // ---- | Ø16 A500C, L=4000 | 14 | 88.40 |
| | | 7 | DÜİST 5781-82* | Ø8A-I (A240), L=1520 | 576 | 345.90 |
| | | 8 | ---- // ---- | Ø8A-I (A240), L=1740 | 80 | 55.00 |
| | | | | MATERİAL: BETON B25 | - | 8.96 m³ |

## POLAD SƏRFİ CƏDVƏLİ , Kq.

| ELEMENTİN MARKASI | ARMATUR MƏMULATLARI | | | | | | | | ÜMUMİ SƏRF (kq) | BETON B25 |
|---|---|---|---|---|---|---|---|---|---|---|
| | ARMATURUN SİNFİ | | | | | | | | | |
| | A-I (A240) | | | A500C | | | | | | |
| | DÜİST 5781-82* | | | DÜİST 52544-2006 | | | | | | |
| | Ø6 | Ø8 | CƏMİ: | Ø16 | Ø18 | Ø20 | Ø22 | CƏMİ: | | |
| RİGEL "MR -1" (3 ƏDƏD ÜÇÜN) | - | 1202.70 | 1202.70 | 1925.70 | - | - | - | 1925.70 | 3128.40 | 26.88 m³ |

| | | | | | | |
|---|---|---|---|---|---|---|
| | | | | | | Sifarişçi: Cəfərov Mədət İslam oğlu — DK-MK |
| Dəyiş | Sh.sən | Vərəq | Sən.№ | İmza | Tarix | Abşeron rayonu, Qobu qəsəbəsində yerləşən torpaq sahəsində tikintisi nəzərdə tutulan anbar və inzibati binası anbar binası. |
| L.B.M. | | G. Musayeva | | | | Anbar binası — Mərhələ: İ.L. — Vərəq: 21 — Vərəqlər: |
| Konstruktor | | M. Əzizov | | | | MONOLİT D/B RİGEL "MR-1" KONSTRUKSİYASI — "STORM BUİLDİNG" MMC |
| Norm. nəzarət | | S. Şükürova | | | | |

Razılaşdırılmışdır

İnvent № Əvəzinə

İmza və Tarix

İnvent № İmza

Format A3

MONOLİT D/B RİGEL "MR-2"

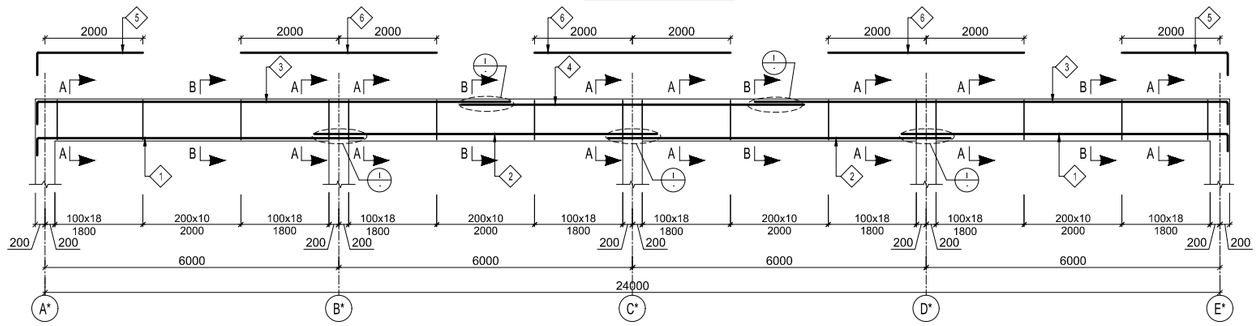


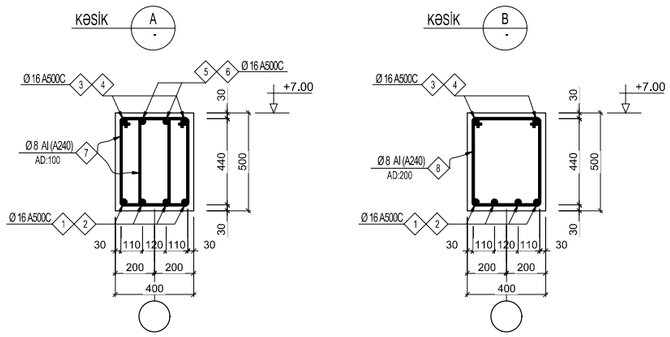





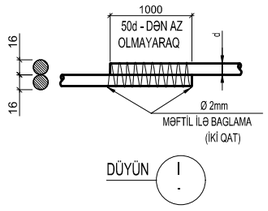


## MATERİALLARIN TƏSNİFATI.

| FORMAT | ZONA | MÖVQE | İŞARƏ | ADI | MİQDARI | KÜTLƏSİ ( kq ) |
|---|---|---|---|---|---|---|
| | | | | MONOLİT RİGEL "MR -2" | 2 | |
| | | 1 | DÜİST 52544-2006 | Ø16 A500C, L=7110 | 8 | 97.40 |
| | | 2 | ---- // ---- | Ø16 A500C, L=7000 | 8 | 88.40 |
| | | 3 | ---- // ---- | Ø16 A500C, L=10110 | 4 | 63.90 |
| | | 4 | ---- // ---- | Ø16 A500C, L=7000 | 2 | 22.10 |
| | | 5 | ---- // ---- | Ø16 A500C, L=2610 | 4 | 16.50 |
| | | 6 | ---- // ---- | Ø16 A500C, L=4000 | 6 | 37.90 |
| | | 7 | DÜİST 5781-82* | Ø8A-I (A240), L=1520 | 288 | 173.00 |
| | | 8 | ---- // ---- | Ø8A-I (A240), L=1740 | 40 | 27.50 |
| | | | | MATERİAL: BETON B25 | - | 4.40 m³ |

## DETALLAR CƏDVƏLİ

| MÖVQE | ESKİZ | |
|---|---|---|
| 1 / 3 | 400 6710 | 400 9710 |
| 5 | 400 2210 | |
| 7 / 8 | 320, 520, 440, 240 | 430, 440, 520, 350 |

## POLAD SƏRFİ CƏDVƏLİ , Kq.

| ELEMENTİN MARKASI | ARMATUR MƏMULATLARI | | | | | | | | ÜMUMİ SƏRF (kq) | BETON B25 |
|---|---|---|---|---|---|---|---|---|---|---|
| | ARMATURUN SİNFİ | | | | | | | | | |
| | A-I (A240) | | | A500C | | | | | | |
| | DÜİST 5781-82* | | | DÜİST 52544-2006 | | | | | | |
| | Ø6 | Ø8 | CƏMİ: | Ø16 | Ø18 | Ø20 | Ø22 | CƏMİ: | | |
| RİGEL "MR -2" (2 ƏDƏD ÜÇÜN) | - | 401.00 | 401.00 | 652.40 | - | - | - | 652.40 | 1053.40 | 8.80 m³ |

| | | | | | | |
|---|---|---|---|---|---|---|
| | | | | | | Sifarişçi: Cəfərov Mədət İslam oğlu — DK-MK |
| Dəyiş | Sh.sən | Vərəq | Sən.№ | İmza | Tarix | Abşeron rayonu, Qobu qəsəbəsində yerləşən torpaq sahəsində tikintisi nəzərdə tutulan anbar və inzibati binası anbar binası. |
| L.B.M. | | G. Musayeva | | | | Anbar binası — Mərhələ: İ.L. — Vərəq: 22 — Vərəqlər: |
| Konstruktor | | M. Əzizov | | | | MONOLİT D/B RİGEL "MR-2" KONSTRUKSİYASI — "STORM BUİLDİNG" MMC |
| Norm. nəzarət | | S. Şükürova | | | | |

Razılaşdırılmışdır

İnvent № Əvəzinə

İmza və Tarix

İnvent № İmza

Format A3

MONOLİT D/B RİGEL "MR-3"

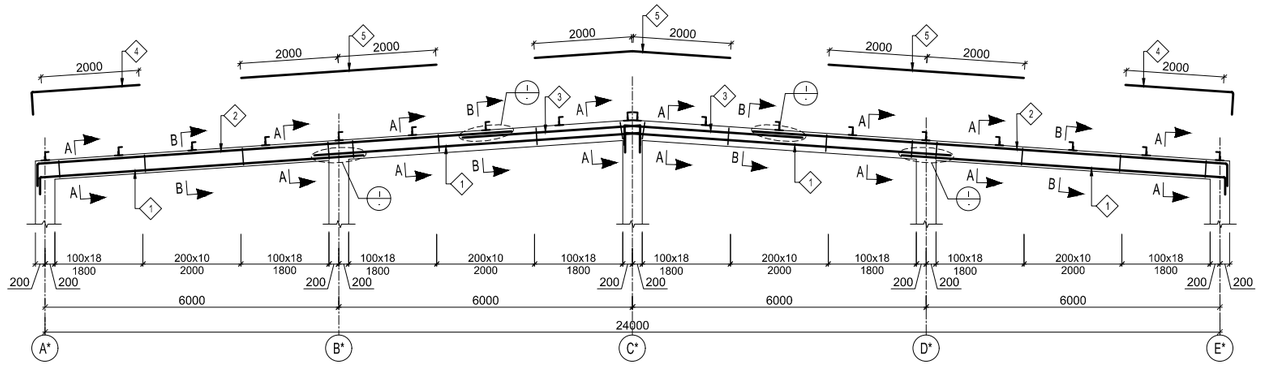


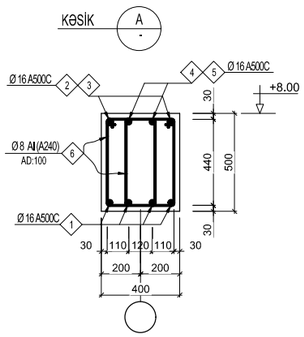


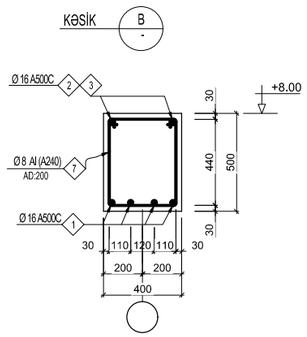


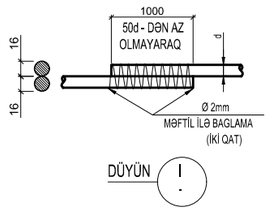


DETALLAR CƏDVƏLİ

| MÖVQE | ESKİZ |
|---|---|
| 1 | 6700 / 400 |
| 2(3) / 4 | 9700(3650) / 400 ; 2210 / 400 |
| 6 / 7 | 320, 420, 340, 240 ; 430, 440, 520, 350 |

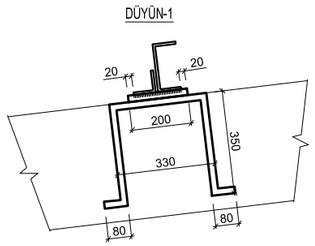


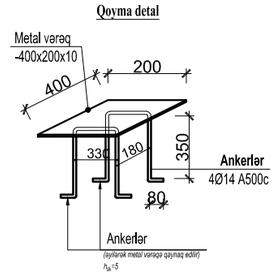


MATERİALLARIN TƏSNİFATI.

| FORMAT | ZONA | MÖVQE | İŞARƏ | ADI | MİQDARI | KÜTLƏSİ ( kq ) |
|---|---|---|---|---|---|---|
| | | | | MONOLİT RİGEL "MR -3" | 2 | |
| | | 1 | DÜİST 52544-2006 | Ø16 A500C, L=7110 | 16 | 97.40 |
| | | 2 | ---- // ---- | Ø16 A500C, L=10110 | 4 | 63.90 |
| | | 3 | ---- // ---- | Ø16 A500C, L=4050 | 4 | 25.60 |
| | | 4 | ---- // ---- | Ø16 A500C, L=2610 | 4 | 16.50 |
| | | 5 | ---- // ---- | Ø16 A500C, L=4000 | 6 | 37.90 |
| | | 6 | DÜİST 5781-82* | Ø8A-I (A240), L=1520 | 288 | 173.00 |
| | | 7 | ---- // ---- | Ø8A-I (A240), L=1740 | 40 | 27.50 |
| | | | | MATERİAL: BETON B25 | - | 4.40 m³ |

POLAD SƏRFİ CƏDVƏLİ , Kq.

| ELEMENTİN MARKASI | ARMATUR MƏMULATLARI | | | | | | | | ÜMUMİ SƏRF (kq) | BETON B25 |
|---|---|---|---|---|---|---|---|---|---|---|
| | ARMATURUN SİNFİ | | | | | | | | | |
| | A-I (A240) | | | A500C | | | | | | |
| | DÜİST 5781-82* | | | DÜİST 52544-2006 | | | | | | |
| | Ø6 | Ø8 | CƏMİ: | Ø16 | Ø18 | Ø20 | Ø22 | CƏMİ: | | |
| RİGEL "MR -3" (2 ƏDƏD ÜÇÜN) | - | 401.00 | 401.00 | 482.60 | - | - | - | 482.60 | 883.60 | 8.80 m³ |

| FORMAT | ZONA | MÖVQE | İŞARƏ | ADI | MİQDARI | KÜTLƏSİ ( kq ) |
|---|---|---|---|---|---|---|
| | | | | Praqon detal birləşməsi | 36 | |
| | | 1 | DÜİST 52544-2006 | Ø14 A500C, L=1190 | 72 | 103.50 |
| | | 2 | | - 400 x 200 x 10 | 36 | 226.10 |

| Dəyiş | Sh.sən | Vərəq | Sən.№ | İmza | Tarix |
|---|---|---|---|---|---|
| L.B.M. | | G. Musayeva | | | |
| Konstruktor | | M. Əzizov | | | |
| Norm. nəzarət | | S. Şükürova | | | |

Sifarişçi: Cəfərov Mədət İslam oğlu — DK-MK

Abşeron rayonu, Qobu qəsəbəsində yerləşən torpaq sahəsində tikintisi nəzərdə tutulan anbar və inzibati binası anbar binası.

| Anbar binası | Mərhələ | Vərəq | Vərəqlər |
|---|---|---|---|
| | İ.L. | 23 | |
| MONOLİT D/B RİGEL "MR-3" KONSTRUKSİYASI | "STORM BUİLDİNG" MMC | | |

Razılaşdırılmışdır

İnvent № Əvəzinə

İmza və Tarix

İnvent № İmza

Format A3

Fermaların yerləşməsi

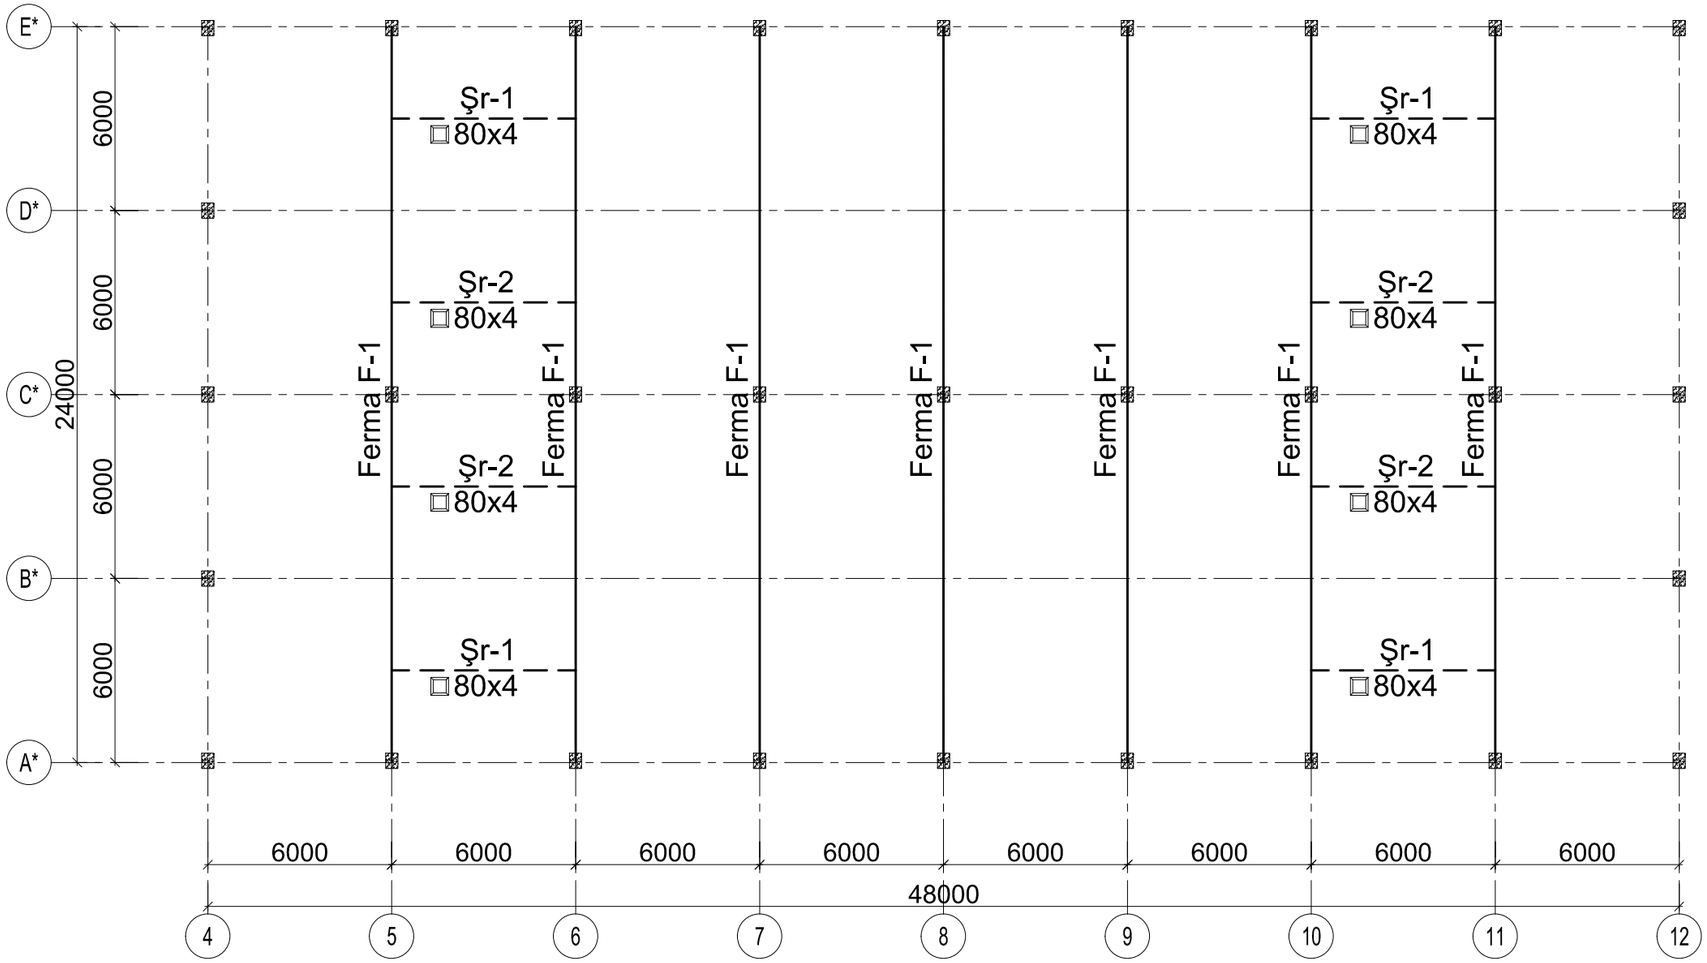


| | | | | | | | |
|---|---|---|---|---|---|---|---|
| | | | | | | Sifarişçi: Cəfərov Mədət İslam oğlu | DK-MK |
| | | | | | | Abşeron rayonu, Qobu qəsəbəsində yerləşən torpaq sahəsində tikintisi nəzərdə tutulan anbar və inzibati binası anbar binası. | |
| Dəyiş | Sh.sən | Vərəq | Sən.№ | İmza | Tarix | | |
| L.B.M. | | G. Musayeva | | | | Anbar binası | Mərhələ / Vərəq / Vərəqlər: İ.L. / 24 / |
| Konstruktor | | M. Əzizov | | | | | |
| Norm. nəzarət | | S. Şükürova | | | | Fermaların yerləşməsi | "STORM BUİLDİNG" MMC |

Razılaşdırılmışdır

İnvent № | İmza

İmza və Tarix | İnvent № Əvəzinə

Format A3

Ferma "F-1"-in həndəsi ölçüləri

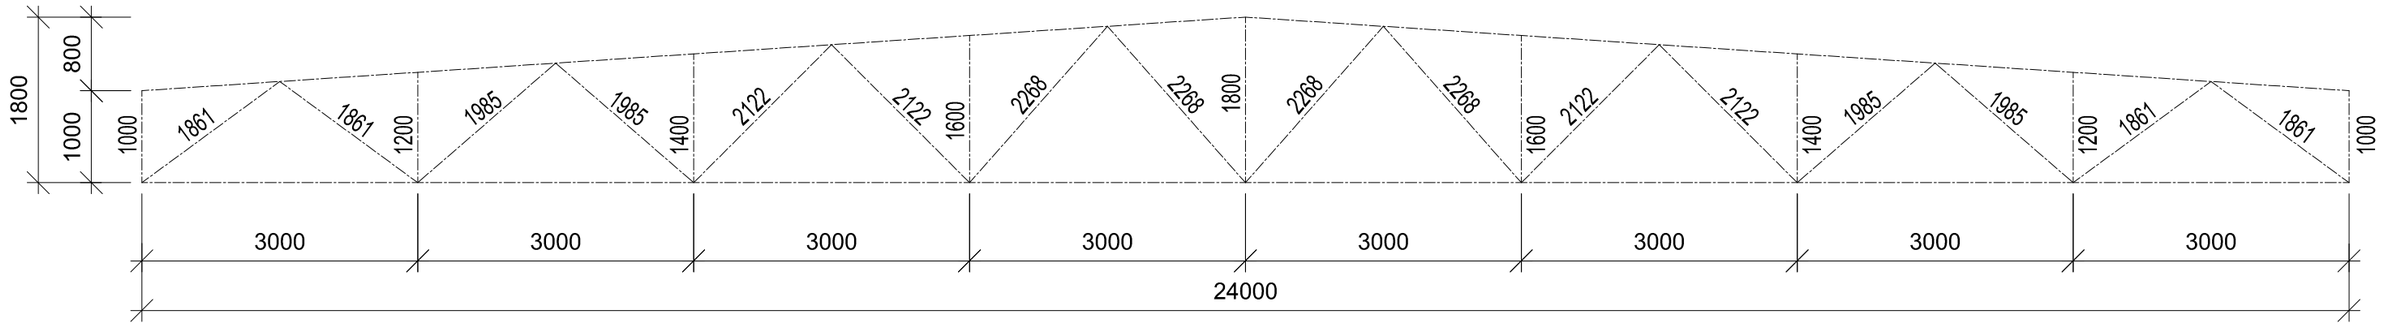


Ferma "F-1"

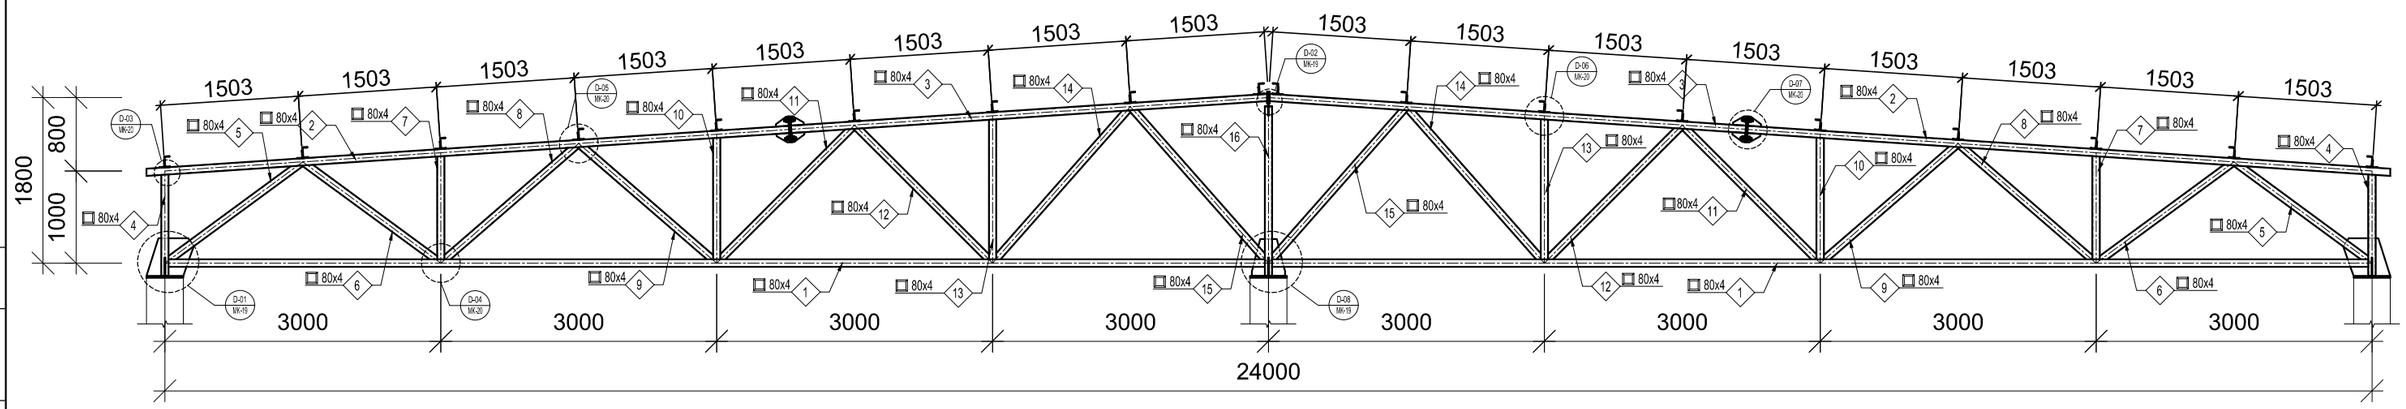


Razılaşdırılmışdır

| İnvent № | İmza | İmza və Tarix | İnvent № Əvəzinə |
|---|---|---|---|
| | | | |

| Dəyiş | Sh.sən | Vərəq | Sən.№ | İmza | Tarix |
|---|---|---|---|---|---|
| L.B.M. | | G. Musayeva | | | |
| Konstruktor | | M. Əzizov | | | |
| Norm. nəzarət | | S. Şükürova | | | |

Sifarişçi: Cəfərov Mədət İslam oğlu

DK-MK

Abşeron rayonu, Qobu qəsəbəsində yerləşən torpaq sahəsində tikintisi nəzərdə tutulan anbar və inzibati binası anbar binası.

| Anbar binası | Mərhələ | Vərəq | Vərəqlər |
|---|---|---|---|
| | İ.L. | 25 | |

Ferma "F-1"

"STORM BUİLDİNG" MMC

Format A3

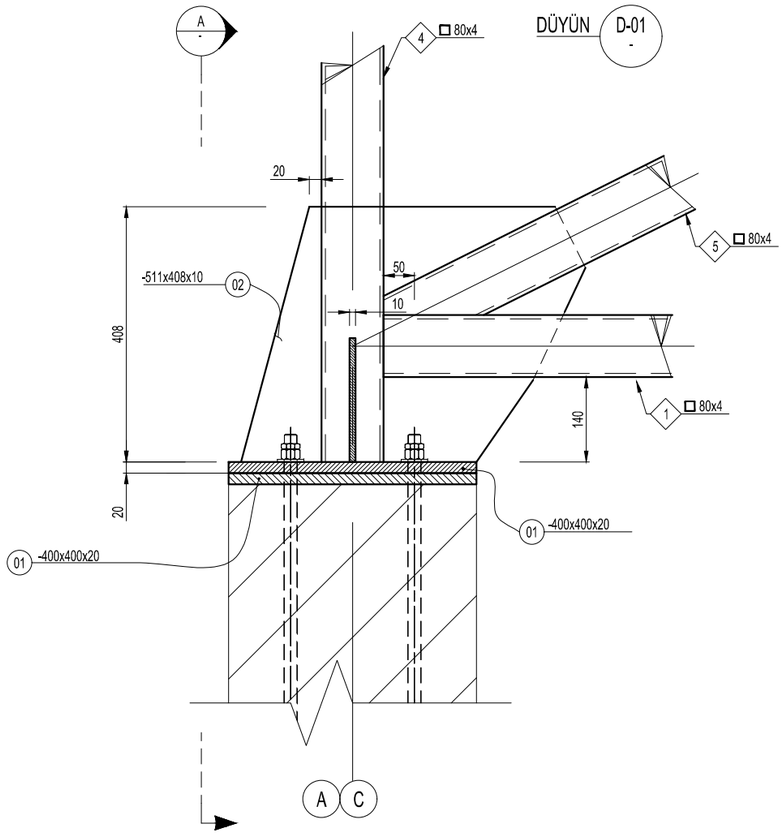


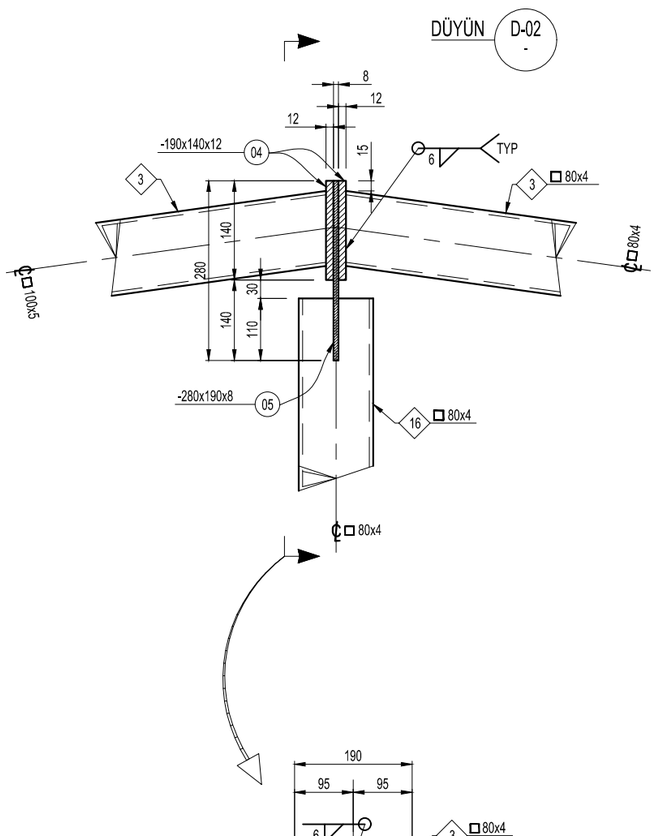


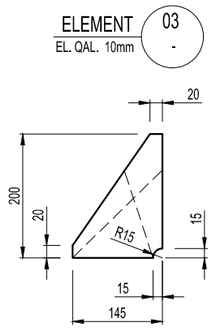


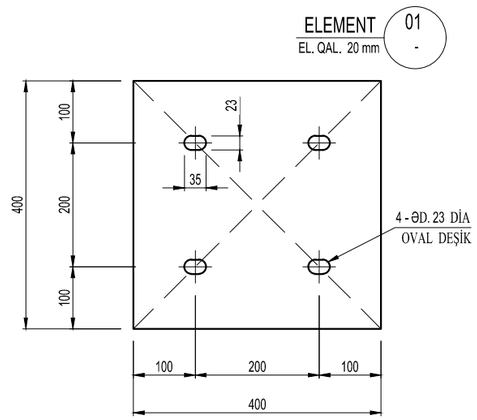


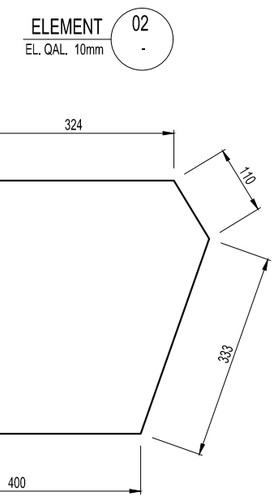


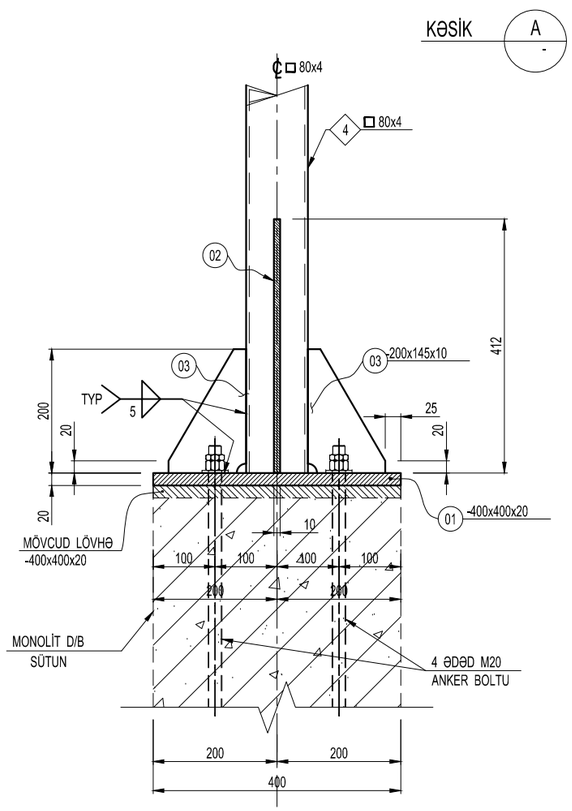


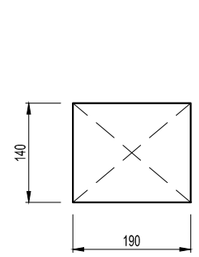


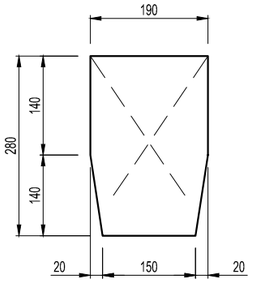


ELEMENT 04
EL. QAL. 12mm
-

ELEMENT 05
EL. QAL. 8mm
-

| | | | | | | | |
|---|---|---|---|---|---|---|---|
| | | | | | | Sifarişçi: Cəfərov Mədət İslam oğlu | DK-MK |
| Dəyiş | Sh.sən | Vərəq | Sən.№ | İmza | Tarix | Abşeron rayonu, Qobu qəsəbəsində yerləşən torpaq sahəsində tikintisi nəzərdə tutulan anbar və inzibati binası anbar binası. | |
| L.B.M. | | G. Musayeva | | | | Anbar binası | Mərhələ: İ.L. / Vərəq: 26 / Vərəqlər: |
| Konstruktor | | M. Əzizov | | | | Düyün "D-01" ; "D-02" | "STORM BUİLDİNG" MMC |
| Norm. nəzarət | | S. Şükürova | | | | | |

Razılaşdırılmışdır

İnvent № Əvəzinə

İmza və Tarix

İnvent № İmza

Format A3

DÜYÜN D-03 MK-18

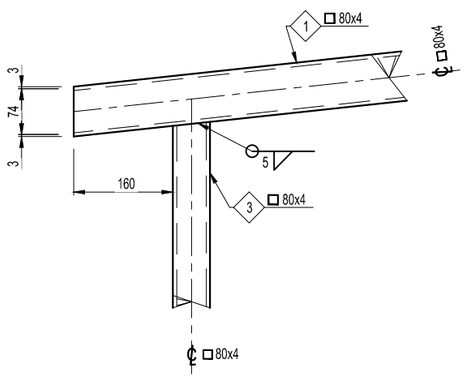


DÜYÜN D-04 MK-18

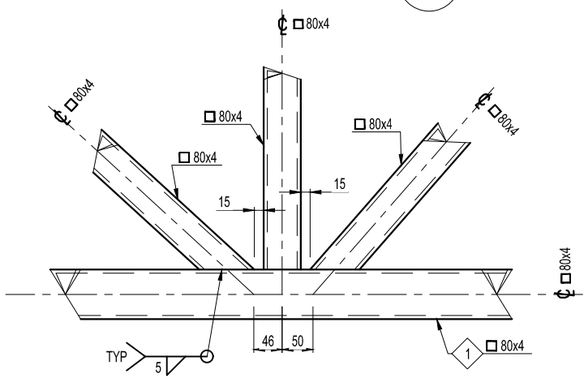


DÜYÜN D-05 MK-18

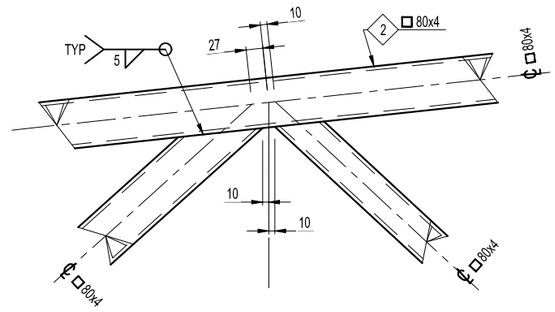


DÜYÜN D-06 MK-18

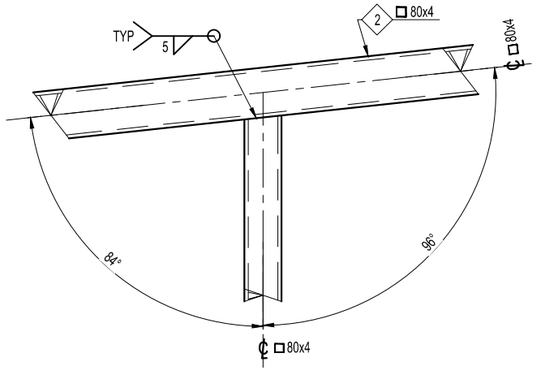


KƏSİK A -

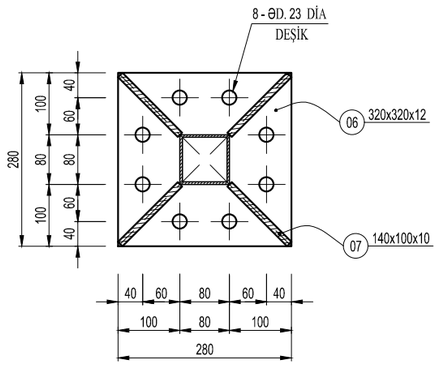


DÜYÜN D-07 MK-18

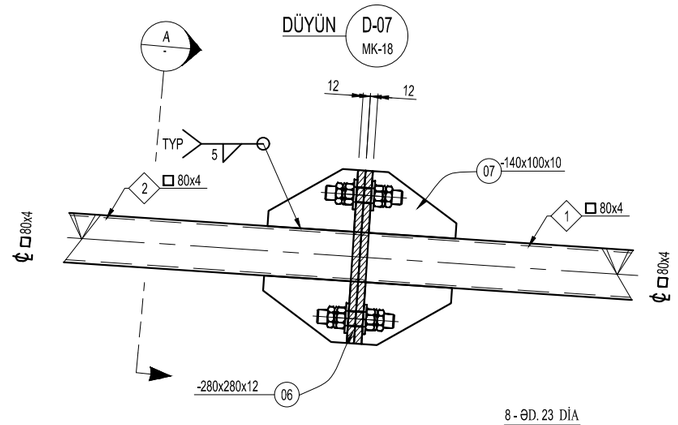


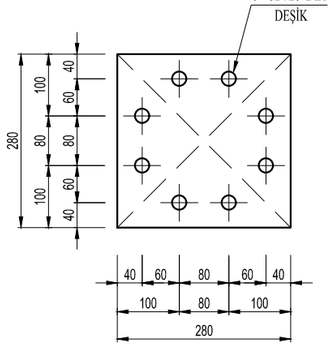


ELEMENT 06 - EL. QAL. 12mm

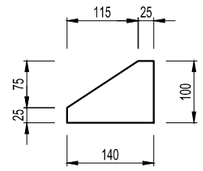


ELEMENT 07 - EL. QAL. 10mm

| | | | | | | | |
|---|---|---|---|---|---|---|---|
| | | | | | | Sifarişçi: Cəfərov Mədət İslam oğlu | DK-MK |
| Dəyiş | Sh.sən | Vərəq | Sən.№ | İmza | Tarix | Abşeron rayonu, Qobu qəsəbəsində yerləşən torpaq sahəsində tikintisi nəzərdə tutulan anbar və inzibati binası anbar binası. | |
| L.B.M. | | G. Musayeva | | | | Anbar binası | Mərhələ: İ.L. / Vərəq: 27 / Vərəqlər: |
| Konstruktor | | M. Əzizov | | | | | |
| Norm. nəzarət | | S. Şükürova | | | | DÜYÜN "D-03" , DÜYÜN "D-04" , "DÜYÜN "D-05" , "DÜYÜN "D-06" , DÜYÜN "D-07" | "STORM BUİLDİNG" MMC |

Format A3

Razılaşdırılmışdır

İnvent № Əvəzinə

İmza və Tarix

İnvent № İmza

DÜYÜN D-08 -

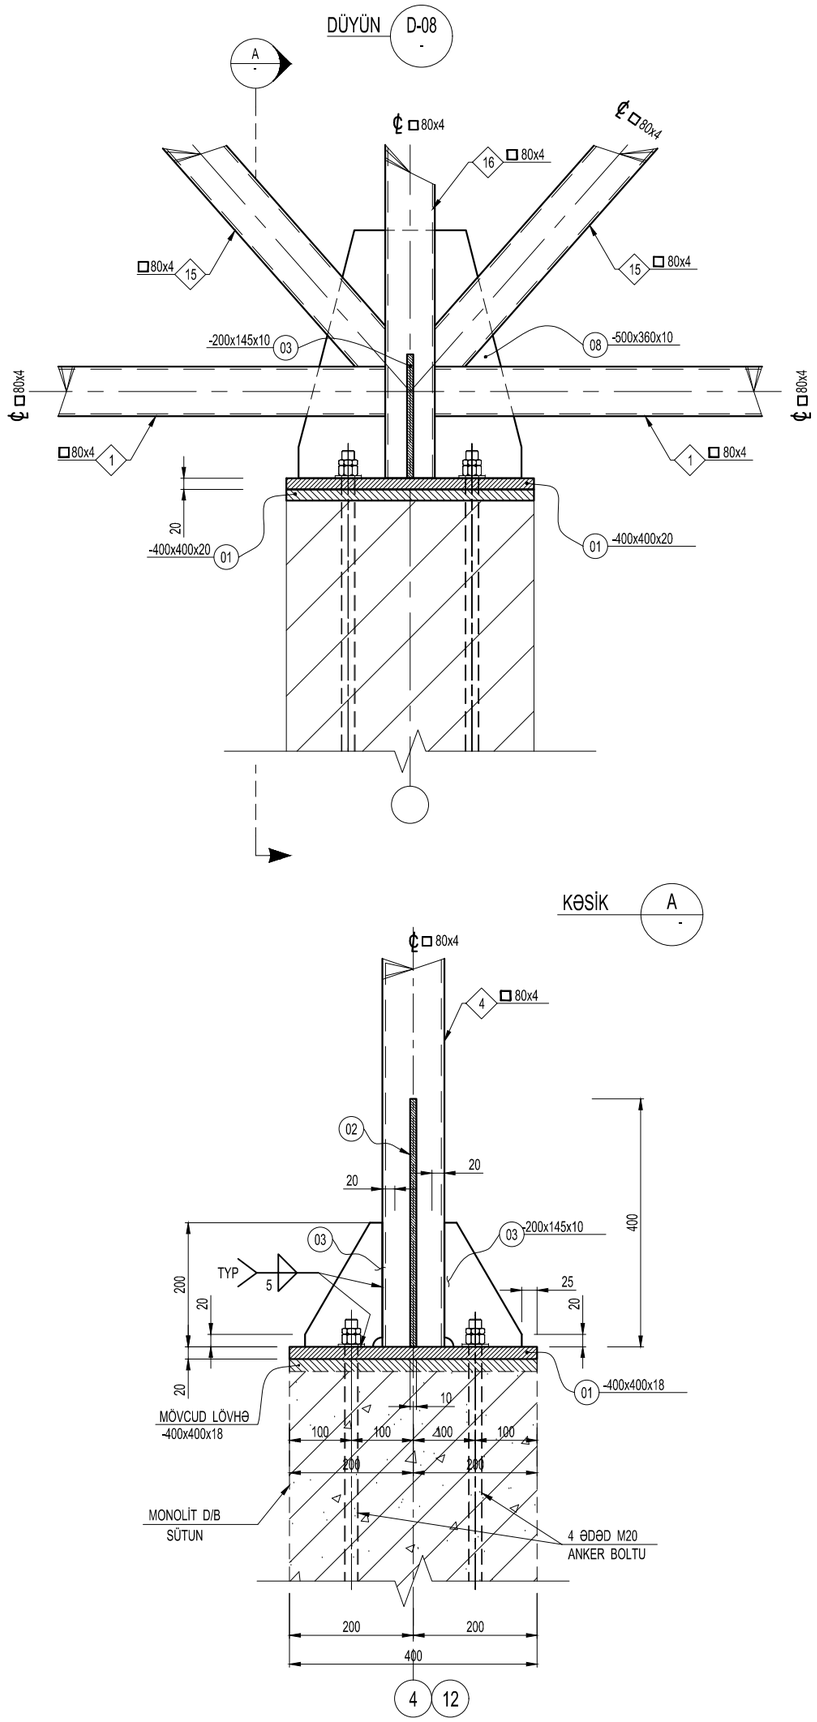


KƏSİK A -




ELEMENT 01 - EL. QAL. 18mm

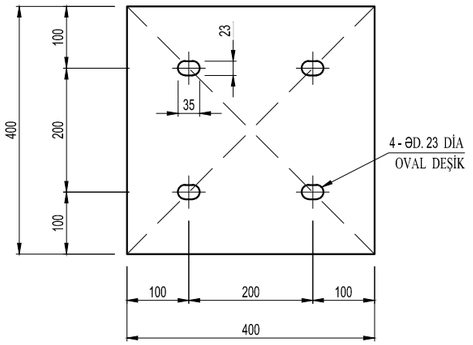


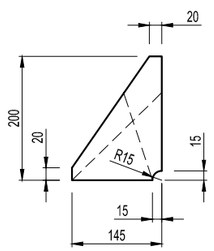


ELEMENT 03 - EL. QAL. 10mm

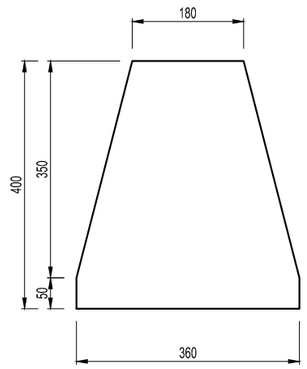


ELEMENT 08 - EL. QAL. 10mm

| | | | | | | | |
|---|---|---|---|---|---|---|---|
| | | | | | | Sifarişçi: Cəfərov Mədət İslam oğlu | DK-MK |
| Dəyiş | Sh.sən | Vərəq | Sən.№ | İmza | Tarix | Abşeron rayonu, Qobu qəsəbəsində yerləşən torpaq sahəsində tikintisi nəzərdə tutulan anbar və inzibati binası anbar binası. | |
| L.B.M. | | G. Musayeva | | | | Anbar binası | Mərhələ: İ.L. / Vərəq: 28 / Vərəqlər: |
| Konstruktor | | M. Əzizov | | | | DÜYÜN "D-08" | "STORM BUİLDİNG" MMC |
| Norm. nəzarət | | S. Şükürova | | | | | |

Razılaşdırılmışdır

İnvent № Əvəzinə

İmza və Tarix

İnvent № İmza

Format A3

## METAL ELEMENTLƏRİN TƏSNİFATI.

| ELEMENTİN MARKASI. | DET- N , S/S. | EN KƏSİYİ , MM. | UZUNLUQ , MM. | SAYI ƏD: | KÜTLƏSİ , Kq | | | POLADIN MARKASI. | DÜİST. |
|---|---|---|---|---|---|---|---|---|---|
| | | | | | BİR DETAL. | ÜMUMİ DETAL. | YEKUN. | | |
| | PROFİLLƏR | | | | | | | | |
| FERMA F-1 ( 1 ƏDƏD ÜÇÜN ) | 1 | □ 80x80x4 | 11920 | 2 | 106.10 | 212.20 | 828.26 | C245 | 27772-88 |
| | 2 | □ 80x80x4 | 7000 | 2 | 62.30 | 124.60 | | ---- | ---- |
| | 3 | □ 80x80x4 | 5187 | 2 | 46.16 | 92.32 | | ---- | ---- |
| | 4 | □ 80x80x4 | 1100 | 2 | 9.79 | 19.58 | | ---- | ---- |
| | 5 | □ 80x80x4 | 1720 | 2 | 15.30 | 30.60 | | ---- | ---- |
| | 6 | □ 80x80x4 | 1730 | 2 | 15.40 | 30.80 | | ---- | ---- |
| | 7 | □ 80x80x4 | 1123 | 2 | 10.00 | 20.00 | | ---- | ---- |
| | 8 | □ 80x80x4 | 1860 | 2 | 16.55 | 33.10 | | ---- | ---- |
| | 9 | □ 80x80x4 | 1870 | 2 | 16.65 | 33.30 | | ---- | ---- |
| | 10 | □ 80x80x4 | 1323 | 2 | 11.77 | 23.54 | | ---- | ---- |
| | 11 | □ 80x80x4 | 2004 | 2 | 17.84 | 35.68 | | ---- | ---- |
| | 12 | □ 80x80x4 | 2012 | 2 | 17.90 | 35.80 | | ---- | ---- |
| | 13 | □ 80x80x4 | 1523 | 2 | 13.55 | 27.10 | | ---- | ---- |
| | 14 | □ 80x80x4 | 2155 | 2 | 19.18 | 38.36 | | ---- | ---- |
| | 15 | □ 80x80x4 | 2160 | 2 | 19.22 | 38.44 | | ---- | ---- |
| | 16 | □ 80x80x4 | 1845 | 2 | 16.42 | 32.84 | | ---- | ---- |
| | | | | | | | | ---- | ---- |
| | | | | | | | | ---- | ---- |
| | | | | | | | | ---- | ---- |
| | | | | | | | | ---- | ---- |
| | | | | | | | | ---- | ---- |
| | METAL VƏRƏQƏLƏR | | | | | | | | |
| | 01 | - 400x20 | 400 | 6 | 25.12 | 150.72 | 253.36 | C245 | ---- |
| | 02 | - 511x10 | 408 | 2 | 16.36 | 32.72 | | ---- | ---- |
| | 03 | - 145x10 | 200 | 4 | 2.28 | 9.12 | | ---- | ---- |
| | 04 | - 190x12 | 140 | 2 | 2.5 | 5.0 | | ---- | ---- |
| | 05 | - 280x8 | 190 | 1 | 3.35 | 3.35 | | ---- | ---- |
| | 06 | - 280x12 | 280 | 4 | 7.38 | 29.52 | | ---- | ---- |
| | 07 | - 140x10 | 100 | 8 | 1.10 | 8.80 | | ---- | ---- |
| | 08 | - 500x10 | 360 | 1 | 14.13 | 14.13 | | ---- | ---- |

Razılaşdırılmışdır

İnvent № Əvəzinə

İmza və Tarix

İnvent № İmza

| Dəyiş | Sh.sən | Vərəq | Sən.№ | İmza | Tarix |
|---|---|---|---|---|---|
| L.B.M. | | G. Musayeva | | | |
| Konstruktor | | M. Əzizov | | | |
| Norm. nəzarət | | S. Şükürova | | | |

Sifarişçi: Cəfərov Mədət İslam oğlu — DK-MK

Abşeron rayonu, Qobu qəsəbəsində yerləşən torpaq sahəsində tikintisi nəzərdə tutulan anbar və inzibati binası anbar binası.

| Anbar binası | Mərhələ | Vərəq | Vərəqlər |
|---|---|---|---|
| | İ.L. | 29 | |

FERMA "F-1" ÜÇÜN MATERİAL SƏRFİ

"STORM BUİLDİNG" MMC

Format A3

Şaquli rabitə Şr-1 (4 ədəd)

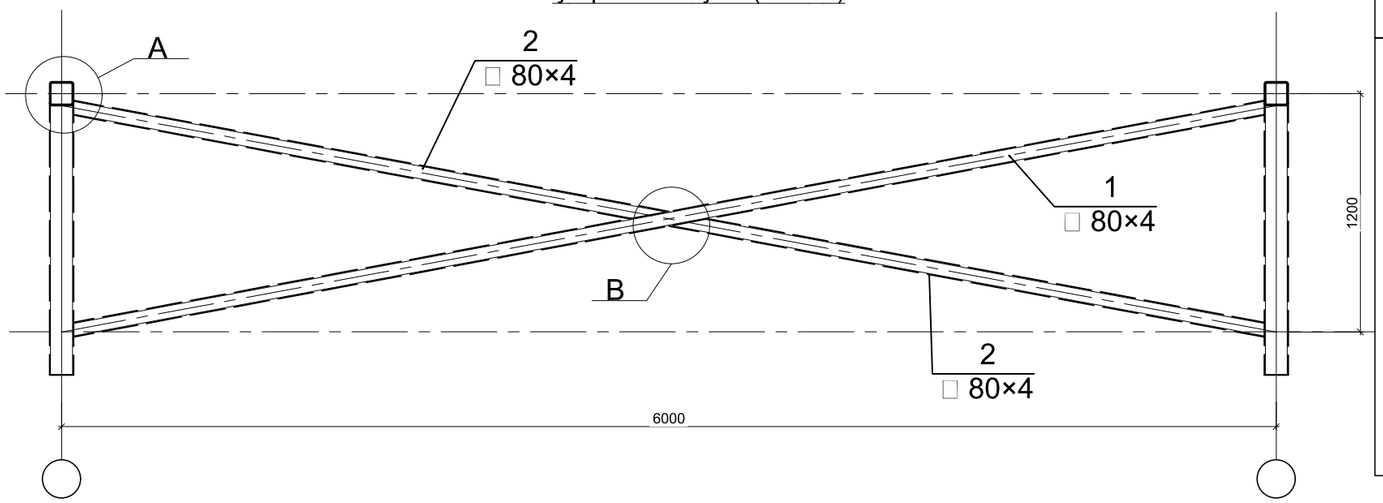


METAL ELEMENTLƏRİN TƏSNİFATI (ümumi).

| ELEMENTİN MARKASI. | DET-N, S/S. | EN KƏSİYİ, MM. | UZUNLUQ, MM. | SAYI ƏD: | KÜTLƏSİ, Kq | | | POLADIN MARKASI. |
|---|---|---|---|---|---|---|---|---|
| | | | | | BİR DETAL. | ÜMUMİ DETAL. | YEKUN.. +1.01 | |
| FERMALAR ARASI ŞAQULİ RABİTƏ | PROFİLLƏR | | | | | | | |
| | 1 | □ 80x4 | 5650 | 4 | 50.29 | 201.16 | 402.28 | C245 |
| | 2 | □ 80x4 | 2825 | 8 | 25.14 | 201.12 | | C245 |
| | | | | | | | | C245 |
| | | | | | | | | C245 |
| | | | | | | | | |
| | | | | | | | | |
| | METAL VƏRƏQƏLƏR | | | | | | 140.6 | |
| | 3 | - 120x8 | 260 | 24 | 1.96 | 47.1 | | C255 |
| | 4 | - 217x8 | 262 | 16 | 3.57 | 57.1 | | C255 |
| | 5 | - 254x8 | 274 | 8 | 4.37 | 35.0 | | C255 |
| | | | | | | | | C255 |
| | | | | | | | | C255 |
| | | | | | | | | C255 |

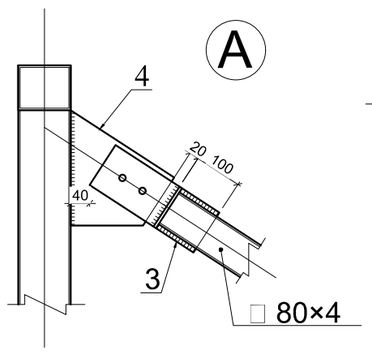


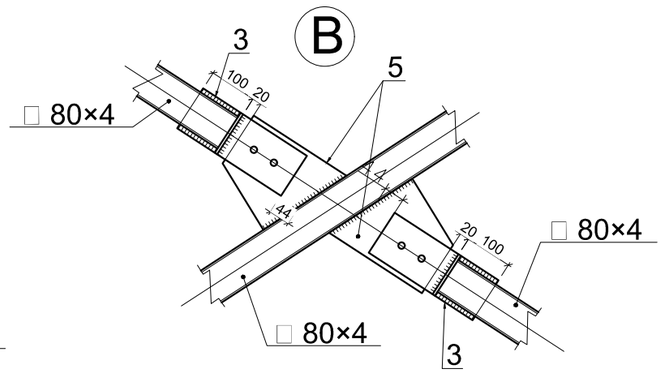


Mövqe -3

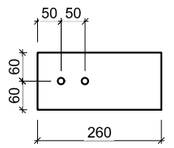


Mövqe -4

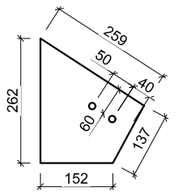


Mövqe -5

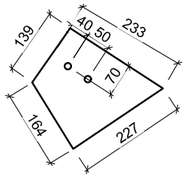


| Dəyiş | Sh.sən | Vərəq | Sən.№ | İmza | Tarix |
|---|---|---|---|---|---|
| L.B.M. | | G. Musayeva | | | |
| Konstruktor | | M. Əzizov | | | |
| Norm. nəzarət | | S. Şükürova | | | |

Sifarişçi: Cəfərov Mədət İslam oğlu — DK-MK

Abşeron rayonu, Qobu qəsəbəsində yerləşən torpaq sahəsində tikintisi nəzərdə tutulan anbar və inzibati binası anbar binası.

| Anbar binası | Mərhələ | Vərəq | Vərəqlər |
|---|---|---|---|
| | İ.L. | 30 | |

Şaquli rabitə Şr-1 — "STORM BUİLDİNG" MMC

Format A3

Razılaşdırılmışdır

İnvent № Əvəzinə

İmza və Tarix

İnvent № İmza

## Şaquli rabitə Şr-2 (4 ədəd)

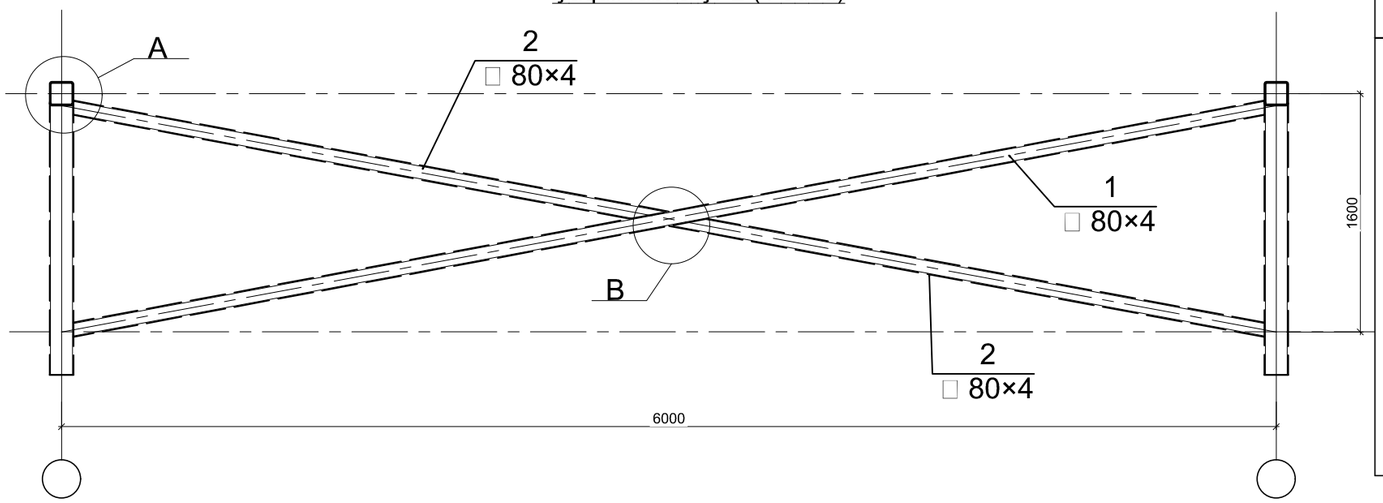


### METAL ELEMENTLƏRİN TƏSNİFATI.

| ELEMENTİN MARKASI. | DET-N, S/S. | EN KƏSİYİ, MM. | UZUNLUQ, MM. | SAYI ƏD: | KÜTLƏSİ, Kq | | | POLADIN MARKASI. |
|---|---|---|---|---|---|---|---|---|
| | | | | | BİR DETAL. | ÜMUMİ DETAL. | YEKUN.. +1.01 | |
| FERMALAR ARASI ŞAQULİ RABİTƏ | | PROFİLLƏR | | | | | | |
| | 1 | □ 80x4 | 5740 | 4 | 51.10 | 404.40 | 808.80 | C245 |
| | 2 | □ 80x4 | 2870 | 8 | 25.55 | 404.40 | | C245 |
| | | | | | | | | C245 |
| | | | | | | | | C245 |
| | | | | | | | | |
| | | | | | | | | |
| | | METAL VƏRƏQƏLƏR | | | | | 140.6 | |
| | 3 | - 120x8 | 260 | 24 | 1.96 | 47.1 | | C255 |
| | 4 | - 217x8 | 262 | 16 | 3.57 | 57.1 | | C255 |
| | 5 | - 254x8 | 274 | 8 | 4.37 | 35.0 | | C255 |
| | | | | | | | | C255 |
| | | | | | | | | C255 |
| | | | | | | | | C255 |

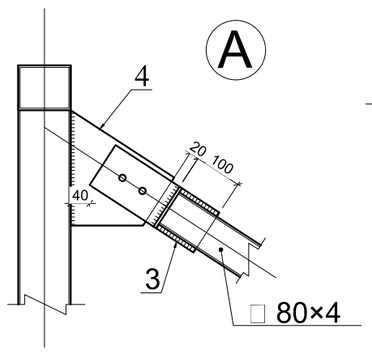


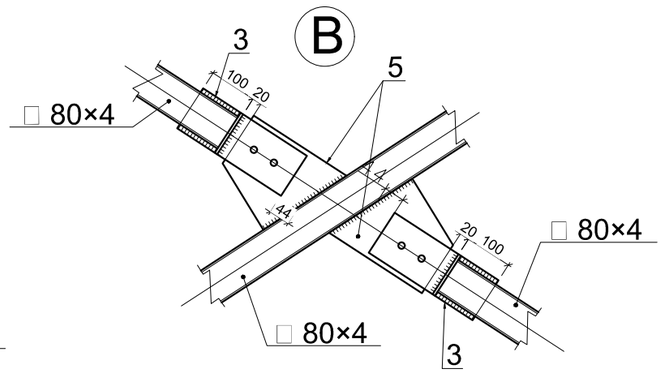


Mövqe -3

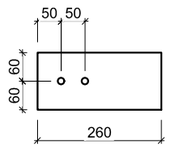


Mövqe -4

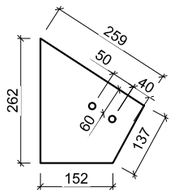


Mövqe -5

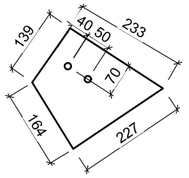


| | | | | | | | |
|---|---|---|---|---|---|---|---|
| | | | | | | Sifarişçi: Cəfərov Mədət İslam oğlu | DK-MK |
| Dəyiş | Sh.sən | Vərəq | Sən.№ | İmza | Tarix | Abşeron rayonu, Qobu qəsəbəsində yerləşən torpaq sahəsində tikintisi nəzərdə tutulan anbar və inzibati binası anbar binası. | |
| L.B.M. | | G. Musayeva | | | | Anbar binası | Mərhələ: İ.L. / Vərəq: 31 / Vərəqlər |
| Konstruktor | | M. Əzizov | | | | | |
| Norm. nəzarət | | S. Şükürova | | | | Şaquli rabitə Şr-2 | "STORM BUİLDİNG" MMC |

Razılaşdırılmışdır

İnvent № Əvəzinə

İmza və Tarix

İnvent № İmza

Format A3

Fermaların alt kəmər üzrə üfiqi rabitələrin və dartqiların yerləşmə planı.

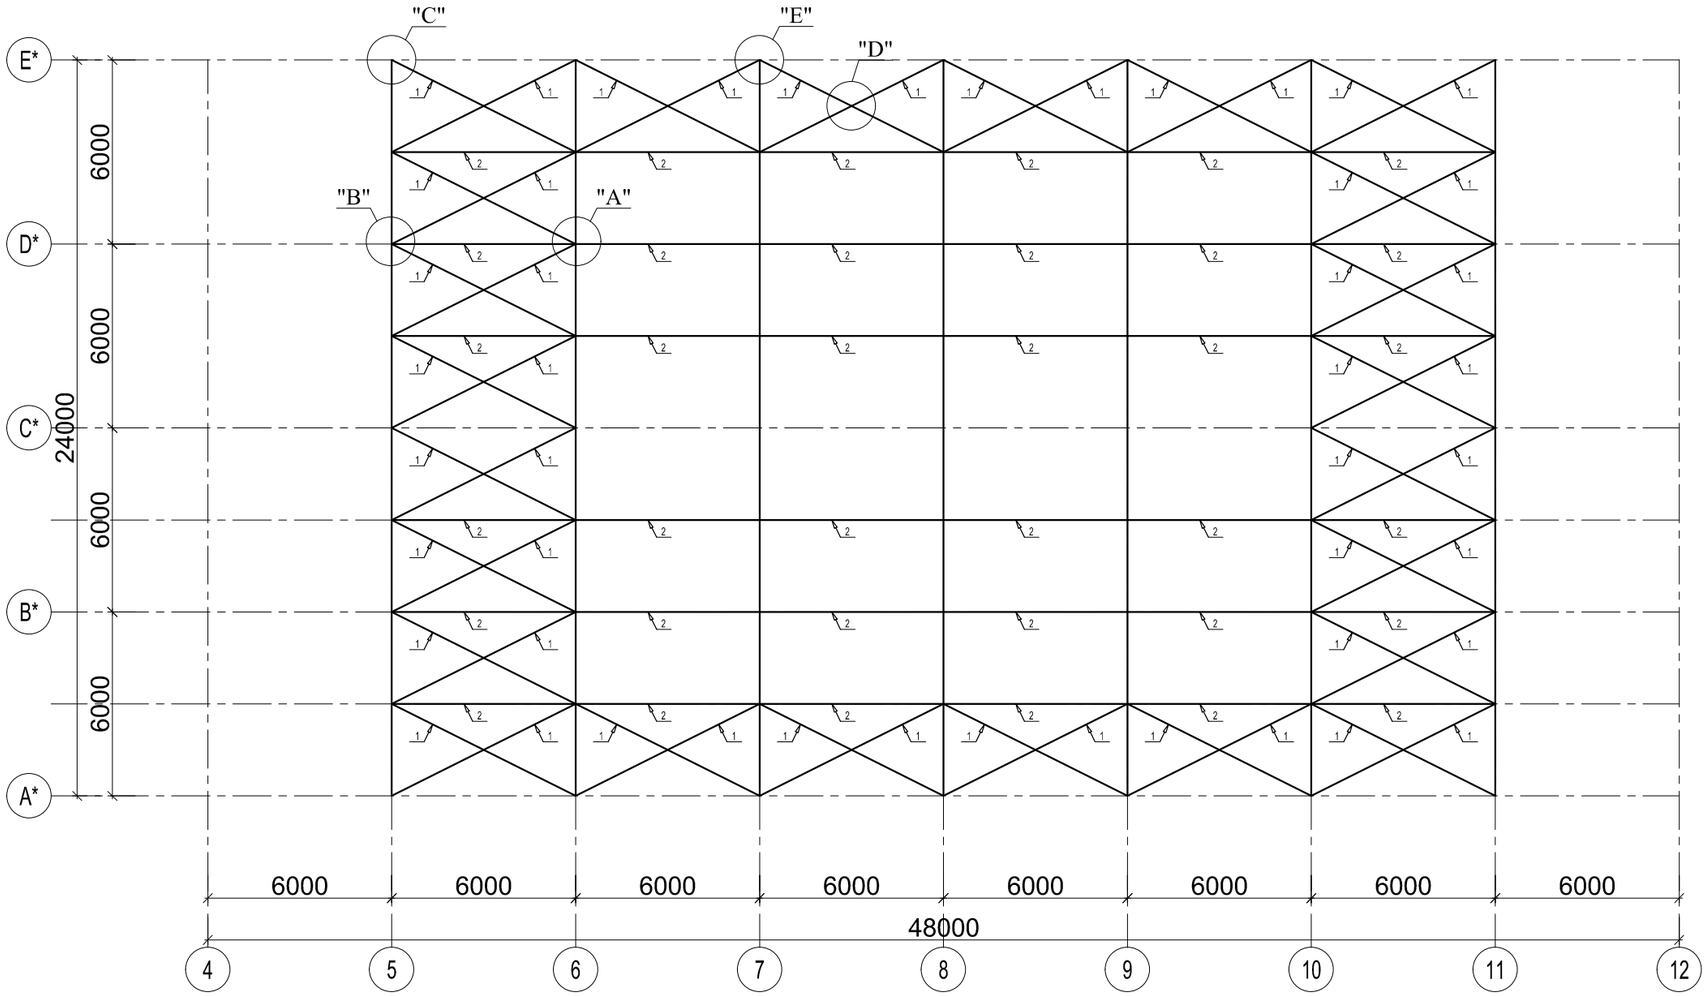


Qeyd:

1. Metal profillərdə işlənilən poladın markası C 245, birləşdirici metal vərəqlərdə işlənilən poladın markası C 245 qəbul edilmişdir.
2. Qaynağı Э-42A (ГОСТ9467-75). tipli elektrodla aparmaq lazımdır.
3. Tikişin qalınlığı (ГОСТ 9467-73*) qaynaq edilən nazik elementin (ən azı) qalınlığına bərabər olmalıdır.
4. Qaynaqların qalınlığı 6 mm -dir. Quraşdırma boltları 8.8 (ГОСТ 1759.4-87) siniflidir.
5. Bütün metal konstruksiyaları paslanmadan təmizləyib tez quruyan ПФ 1189 emalı ilə iki dəfə rənglənməlidir.

| Dəyiş | Sh.sən | Vərəq | Sən.№ | İmza | Tarix |
|---|---|---|---|---|---|
| L.B.M. | | G. Musayeva | | | |
| Konstruktor | | M. Əzizov | | | |
| Norm. nəzarət | | S. Şükürova | | | |

Sifarişçi: Cəfərov Mədət İslam oğlu — DK-MK

Abşeron rayonu, Qobu qəsəbəsində yerləşən torpaq sahəsində tikintisi nəzərdə tutulan anbar və inzibati binası anbar binası.

| Anbar binası | Mərhələ | Vərəq | Vərəqlər |
|---|---|---|---|
| | İ.L. | 32 | |

Fermaların alt kəmər üzrə üfiqi rabitələrin və dartqiların yerləşmə planı

"STORM BUİLDİNG" MMC

Format A3

Razılaşdırılmışdır

İnvent № Əvəzinə

İmza və Tarix

İnvent № İmza

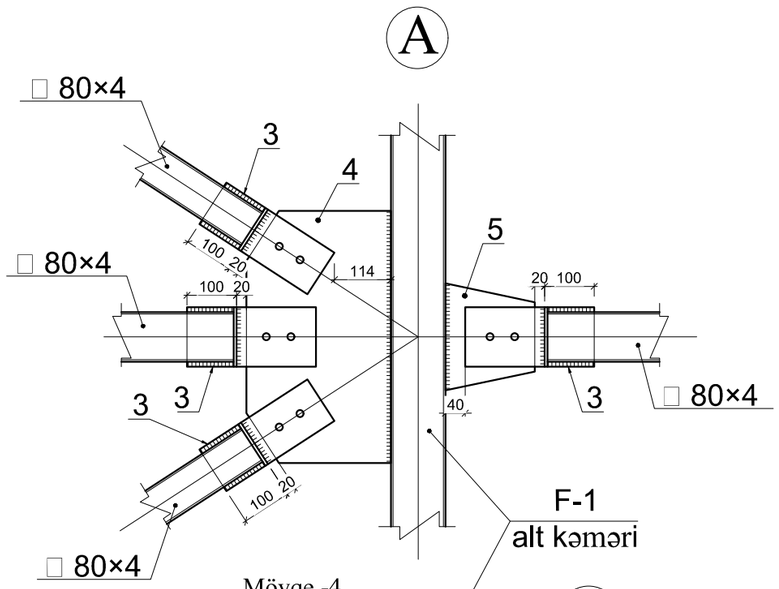


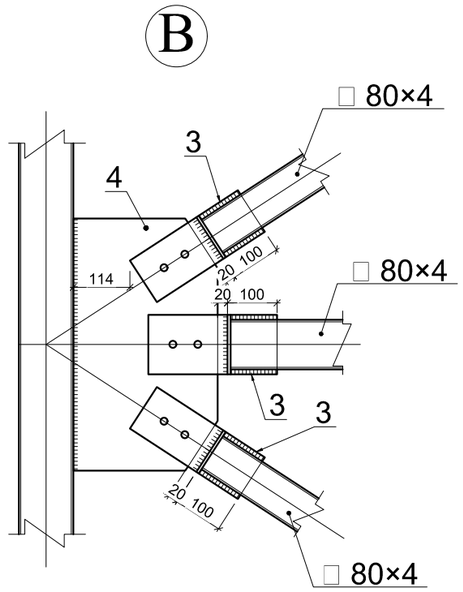


Mövqe -4

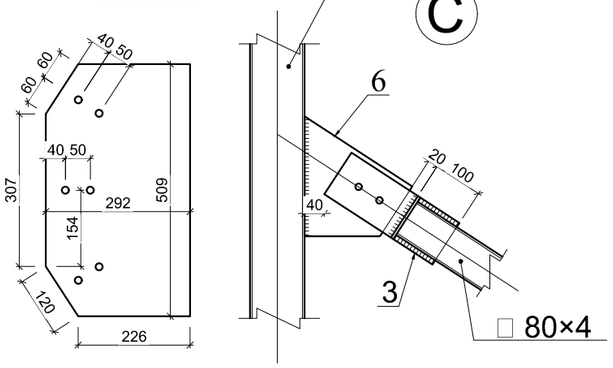


Mövqe -3

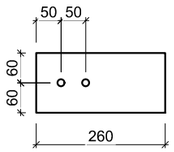


Mövqe -5

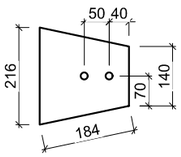


Mövqe -6

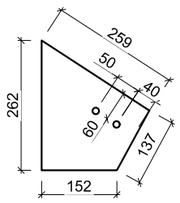


Mövqe -7

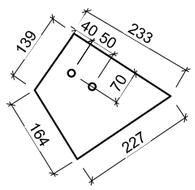


METAL ELEMENTLƏRİN TƏSNİFATI.

| ELEMENTİN MARKASI. | DET-N, S/S. | EN KƏSİYİ, MM. | UZUNLUQ, MM. | SAYI ƏD: | KÜTLƏSİ, Kq | | | POLADIN MARKASI. |
|---|---|---|---|---|---|---|---|---|
| | | | | | BİR DETAL. | ÜMUMİ DETAL. | YEKUN.. +1.01 | |
| AŞAĞI KƏMƏR ÜZRƏ ÜFİQİ RABİTƏLƏR "AKR-01", "AKR-02", "AKR-03", "AKR-04" | PROFİLLƏR | | | | | | | |
| | 1 | □ 80x4 | 6700 | 48 | 59.63 | 2862.24 | 4784.64 | C245 |
| | 2 | □ 80x4 | 6000 | 36 | 53.40 | 1922.40 | | C245 |
| | | | | | | | | |
| | | | | | | | | |
| | | | | | | | | |
| | | | | | | | | |
| | METAL VƏRƏQƏLƏR | | | | | | | |
| | 3 | - 120x8 | 260 | 168 | 1.96 | 329.30 | 926.10 | C255 |
| | 4 | - 292x8 | 509 | 24 | 9.3 | 223.20 | | C255 |
| | 5 | - 180x8 | 216 | 32 | 2.44 | 78.10 | | C255 |
| | 6 | - 217x8 | 262 | 24 | 3.57 | 85.70 | | C255 |
| | 7 | - 254x8 | 274 | 48 | 4.37 | 209.80 | | C255 |
| | | | | | | | | |

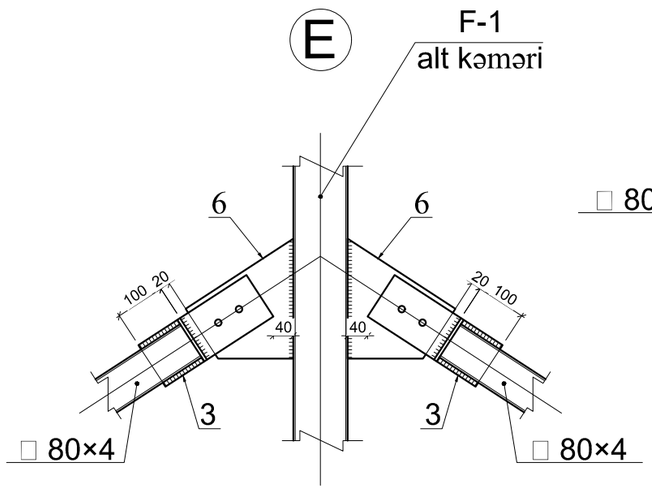


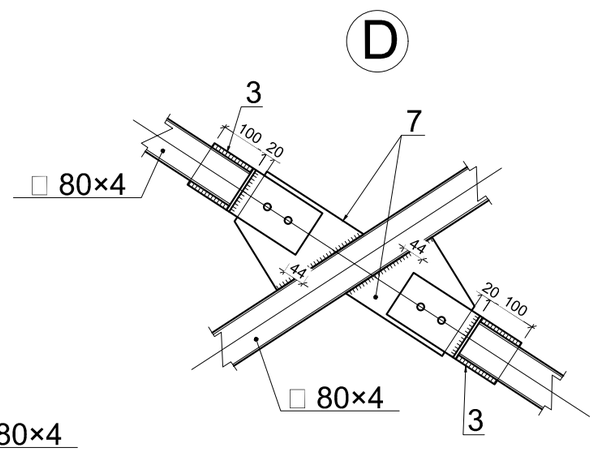


| | | | | | | | |
|---|---|---|---|---|---|---|---|
| | | | | | | Sifarişçi: Cəfərov Mədət İslam oğlu | DK-MK |
| Dəyiş | Sh.sən | Vərəq | Sən.№ | İmza | Tarix | Abşeron rayonu, Qobu qəsəbəsində yerləşən torpaq sahəsində tikintisi nəzərdə tutulan anbar və inzibati binası anbar binası. | |
| L.B.M. | | G. Musayeva | | | | Anbar binası | Mərhələ: İ.L. Vərəq: 33 Vərəqlər: |
| Konstruktor | | M. Əzizov | | | | Alt kəmər üzrə üfiqi rabitə və dartqilarin düyünləri : | "STORM BUİLDİNG" MMC |
| Norm. nəzarət | | S. Şükürova | | | | | |

Razılaşdırılmışdır

İnvent № Əvəzinə

İmza və Tarix

İnvent № İmza

Format A3

Fermalarin üst kəmər üzrə üfiqi rabitələrin yerləşmə plani.

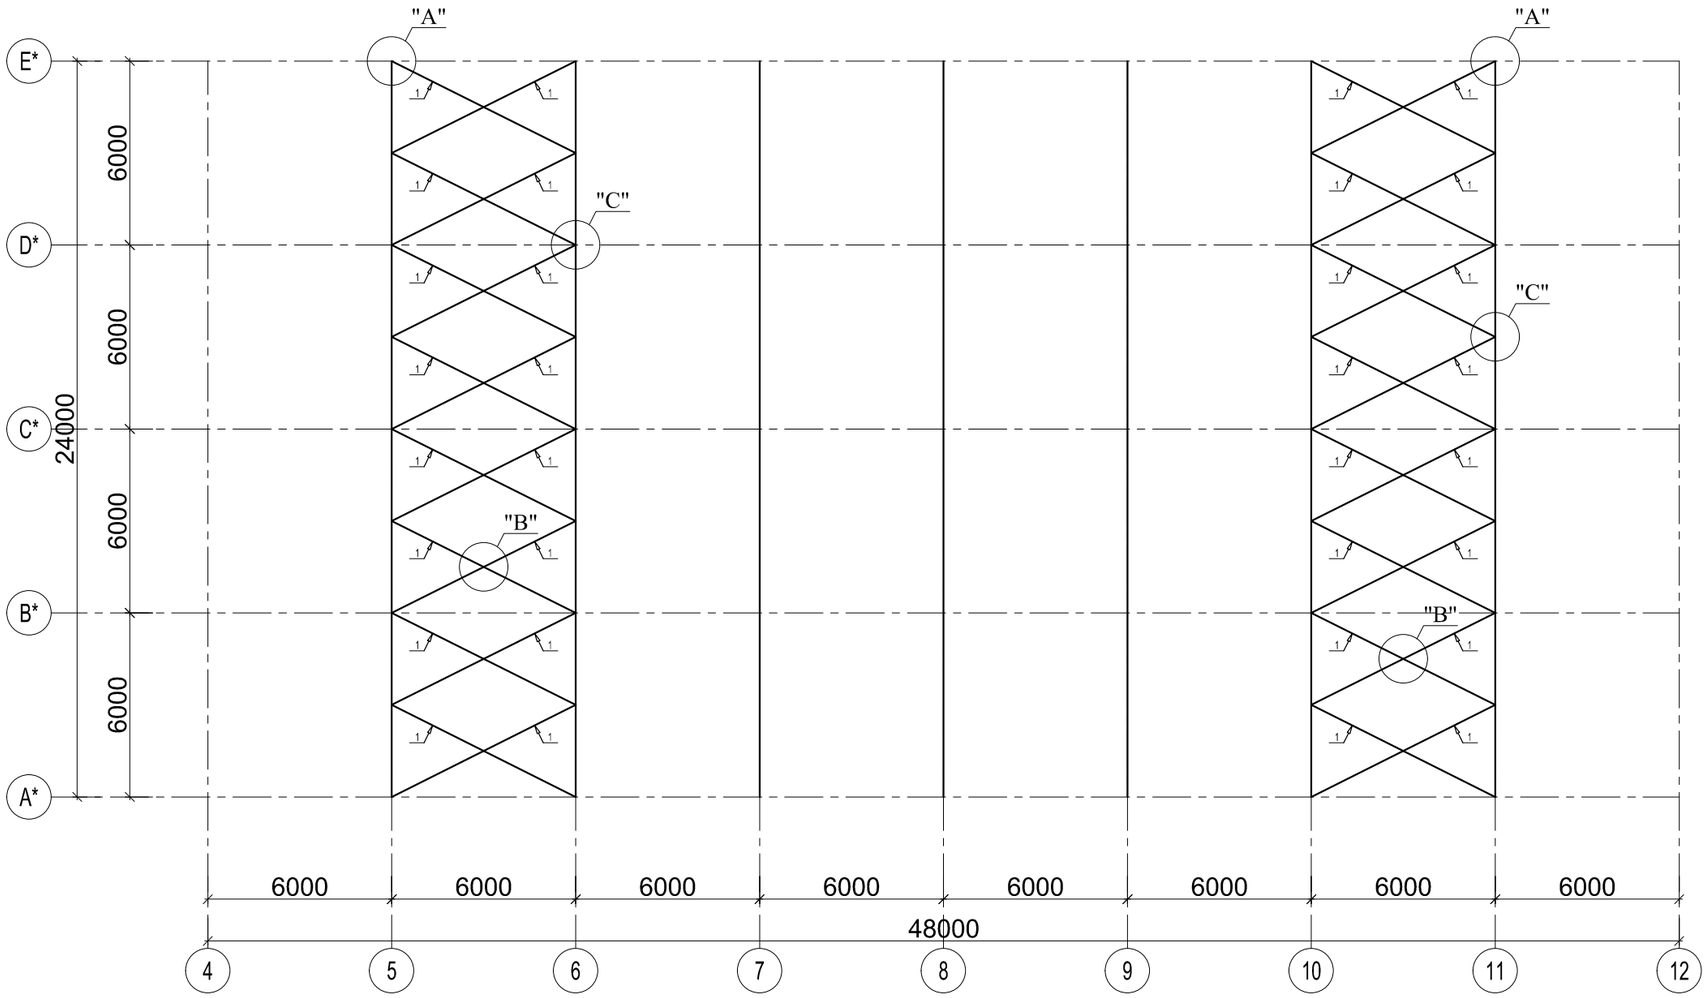


Qeyd:

1. Metal profillərdə işlənilən poladın markası C 245, birləşdirici metal vərəqlərdə işlənilən poladın markası C 245 qəbul edilmişdir.
2. Qaynağı Э-42A (ГОСТ9467-75). tipli elektrodla aparmaq lazımdır.
3. Tikişin qalınlığı (ГОСТ 9467-73*) qaynaq edilən nazik elementin (ən azı) qalınlığına bərabər olmalıdır.
4. Qaynaqların qalınlığı 6 mm -dir. Quraşdırma boltları 8.8 (ГОСТ 1759.4-87) siniflidir.
5. Bütün metal konstruksiyaları paslanmadan təmizləyib tez quruyan ПФ 1189 emalı ilə iki dəfə rənglənməlidir.

| | | | | | | | |
|---|---|---|---|---|---|---|---|
| | | | | | | Sifarişçi: Cəfərov Mədət İslam oğlu | DK-MK |
| Dəyiş | Sh.sən | Vərəq | Sən.№ | İmza | Tarix | Abşeron rayonu, Qobu qəsəbəsində yerləşən torpaq sahəsində tikintisi nəzərdə tutulan anbar və inzibati binası anbar binası. | |
| L.B.M. | | G. Musayeva | | | | Anbar binası | Mərhələ: İ.L. / Vərəq: 34 / Vərəqlər: |
| Konstruktor | | M. Əzizov | | | | | |
| Norm. nəzarət | | S. Şükürova | | | | Fermalarin üst kəmər üzrə üfüqi rabitələrin yerləşmə planı | "STORM BUİLDİNG" MMC |

Format A3

Razılaşdırılmışdır

İnvent № Əvəzinə

İmza və Tarix

İnvent №

İmza

A

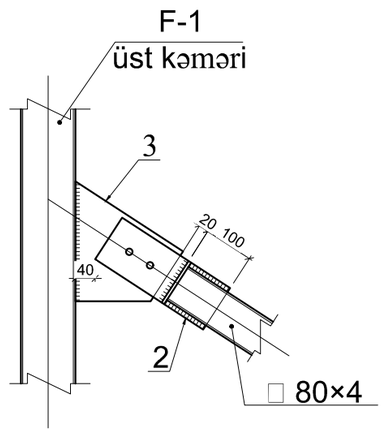


B

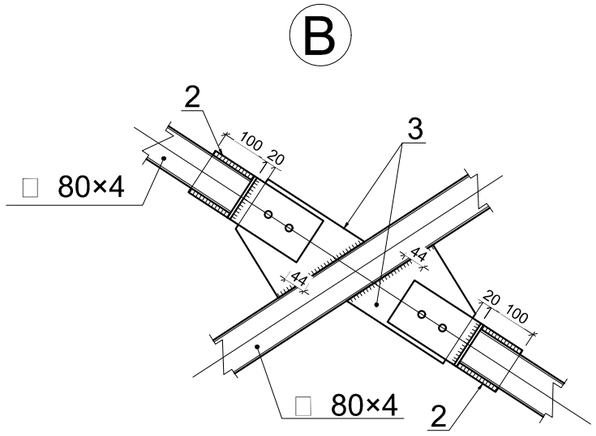


C

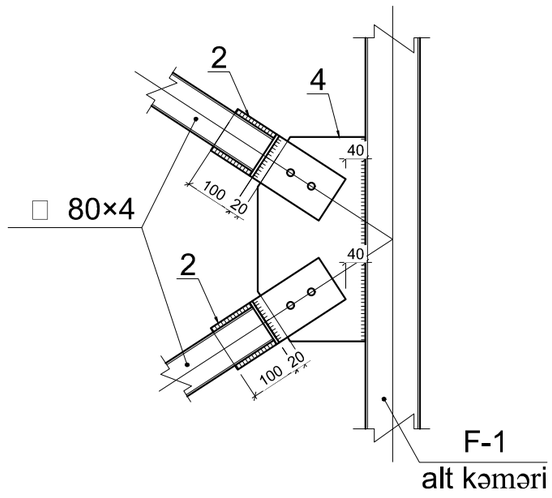


METAL ELEMENTLƏRİN TƏSNİFATI.

| ELEMENTİN MARKASI. | DET-N , S/S. | EN KƏSİYİ , MM. | UZUNLUQ , MM. | SAYI ƏD: | KÜTLƏSİ , Kq | | | POLADIN MARKASI. |
|---|---|---|---|---|---|---|---|---|
| | | | | | BİR DETAL. | ÜMUMİ DETAL. | YEKUN.. +1.01 | |
| ÜST KƏMƏR ÜZRƏ ÜFİQİ RABİTƏLƏR | PROFİLLƏR | | | | | | | |
| | 1 | □ 80x4 | 6700 | 32 | 59.63 | 1908.16 | 1908.16 | C245 |
| | | | | | | | | |
| | | | | | | | | |
| | | | | | | | | |
| | METAL VƏRƏQƏLƏR | | | | | | 401.88 | |
| | 2 | - 120x8 | 260 | 64 | 1.96 | 125.44 | | C255 |
| | 3 | - 217x8 | 274 | 32 | 3.73 | 119.36 | | C255 |
| | 4 | - 217x8 | 412 | 28 | 5.61 | 157.08 | | C255 |
| | | | | | | | | C255 |
| | | | | | | | | |
| | | | | | | | | |

Mövqe -2

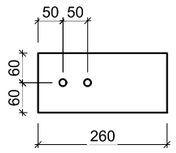


Mövqe -3

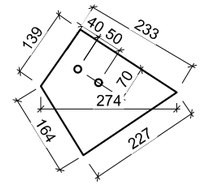


Mövqe -4

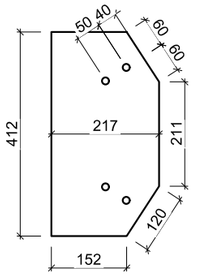


Razılaşdırılmışdır

İnvent № Əvəzinə

İmza və Tarix

İnvent № İmza

| | | | | | | | |
|---|---|---|---|---|---|---|---|
| | | | | | | Sifarişçi: Cəfərov Mədət İslam oğlu | DK-MK |
| Dəyiş | Sh.sən | Vərəq | Sən.№ | İmza | Tarix | Abşeron rayonu, Qobu qəsəbəsində yerləşən torpaq sahəsində tikintisi nəzərdə tutulan anbar və inzibati binası anbar binası. | |
| L.B.M. | | G. Musayeva | | | | Anbar binası | Mərhələ / Vərəq / Vərəqlər |
| Konstruktor | | M. Əzizov | | | | | İ.L. / 35 / |
| Norm. nəzarət | | S. Şükürova | | | | Üst kəmər üzrə üfiqi rabitə düyünləri : | "STORM BUİLDİNG" MMC |

Format A3

## Proqonların yerləşmə planı. Material sərfi.

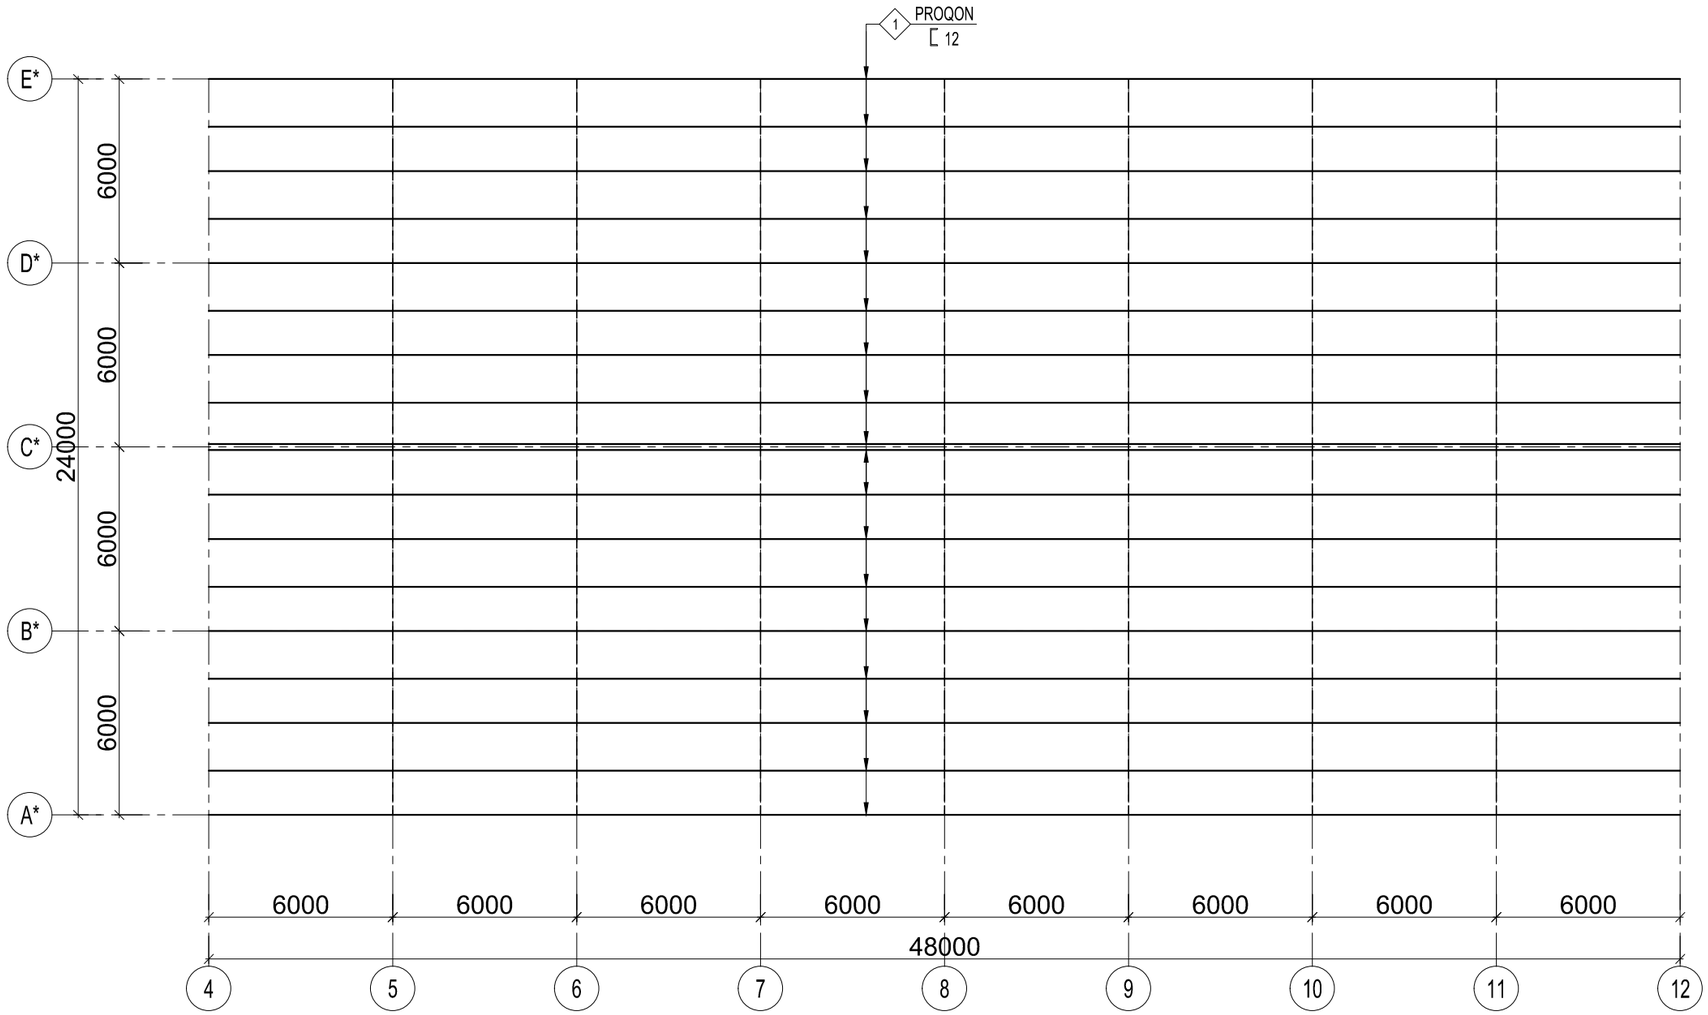


## Proqonun fermaya birləşmə düyünü

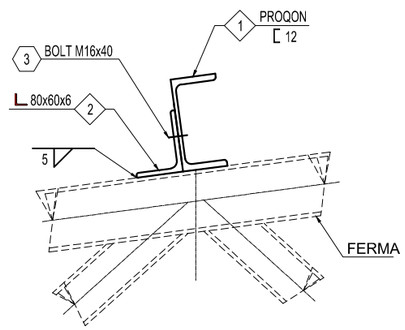


## METAL ELEMENTLƏRİN TƏSNİFATI.

| ELEMENTİN MARKASI. | DET- N , S/S. | EN KƏSİYİ , MM. | UZUNLUQ , MM. | SAYI ƏD: | KÜTLƏSİ , Kq | | | POLADIN MARKASI. | DÜİST. |
|---|---|---|---|---|---|---|---|---|---|
| | | | | | BİR DETAL. | ÜMUMİ DETAL. | YEKUN. | | |
| PROQON | 1 | [12 | 12000 | 72 | 124.8 | 8985.60 | 9068.30 | BCт3сп6 | 8509-93 |
| PROFİL | 2 | L 80x60x6 | 80 | 162 | 0.51 | 82.70 | | ----- | ---- |

### Qeyd:

1. Metal profillərdə işlənilən poladın markası C 245, birləşdirici metal vərəqlərdə işlənilən poladın markası C 245 qəbul edilmişdir.
2. Qaynağı Э-42A (ГОСТ9467-75). tipli elektrodla aparmaq lazımdır.
3. Tikişin qalınlığı (ГОСТ 9467-73*) qaynaq edilən nazik elementin (ən azı) qalınlığına bərabər olmalıdır.
4. Qaynaqların qalınlığı 6 mm -dir. Quraşdırma boltları 8.8 (ГОСТ 1759.4-87) siniflidir.
5. Bütün metal konstruksiyaları paslanmadan təmizləyib tez quruyan ПФ 1189 emalı ilə iki dəfə rənglənməlidir.

| Dəyiş | Sh.sən | Vərəq | Sən.№ | İmza | Tarix |
|---|---|---|---|---|---|
| L.B.M. | | G. Musayeva | | | |
| Konstruktor | | M. Əzizov | | | |
| Norm. nəzarət | | S. Şükürova | | | |

Sifarişçi: Cəfərov Mədət İslam oğlu — DK-MK

Abşeron rayonu, Qobu qəsəbəsində yerləşən torpaq sahəsində tikintisi nəzərdə tutulan anbar və inzibati binası anbar binası.

| Anbar binası | Mərhələ | Vərəq | Vərəqlər |
|---|---|---|---|
| | İ.L. | 36 | |

Proqonların yerləşmə planı. Material sərfi. — "STORM BUİLDİNG" MMC

Format A3

Razılaşdırılmışdır

İnvent № Əvəzinə

İmza və Tarix

İnvent № İmza

A Z Ə R B A Y C A N  R E S P U B L İ K A S I

"S T O R M  B U İ L D İ N G"

M ə h d u d  M ə s u l i y y ə t l i  C ə m i y y ə t

# ABŞERON RAYONU, QOBU QƏSƏBƏSİNDƏ YERLƏŞƏN TORPAQ SAHƏSİNDƏ TİKİNTİSİ NƏZƏRDƏ TUTULAN ANBAR VƏ İNZİBATİ BİNASI

## Konstruksiya hissəsi
## (İnzibati bina)

Direktor: A. Cahangiroğlu

L.B.M.: G. Musayeva

Bakı-2026

## Konstruksiya hissələrinin əsas cizgiləri

| Vərəq | Adı | Qeyd |
|---|---|---|
| | Dəmir beton konstruksiya cizgilərinin siyahisi | Dk-Mk |
| 1 | Ümumi verilənlər | Dk |
| 2 | Çalanın yerləşmə planı | Dk |
| 3 | Kəsik A-A | Dk |
| 4 | Kəsik B-B | Dk |
| 5 | Lentvari monolit d/b bünövrənin yerləşmə planı | Dk |
| 6 | Lentvari monolit d/b bünövrənin alt armaturlarının yerləşmə planı | Dk |
| 7 | Lentvari monolit d/b bünövrənin üst armaturlarının yerləşmə planı | Dk |
| 8 | Lentvari monolit d/b bünövrənin material sərfi | Dk |
| 9 | "±0.00" Səviyyəsində monolit d/b döşəmə və kəmər "Mk-1"-in yerləşmə planı | Dk |
| 10 | "±0.00" Səviyyəsində monolit d/b döşəmə və kəmər "Mk-1"-in konstruksiyasi | Dk |
| 11 | "-0.80" Səviyyəsində monolit d/b sütunların yerləşmə planı | Dk |
| 12 | Monolit d/b sütun "Ms-1"-in konstruksiyası. | Dk |
| 13 | "+3.30" Səviyyəsində monolit d/b rigellərin yerləşmə planı | Dk |
| 14 | Monolit d/b rigel "Mr-1"-in konstruksiyası | Dk |
| 15 | Monolit d/b rigel "Mr-2"-nin konstruksiyası | Dk |
| 16 | "+3.30" Səviyyəsində monolit d/b örtüyün yerləşmə planı | Dk |
| 17 | "+3.30" Səviyyəsində monolit d/b örtüyün alt torunun armaturlanması | Dk |
| 18 | "+3.30" Səviyyəsində monolit d/b örtüyün üst torunun armaturlanması | Dk |
| 19 | "+3.30" Səviyyəsində monolit d/b örtük üçün material təsnifatı | Dk |
| 20 | Damda çatı elementlərinin yerləşmə planı | Dk |
| 21 | Kəsik "1" | Dk |
| 22 | Damda çatı elementlərinin material sərfi | Dk |

## Ümumi məlumatlar :

1. Binanın konstruksiya hissəsinin cizgiləri baş plan və memarlıq hissəsinin layihəsinə əsasən yerinə yetirilmişdir.
2. Binanın konstruktiv sxemi çərçivəli sxem qəbul edilmişdir. Bünövrə , sütunlar , rigeller dəmir-beton. Binanın örtüyü isə metal fermalardan qəbul edilmişdir
3. Şərti olaraq "±0.000" səviyyəsi 1-ci mərtəbənin təmiz döşəmə səviyyəsinə uyğun olaraq götürülmüşdür. "±0.000 = 133.30"
4. İstehsalat işləri yerinə yetirilərkən "SNİP III - 4 - 80", "SNİP 3.02.01 - 87", "SNİP 3.03.01 - 87", "SNİP 3.04.01 - 87" və "SNİP 3.04.03 - 85" tikinti normaları tələblərinə riayət olunmuşdur.
5. Bünövrə əsasını bərk konsistensiyalı gilcə qruntu təşkil edir.

| | |
|---|---|
| Şərti hesabi təzyiq | $R_0$= 2.40 kqq/sm$^2$ |
| İlişmə qüvvəsi | $c^n$= 0.21 kqq/sm$^2$ |
| Daxili sürtünmə bucağı | $\varphi$= 22°30' |
| Deformasiya modulu (təbii) | E = 175.10 kqq/sm$^2$ |
| Həcm çəkisi - təbii | $\gamma$= 1.76 q/sm$^3$ |

6. Qruntun aqressivlik xassələri "SNİP 2.03.11 - 85"-ə sasən dəmir-beton konstruksiyalara qarşı orta aqressiv olduğu üçün torpaqla təmasda olan bütün dəmir-beton konstruksiyaların hazırlanması zamanı sulfatadavamlı portlandsementdən istifadə etmək lazımdır.
7. Bünövrənin oturduğu qrunt M.G.E-1 olduğundan qruntun kateqoriyası II sinfə aiddir.
8. Bünövrənin altında 10 sm qalınlığında beton hazırlıq qatı verilməlidir

## Layihənin tətbiqi şəraiti:

| | | |
|---|---|---|
| Tikinti rayonunun seysmikliyi | -- | 8 ball Az. DTN 2.3-1 |
| Havanın xarici hesabi temperaturu | -- | -4° |
| İqlim şəraiti rayonu | -- | IV B |
| Qar örtüyü | -- | 80,0 kq /m² |
| Külək örtüyü | -- | 73,0 kq/m² |

9. Sahədə qazılmış quyularda yeraltı qrunt suların aşkar edilməmişdir.

Razılaşdırılmışdır

İnvent № Əvəzinə

İmza və Tarix

İnvent № İmza

İşlənmiş cizgilər fəaliyyətdə olan norma və qaydalara uyğun gəlir və bina , tikili və qurğuların istismarı zamanı partlayış və yanğından mühafizəni təmin edən tədbirləri nəzərdə tutur.

Layihənin baş mühəndisi Musayeva G.

| Dəyiş | Sh.sən | Vərəq | Sən.№ | İmza | Tarix |
|---|---|---|---|---|---|
| L.B.M. | | G. Musayeva | | | |
| Konstruktor | | M. Əzizov | | | |
| Norm. nəzarət | | S. Şükürova | | | |

Sifarişçi: Cəfərov Mədət İslam oğlu — DK-MK

Abşeron rayonu, Qobu qəsəbəsində yerləşən torpaq sahəsində tikintisi nəzərdə tutulan anbar və inzibati binası anbar binası.

| İnzibati bina | Mərhələ | Vərəq | Vərəqlər |
|---|---|---|---|
| | İ.L. | 1 | |
| Ümumi verilənlər | "STORM BUİLDİNG" MMC | | |

Format A3

# Çalanın yerləşmə planı

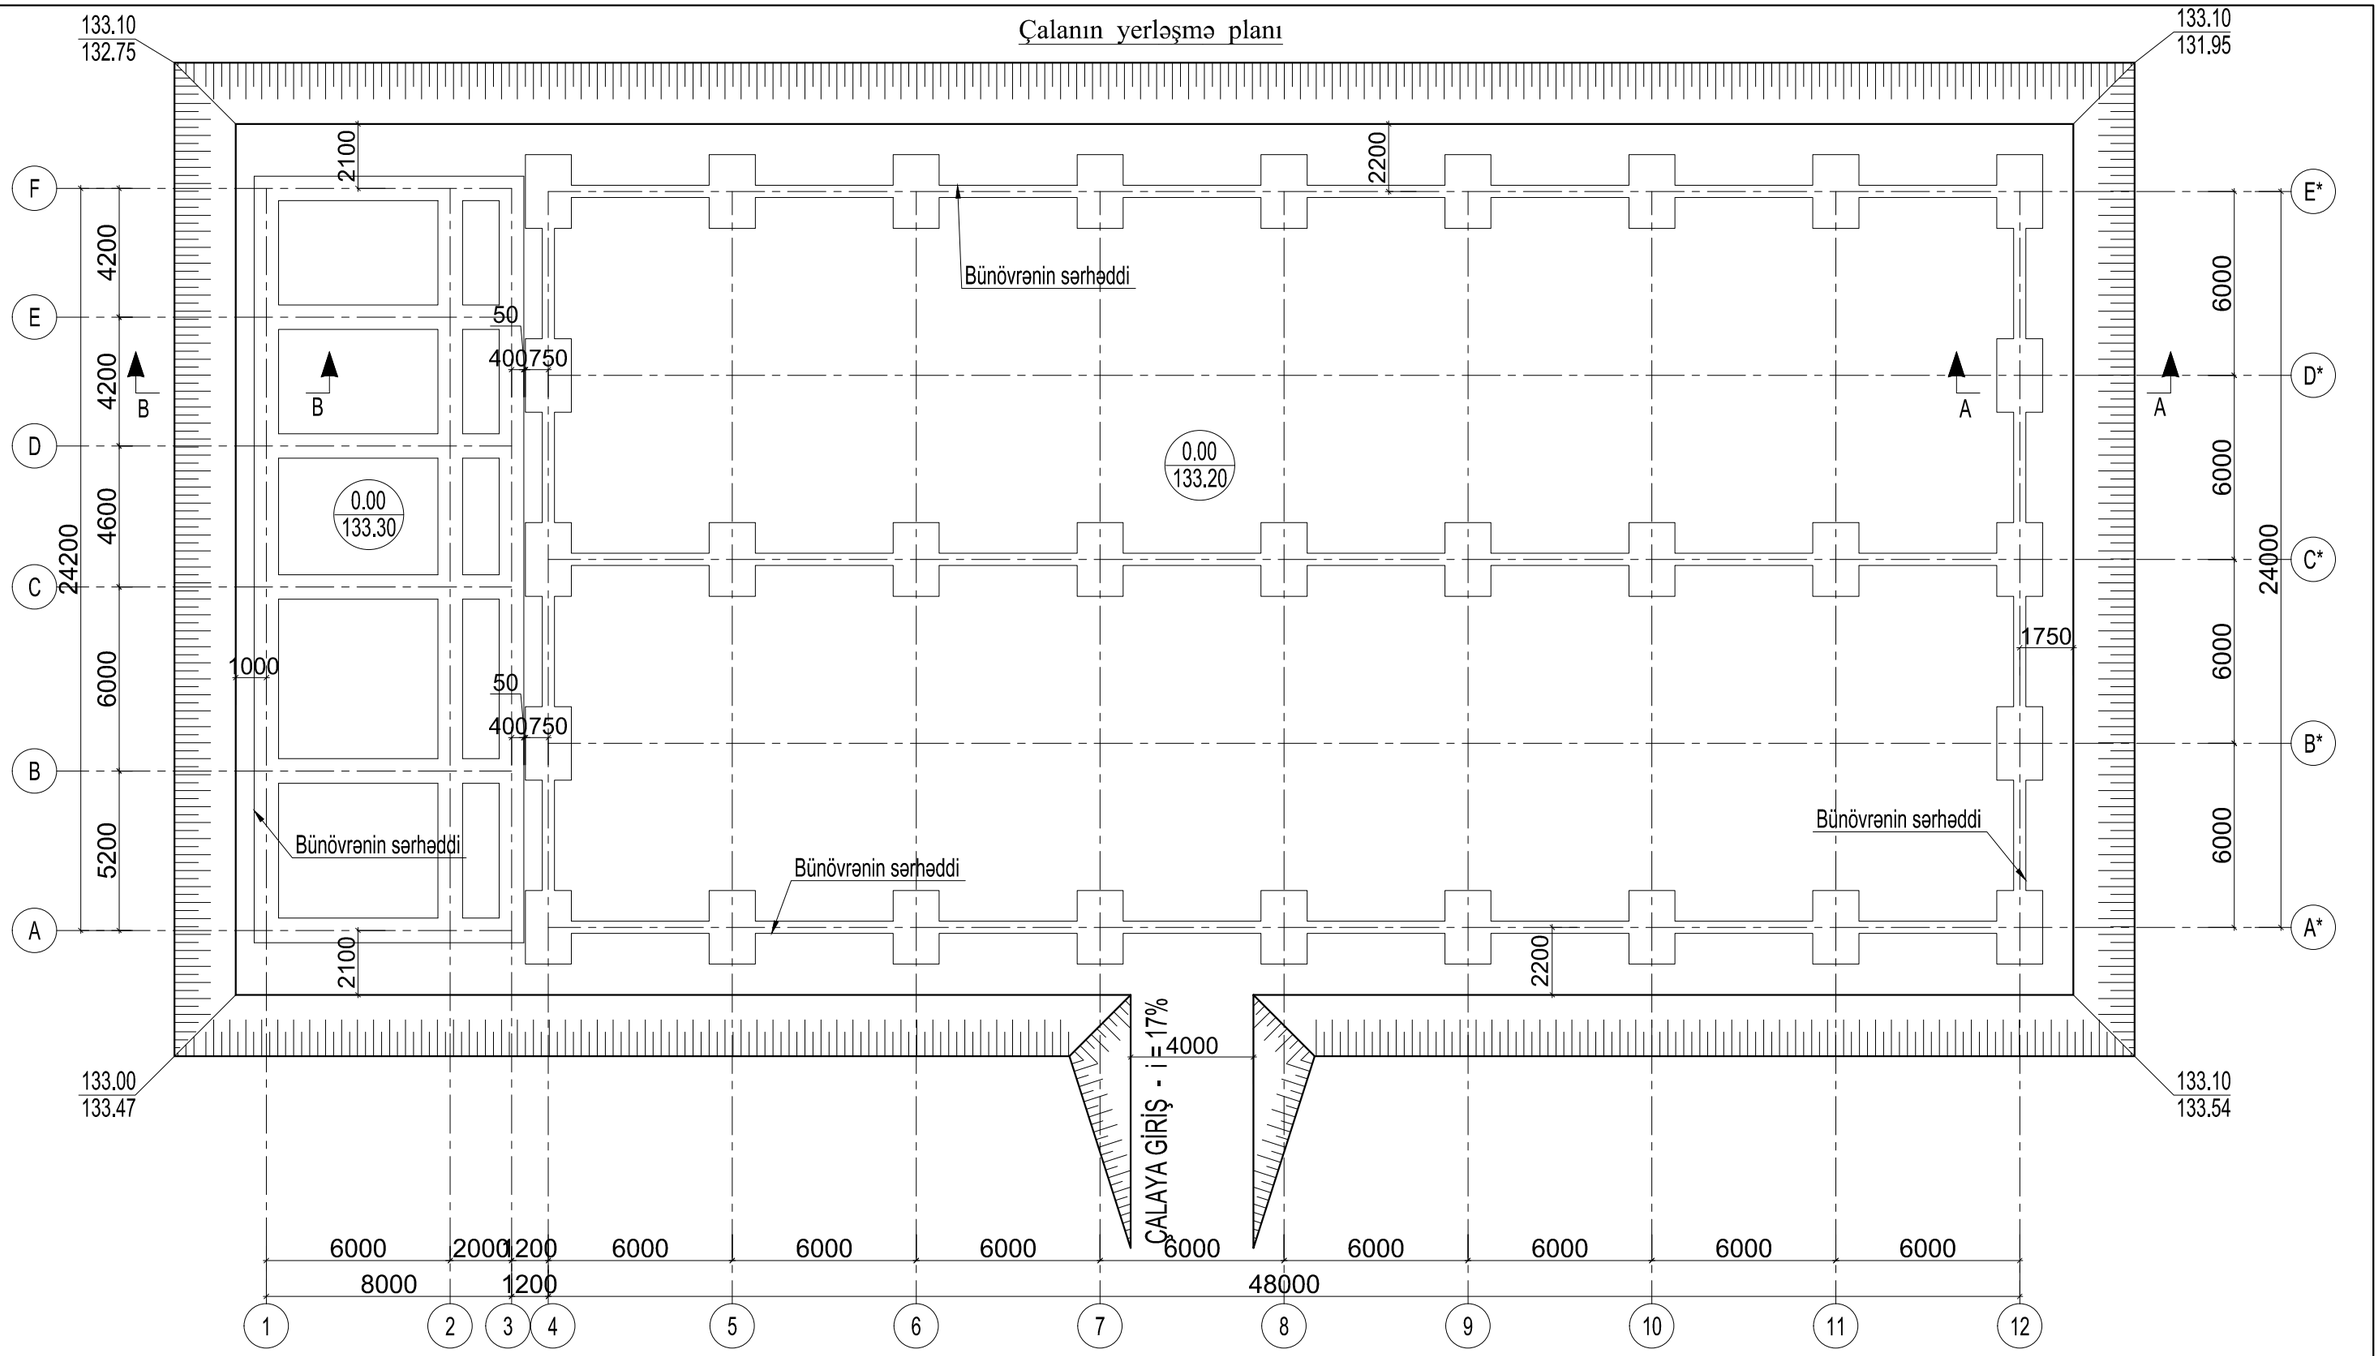


## QEYDLƏR:

1. LAYİHƏ MEMARLIQ CİZGİLƏRİ ƏSASINDA YERİNƏ YETİRİLİB.
2. 0.00 NİSBİ YÜKSƏKLİYİ 1-Cİ MƏRTƏBƏNİN DÖŞƏMƏ SƏVİYYƏSİ KİMİ QƏBUL EDİLİB
3. QRUNT ƏSASININ , GEOLOJİ TƏDQİQATLARIN NƏTİCƏSİNƏ UYĞUNSUZLUĞU OLARSA , ÖZÜL KONSTRUKSİYASI LAYİHƏ İNSTİTUNUN VƏ YA LAYİHƏ FİRMASININ İŞTİRAKI İLƏ YENİDƏN HƏLL EDİLMƏLİDİR.
4. SAHƏNİN SEYSMİKLİYİ 8 BALDIR.
5. ÖZÜL QALINLIĞI 500 mm OLAN MONOLİT D/B BAŞMAQ VƏ QALINLIĞI 400 mm OLAN LENTA ŞƏKLİNDƏ LAYİHƏLƏNDİRİLİB.
6. TİKİNTİ İŞLƏRİNƏ BAŞLAMAZDAN ƏVVƏL ƏLAQƏDAR TƏŞKİLATLARIN VƏ SİFARİŞÇİNİN İŞTİRAKI İLƏ TORPAQ İŞLƏRİNİN APARILMASINA İCAZƏ VERƏN MÜƏYYƏN AKT TƏRTİB EDİLMƏLİDİR.
7. KATLAVANIN DİBİ QAZILARAQ LAYİHƏ SƏVİYYƏSİNƏ ÇATDIRILDIQDAN SONRA KATLAVANIN İÇİNDƏ HƏR 4-5 M-DƏN BİR DƏRİNLİYİ 3 M, DİAMETRİ 150-200 MM OLAN QUYULAR QAZILMALIDIR. SONRADAN KATLAVANIN DİB SƏVİYYƏSİNDƏN 30 SM YUXARI ÇIXMAQ ŞƏRTİ İLƏ SU İLƏ DOLDURULMALIDIR. DOLDURULAN SU QRUNTA HOPDUQDAN SONRA KATLAVAN DİBİNDƏ YARANMIŞ PALÇIQ (STRULTURUNU İTİRMİŞ GİL), LİLLİ PALÇIQ KATLAVANDAN TƏMİZLƏNMƏLİDİR. ÜMUMİLİKDƏ BU PROSES 2 DƏFƏ GÖRÜLMƏLİDİR. KATLAVANIN DİBİ LAYİHƏ SƏVİYYƏSİNƏ ÇATDIRILMAQ ÜÇÜN QIRMADAŞ VƏ ŞİŞMƏYƏN GİL QARIŞIĞI (70 / 30 NİSBƏTİNDƏ) İLƏ HƏR 200 MM-DƏN BİR KİPLƏŞDİRİLƏRƏK YAYILMALIDIR.

| Dəyiş | Sh.sən | Vərəq | Sən.№ | İmza | Tarix |
|---|---|---|---|---|---|
| L.B.M. | | G. Musayeva | | | |
| Konstruktor | | M. Əzizov | | | |
| Norm. nəzarət | | S. Şükürova | | | |

Sifarişçi: Cəfərov Mədət İslam oğlu — DK-MK

Abşeron rayonu, Qobu qəsəbəsində yerləşən torpaq sahəsində tikintisi nəzərdə tutulan anbar və inzibati binası anbar binası.

| İnzibati bina | Mərhələ | Vərəq | Vərəqlər |
|---|---|---|---|
| | İ.L. | 2 | |

Çalanın yerləşmə planı — "STORM BUİLDİNG" MMC

Razılaşdırılmışdır

İnvent № Əvəzinə | İmza və Tarix | İnvent № İmza

Format A3

# Kəsik A-A

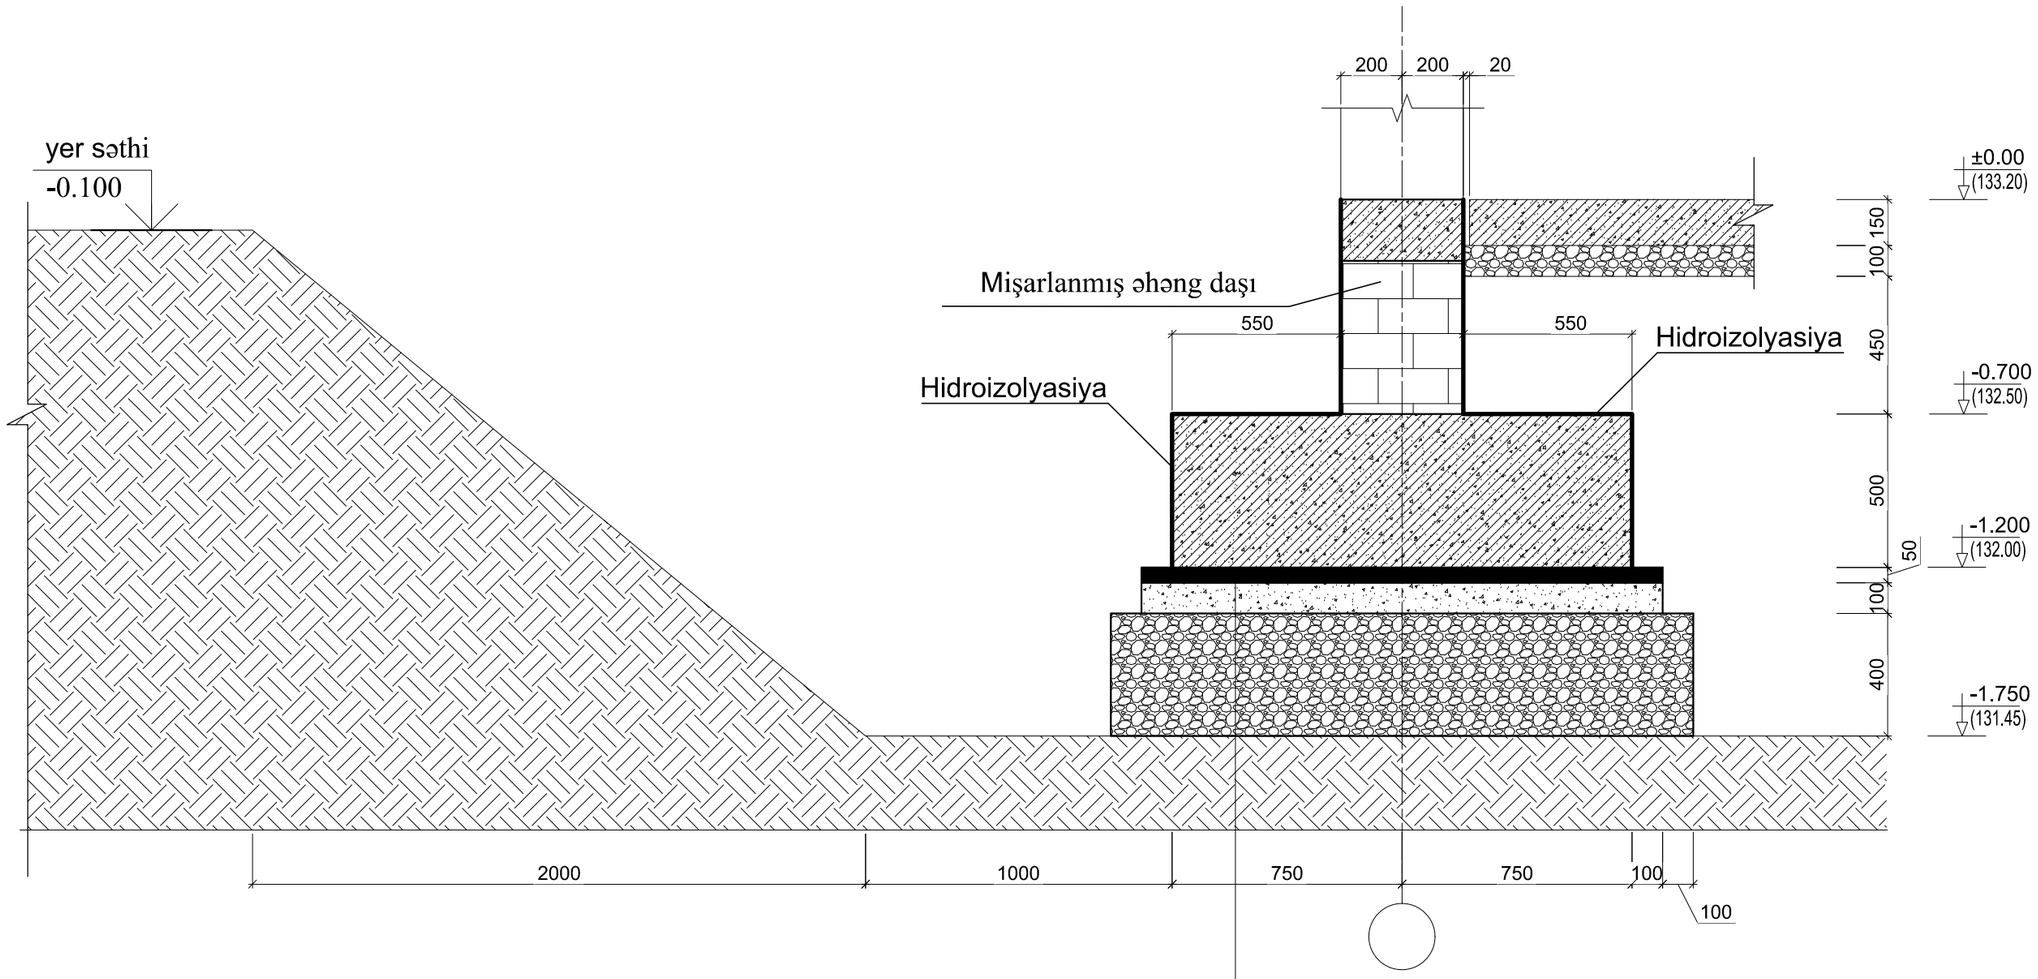


Monolit d/b bünövrə (Başmaq tipli). h=500 mm

Sementdən mühafizə qatı. h=50mm

Hidroizolyasiya 2 qat ruberoid yapışdırma yolu ilə.

Beton hazıqlıq qatı betonun sinfi B7.5 h=100mm

Qrunta toxaclanmış çaqıl-çınqıl qatı. h=400 mm

Kipləşdirilmiş qrunt.

**Qeyd :** 1. Bu vərəq "DK - 2 " vərəqi ilə birgə oxunmalıdır.

| Dəyiş | Sh.sən | Vərəq | Sən.№ | İmza | Tarix |
|---|---|---|---|---|---|
| L.B.M. | | G. Musayeva | | | |
| Konstruktor | | M. Əzizov | | | |
| Norm. nəzarət | | S. Şükürova | | | |

Sifarişçi: Cəfərov Mədət İslam oğlu — DK-MK

Abşeron rayonu, Qobu qəsəbəsində yerləşən torpaq sahəsində tikintisi nəzərdə tutulan anbar və inzibati binası anbar binası.

| İnzibati bina | Mərhələ | Vərəq | Vərəqlər |
|---|---|---|---|
| | İ.L. | 3 | |

Kəsik A-A — "STORM BUİLDİNG" MMC

Razılaşdırılmışdır

İnvent № Əvəzinə

İmza və Tarix

İnvent № İmza

Format A3

# Kəsik B-B

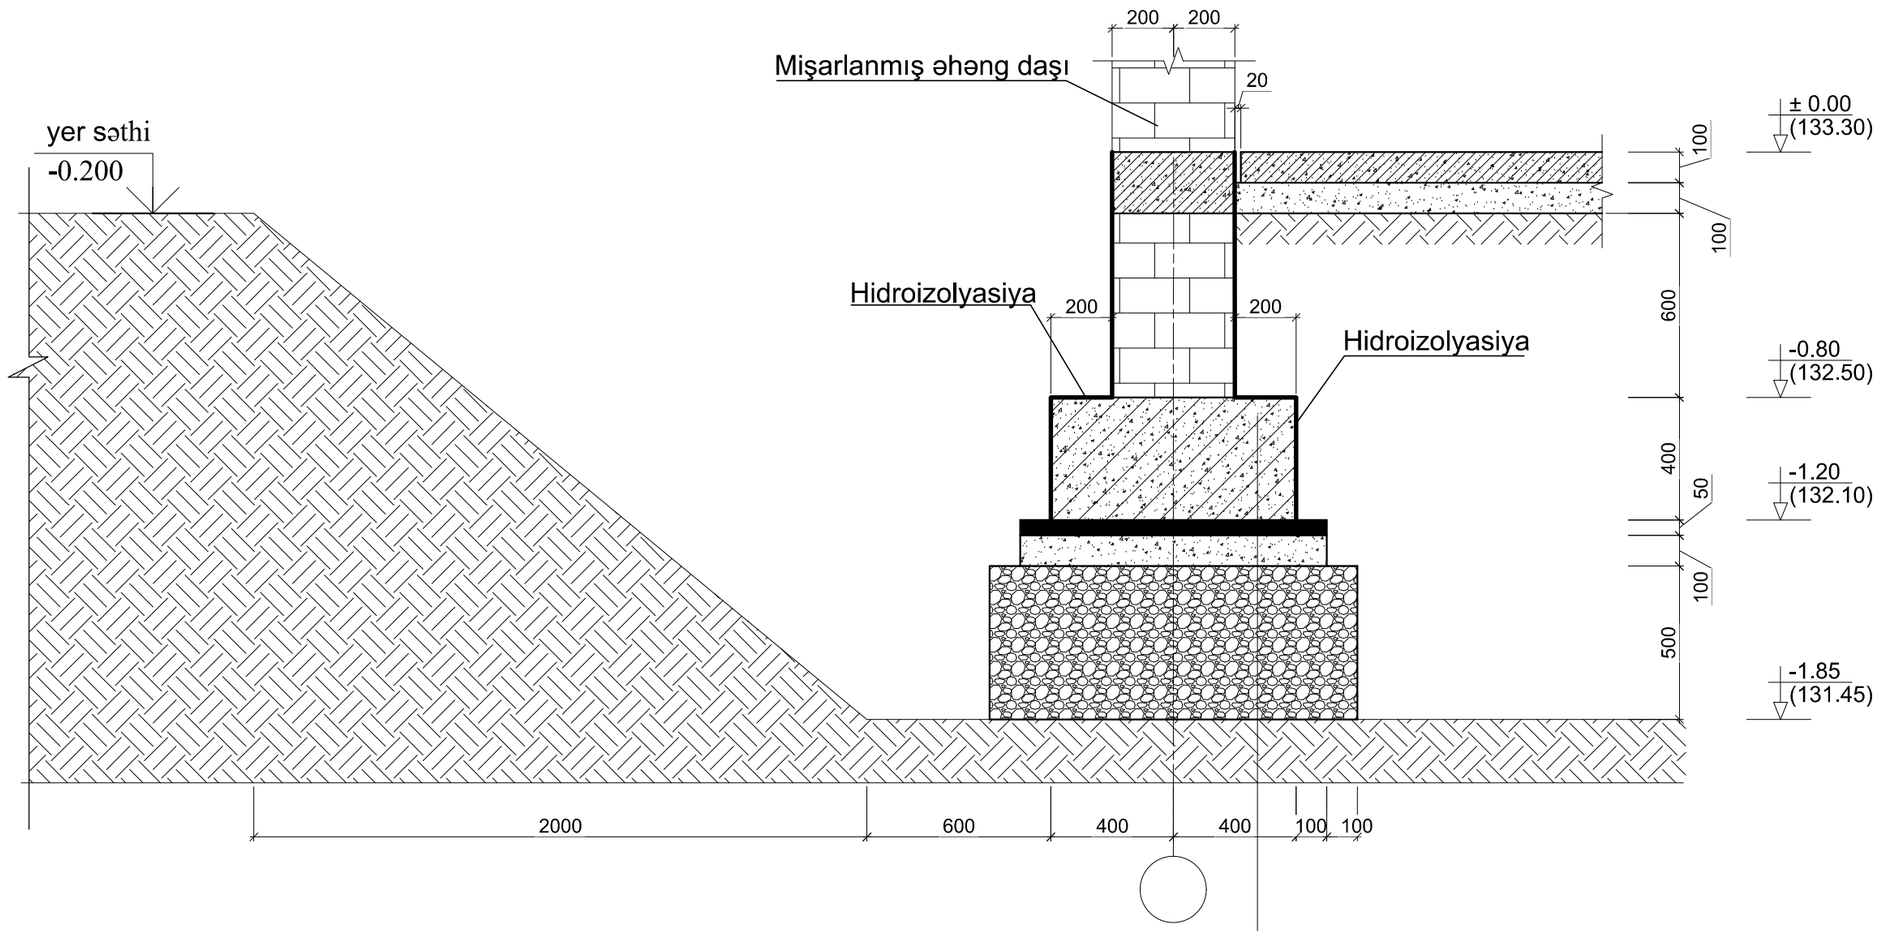


Monolit d/b bünövrə (Lentvari). h=400 mm

Sementdən mühafizə qatı. h=50mm

Hidroizolyasiya 2 qat ruberoid yapışdırma yolu ilə.

Beton hazıqlıq qatı betonun sinfi B7.5 h=100mm

Qrunta toxaclanmış çaqıl-çınqıl qatı. h=500 mm

Kipləşdirilmiş qrunt.

**Qeyd :** 1. Bu vərəq "DK - 2 " vərəqi ilə birgə oxunmalıdır.

| Dəyiş | Sh.sən | Vərəq | Sən.№ | İmza | Tarix |
|---|---|---|---|---|---|
| L.B.M. | | G. Musayeva | | | |
| Konstruktor | | M. Əzizov | | | |
| Norm. nəzarət | | S. Şükürova | | | |

Sifarişçi: Cəfərov Mədət İslam oğlu — DK-MK

Abşeron rayonu, Qobu qəsəbəsində yerləşən torpaq sahəsində tikintisi nəzərdə tutulan anbar və inzibati binası anbar binası.

| İnzibati bina | Mərhələ | Vərəq | Vərəqlər |
|---|---|---|---|
| | İ.L. | 4 | |

Kəsik B-B — "STORM BUİLDİNG" MMC

Razılaşdırılmışdır

İnvent № Əvəzinə

İmza və Tarix

İnvent № İmza

Format A3

# Lentvari monolit d/b bünövrənin yerləşmə planı

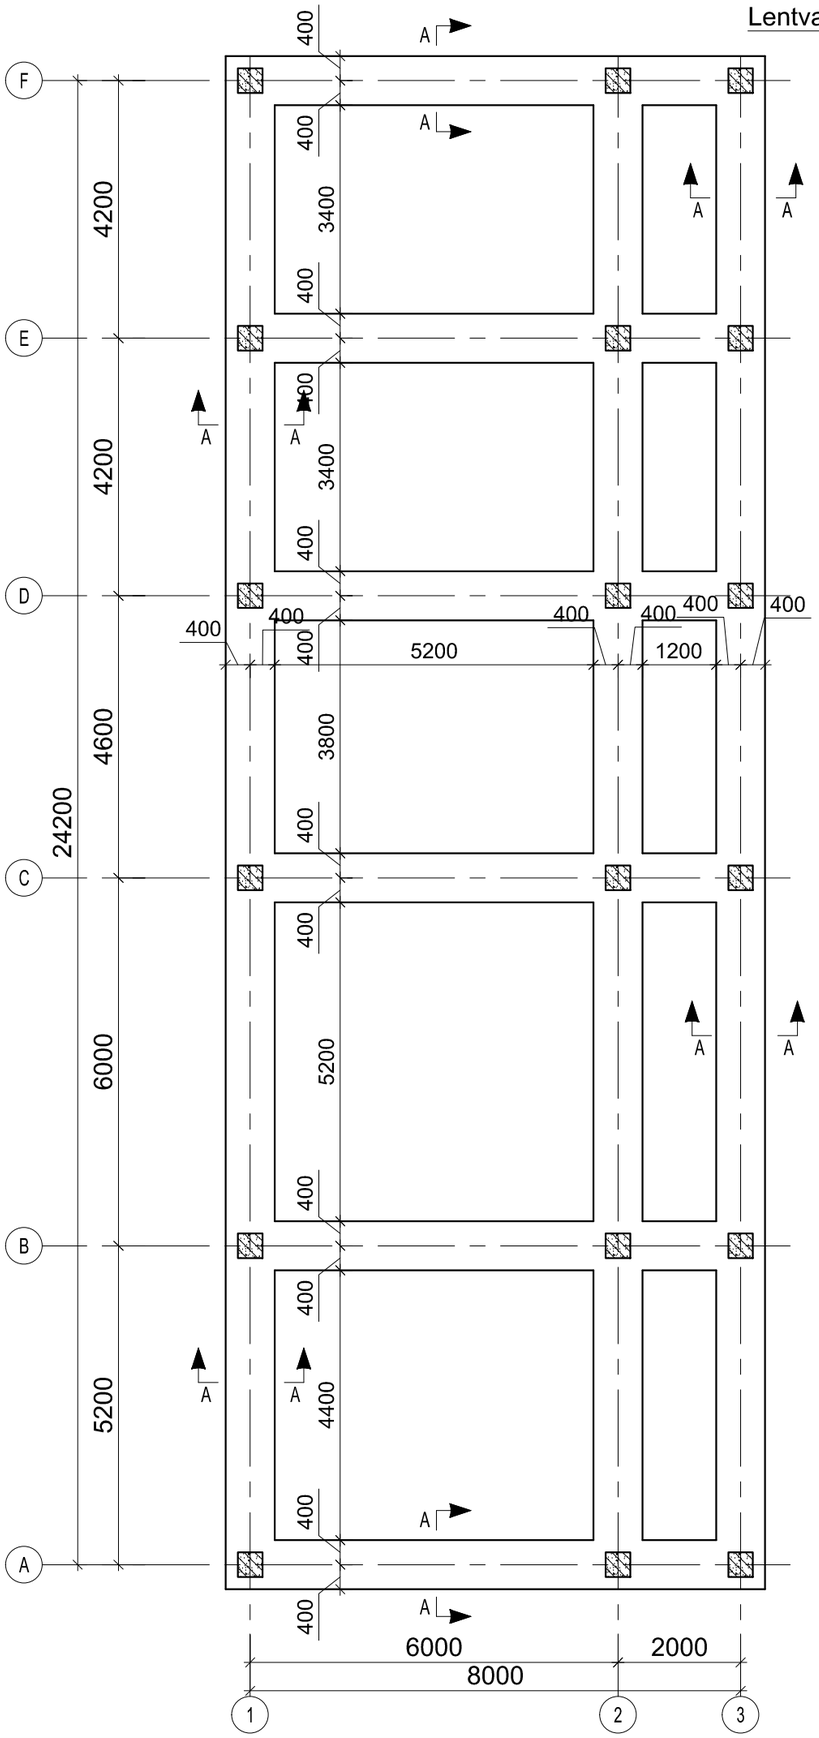


Kəsik A-A

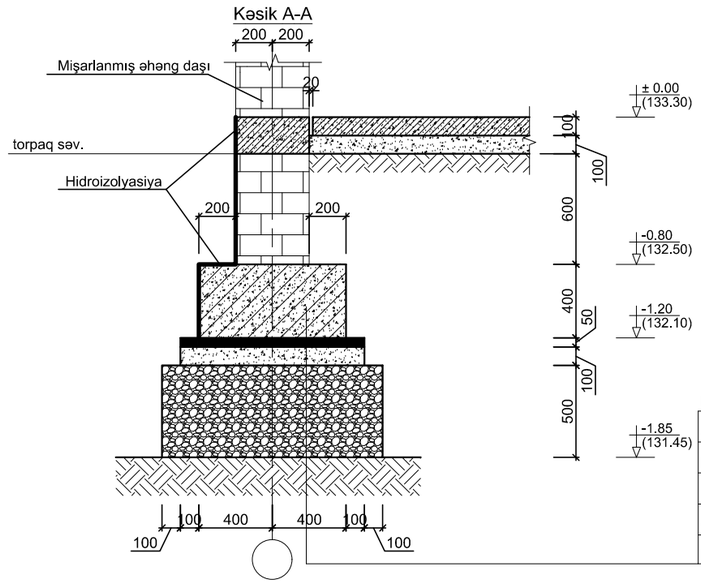


Monolit d/b bünövrə (Lentvari). h=400 mm

Sementdən mühafizə qatı. h=50mm

Hidroizolyasiya 2 qat ruberoid yapışdırma yolu ilə.

Beton hazırlıq qatı betonun sinfi B7.5 h=100mm

Qrunta toxaclanmış çaqıl-çınqıl qatı. h=500 mm

Kipləşdirilmiş qrunt.

| | | | | | | | |
|---|---|---|---|---|---|---|---|
| | | | | | | Sifarişçi: Cəfərov Mədət İslam oğlu | DK-MK |
| Dəyiş | Sh.sən | Vərəq | Sən.№ | İmza | Tarix | Abşeron rayonu, Qobu qəsəbəsində yerləşən torpaq sahəsində tikintisi nəzərdə tutulan anbar və inzibati binası anbar binası. | |
| L.B.M. | | G. Musayeva | | | | İnzibati bina | Mərhələ: İ.L. / Vərəq: 5 / Vərəqlər |
| Konstruktor | | M. Əzizov | | | | | |
| Norm. nəzarət | | S. Şükürova | | | | Lentvari monolit d/b bünövrənin yerləşmə planı | "STORM BUİLDİNG" MMC |

Format A3

Razılaşdırılmışdır

İnvent № Əvəzinə

İmza və Tarix

İnvent №

İmza

Lentvari monolit d/b bünövrənin alt armaturlarının yerləşmə planı

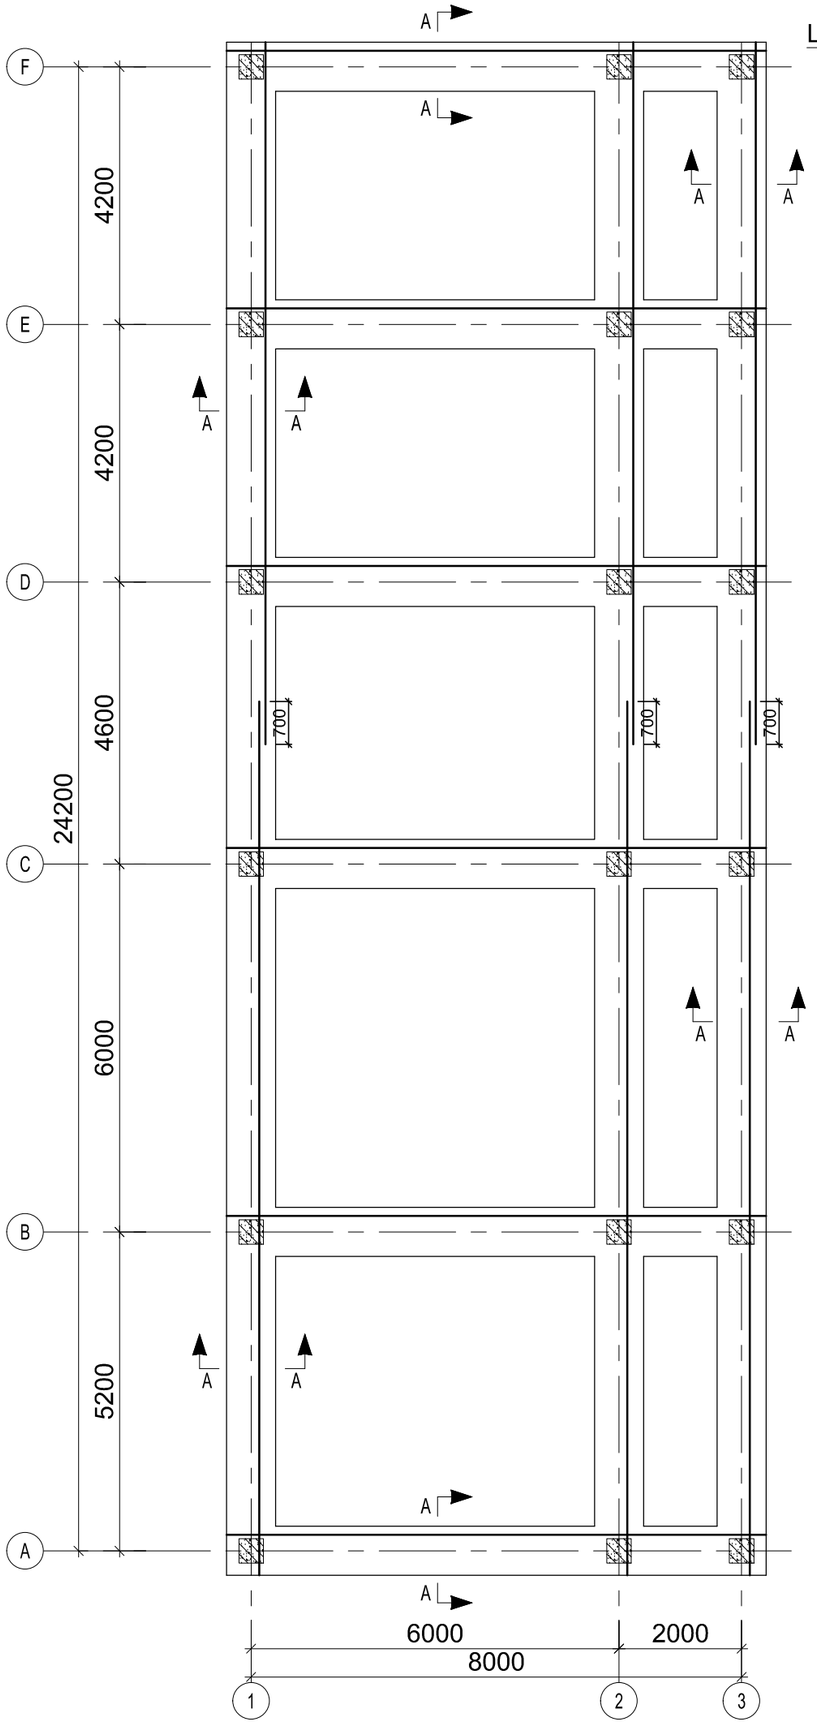


KƏSİK A

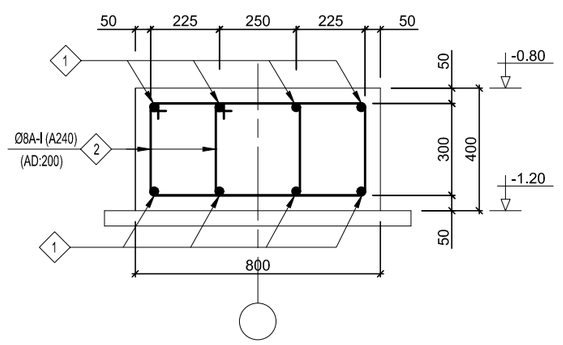


Armaturların calaq düyünü

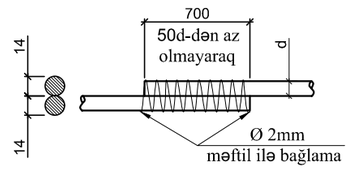


| | | | | | | | |
|---|---|---|---|---|---|---|---|
| | | | | | | Sifarişçi: Cəfərov Mədət İslam oğlu | DK-MK |
| Dəyiş | Sh.sən | Vərəq | Sən.№ | İmza | Tarix | Abşeron rayonu, Qobu qəsəbəsində yerləşən torpaq sahəsində tikintisi nəzərdə tutulan anbar və inzibati binası anbar binası. | |
| L.B.M. | | G. Musayeva | | | | İnzibati bina | Mərhələ: İ.L. / Vərəq: 6 / Vərəqlər |
| Konstruktor | | M. Əzizov | | | | | |
| Norm. nəzarət | | S. Şükürova | | | | Lentvari monolit d/b bünövrənin alt armaturlarının yerləşmə planı | "STORM BUİLDİNG" MMC |

Razılaşdırılmışdır

İnvent № Əvəzinə

İmza və Tarix

İnvent № İmza

Format A3

Lentvari monolit d/b bünövrənin üst armaturlarının yerləşmə planı

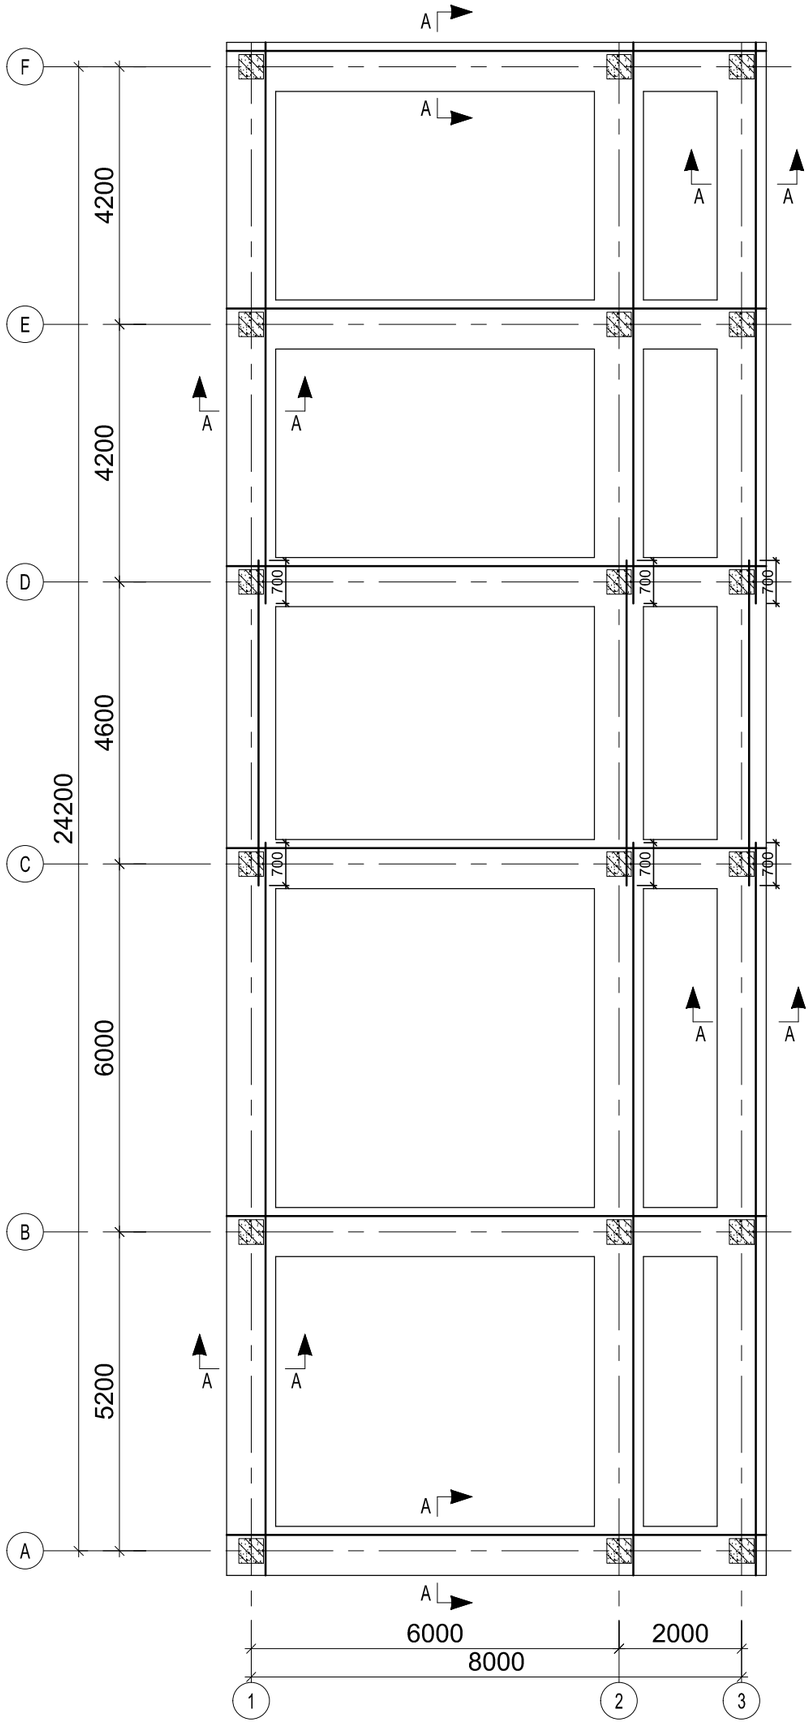


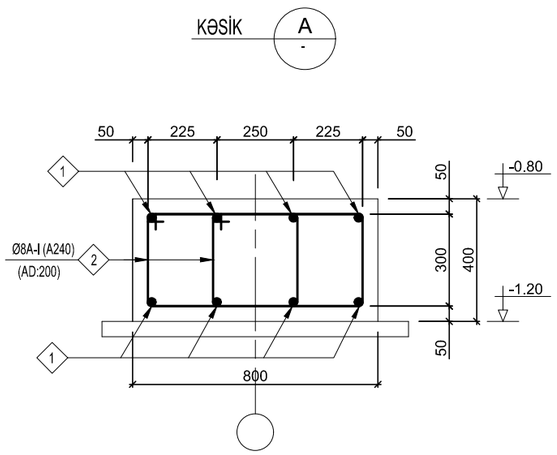


Armaturların calaq düyünü

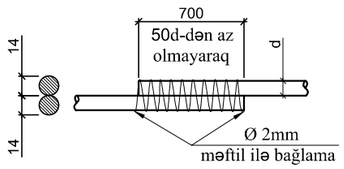


| | | | | | | | |
|---|---|---|---|---|---|---|---|
| | | | | | | Sifarişçi: Cəfərov Mədət İslam oğlu | DK-MK |
| Dəyiş | Sh.sən | Vərəq | Sən.№ | İmza | Tarix | Abşeron rayonu, Qobu qəsəbəsində yerləşən torpaq sahəsində tikintisi nəzərdə tutulan anbar və inzibati binası anbar binası. | |
| L.B.M. | | G. Musayeva | | | | İnzibati bina | Mərhələ: İ.L. / Vərəq: 7 / Vərəqlər: |
| Konstruktor | | M. Əzizov | | | | | |
| Norm. nəzarət | | S. Şükürova | | | | Lentvari monolit d/b bünövrənin üst armaturlarının yerləşmə planı | "STORM BUİLDİNG" MMC |

Format A3

Razılaşdırılmışdır

İnvent № Əvəzinə

İmza və Tarix

İnvent № İmza

## MONOLİT D/B ELEMENTLƏRİN TƏSNİFATI.

| FORMAT | ZONA | MÖVQE | MƏNBƏYİ | ADI | SAYI: ƏD. | QEYD |
|---|---|---|---|---|---|---|
| | | | | Monolit d/b lentvari bünövrə | | |
| | | 1 | DÜİST 52544-2006 | Ø14 A500C , L=866.0 p.m | - | - / 1046.2 |
| | | 2 | DÜİST 5781-82* | Ø8A-I (A240), L=1860 mm | 1030 | 0.7 / 721.0 |
| | | | | Beton B25 | - | 33.0 M³ |

## DETALLAR CƏDVƏLİ

| MÖVQE | ESKİZ |
|---|---|
| 2 |   |

## POLAD SƏRFİ CƏDVƏLİ , Kq.

| ELEMENTİN MARKASI | ARMATUR MƏMULATLARI | | | | | | | | |
|---|---|---|---|---|---|---|---|---|---|
| | ARMATURUN SİNFİ | | | | | | | | ÜMUMİ SƏRF |
| | A-I (A240) | | | A500C | | | | | |
| | DÜİST 5781-82* | | | DÜİST 52544-2006 | | | | | |
| | Ø6 | Ø8 | CƏMİ: | Ø14 | Ø16 | Ø20 | Ø22 | CƏMİ: | |
| LENTVARİ MONOLİT D/B ÖZÜL | - | 721.0 | 721.0 | 1046.2 | - | - | - | 1046.2 | 1767.20 |

## QEYD:

1. Əsas qeydlərə "dk-2" vərəqində baxılmalı

| | | | | | | | |
|---|---|---|---|---|---|---|---|
| | | | | | | Sifarişçi: Cəfərov Mədət İslam oğlu | DK-MK |
| Dəyiş | Sh.sən | Vərəq | Sən.№ | İmza | Tarix | Abşeron rayonu, Qobu qəsəbəsində yerləşən torpaq sahəsində tikintisi nəzərdə tutulan anbar və inzibati binası anbar binası. | |
| L.B.M. | | G. Musayeva | | | | İnzibati bina | Mərhələ: İ.L. / Vərəq: 8 / Vərəqlər |
| Konstruktor | | M. Əzizov | | | | | |
| Norm. nəzarət | | S. Şükürova | | | | Lentvari monolit d/b bünövrənin material sərfi | "STORM BUİLDİNG" MMC |

Razılaşdırılmışdır

İnvent № | İmza | İmza və Tarix | İnvent № əvəzinə

Format A3

±0.00 səviyyəsində monolit d\b döşəmə və kəmərin yerləşmə planı.

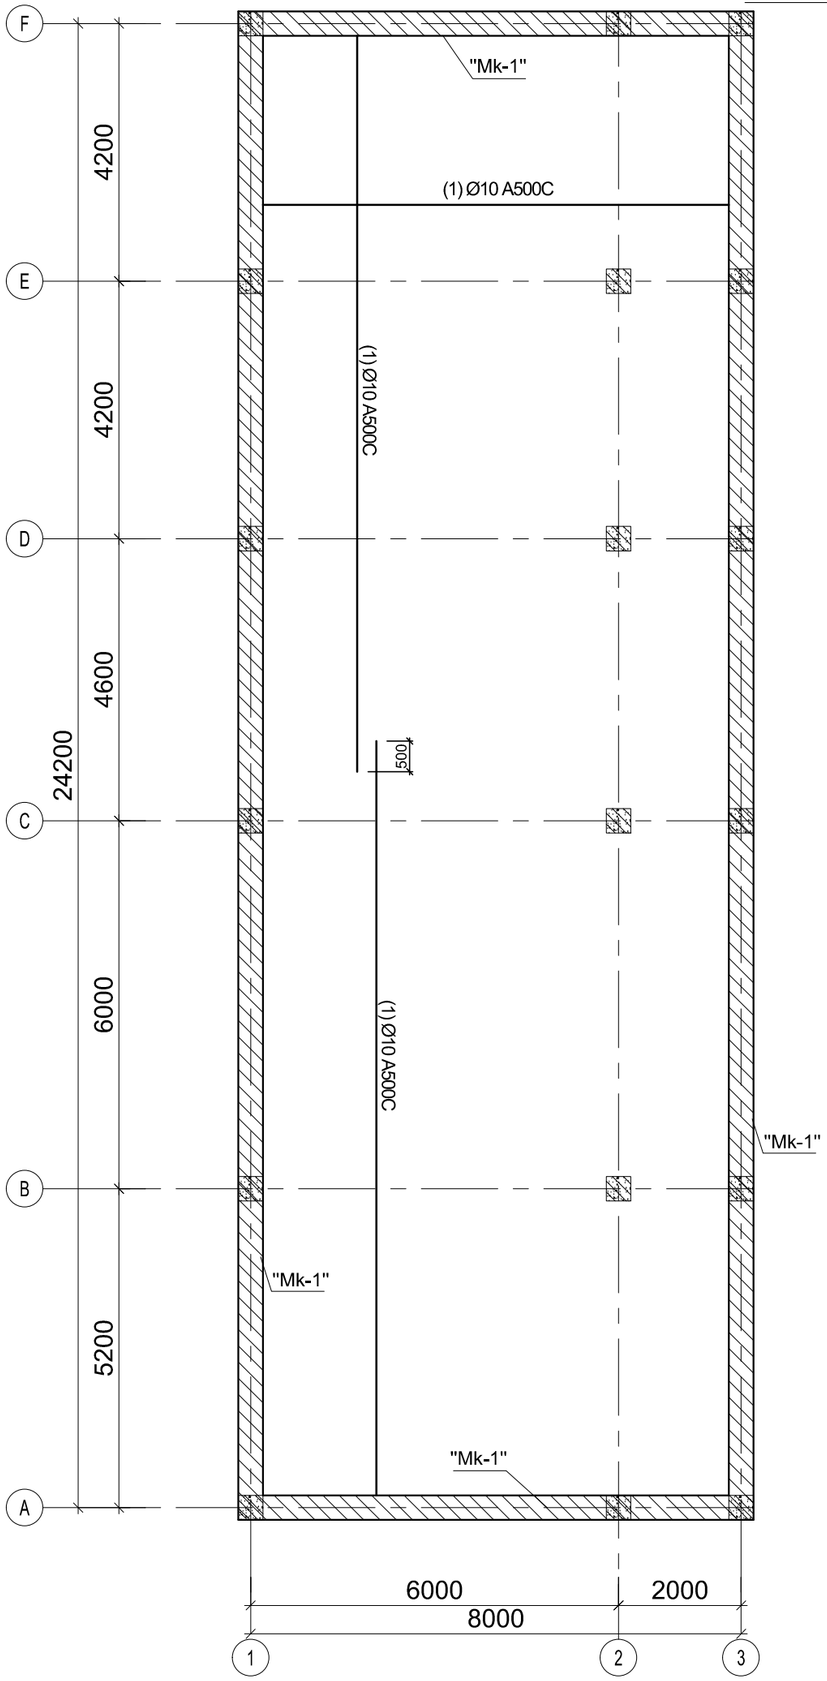


Qeyd :
Monolit d/b kəmər ştrixlənmiş sahə ilə göstərilmişdir.

| | | | | | | | |
|---|---|---|---|---|---|---|---|
| | | | | | | Sifarişçi: Cəfərov Mədət İslam oğlu | DK-MK |
| Dəyiş | Sh.sən | Vərəq | Sən.№ | İmza | Tarix | Abşeron rayonu, Qobu qəsəbəsində yerləşən torpaq sahəsində tikintisi nəzərdə tutulan anbar və inzibati binası anbar binası. | |
| L.B.M. | | G. Musayeva | | | | İnzibati bina | Mərhələ: İ.L. / Vərəq: 9 / Vərəqlər: |
| Konstruktor | | M. Əzizov | | | | | |
| Norm. nəzarət | | S. Şükürova | | | | ±0.00 səviyyəsində monolit d\b döşəmə və kəmərin yerləşmə planı. | "STORM BUİLDİNG" MMC |

Format A3

Razılaşdırılmışdır

İnvent № Əvəzinə

İmza və Tarix

İnvent № İmza

# "±0.00" Səviyyəsində monolit d/b döşəmə və kəmərin konstruksiyasi

## Monolit d\b döşəmənin armaturlanma kəsiyi
Kəsik: A-A

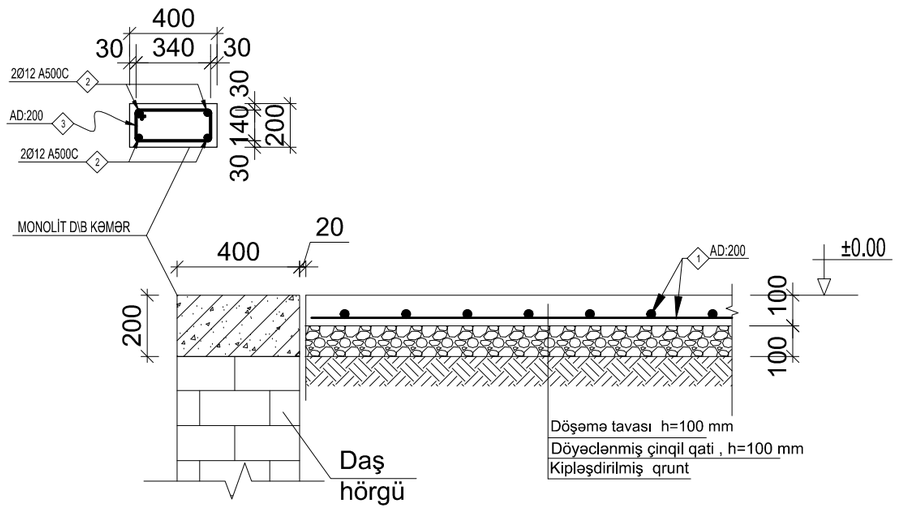


## MATERİALLARIN TƏSNİFATI.

| FORMAT | ZONA | MÖVQE | İŞARƏ | ADI | MİQDARI | QEYD |
|---|---|---|---|---|---|---|
| | | | | D/B DÖŞƏMƏ TAVASI | | |
| | | 1 | DÜİST 52544-2006 | Ø10 A500C , L=1900.0 p.m | - | - / 1172.3 |
| | | | | | | |
| | | | | BETON B15 | - | 18.1 m³ |
| | | | | MONOLİT D/B KƏMƏR - Mk1 | | |
| | | 2 | DÜİST 52544-2006 | Ø12 A500C , L=290.4 pm. | - | - / 257.9 |
| | | 3 | DÜİST 5781-82* | Ø8 A-I (A240), L=1120 mm | 330 | 0.44 / 145.2 |
| | | | | BETON B25 | - | 5.3 m³ |

## DETALLAR CƏDVƏLİ.

| MÖVQE | CİZGİ |
|---|---|
| 3 | 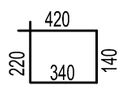 |



DÜYÜN I -

## ARMATURLARIN CALAQ FRAQMENTİ

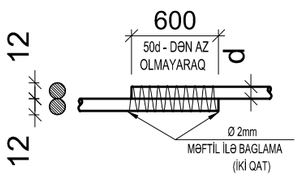


## POLAD SƏRFİ CƏDVƏLİ , Kq.

| ELEMENTİN MARKASI | ARMATUR MƏMULATLARI | | | | | | | | | |
|---|---|---|---|---|---|---|---|---|---|---|
| | ARMATURUN SİNFİ | | | | | | | | | ÜMUMİ SƏRF |
| | A-I (A240) | | | A500C | | | | | | |
| | DÜİST 5781-82* | | | ГОСТ 52544-2006 | | | | | | |
| | Ø8 | Ø10 | CƏMİ: | Ø10 | Ø12 | Ø16 | Ø22 | Ø25 | CƏMİ: | |
| D/B DÖŞƏMƏ TAVASI | - | - | - | 1172.3 | - | - | - | - | 1172.3 | 1172.3 |
| MONOLİT D/B KƏMƏR - Mk1 | 145.2 | - | 145.2 | - | 257.9 | - | - | - | 257.9 | 403.1 |

| Dəyiş | Sh.sən | Vərəq | Sən.№ | İmza | Tarix |
|---|---|---|---|---|---|
| L.B.M. | | G. Musayeva | | | |
| Konstruktor | | M. Əzizov | | | |
| Norm. nəzarət | | S. Şükürova | | | |

Sifarişçi: Cəfərov Mədət İslam oğlu — DK-MK

Abşeron rayonu, Qobu qəsəbəsində yerləşən torpaq sahəsində tikintisi nəzərdə tutulan anbar və inzibati binası anbar binası.

| İnzibati bina | Mərhələ | Vərəq | Vərəqlər |
|---|---|---|---|
| | İ.L. | 10 | |

"±0.00" Səviyyəsində monolit d/b döşəmə və kəmər "Mk-1"-in konstruksiyasi

"STORM BUİLDİNG" MMC

Razılaşdırılmışdır

İnvent № | İmza | İmza və Tarix | İnvent № Əvəzinə

Format A3

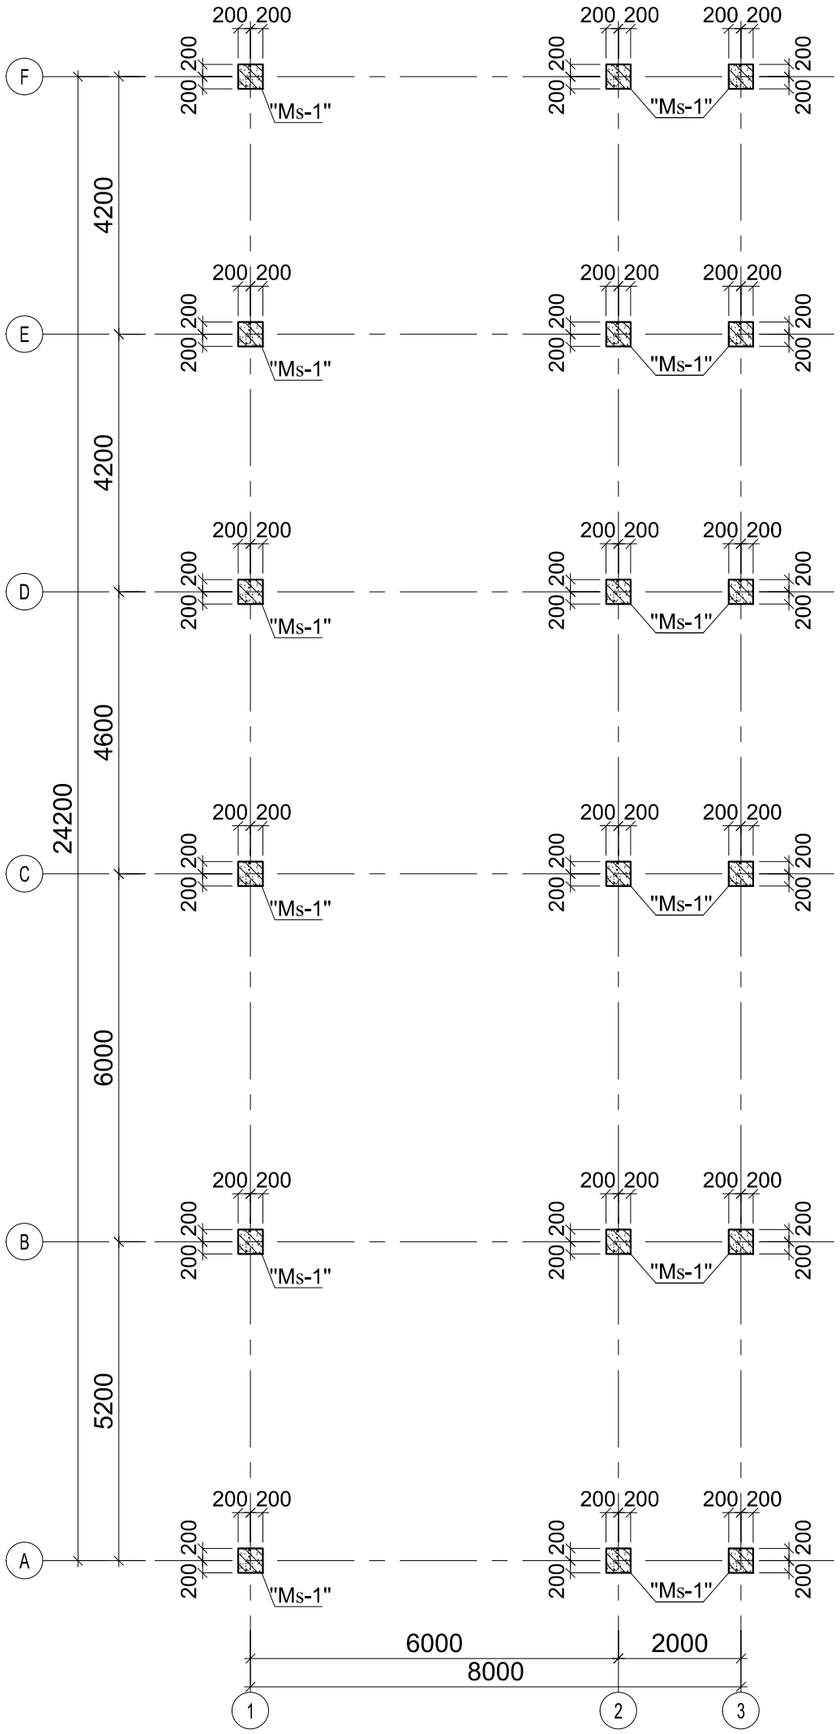


-0.80 səviyyəsində sütunların yerləşmə planı.

Monolit d/b elementlərin təsnifatı

| Format | Zona | Mövqe | İşarə | Adı | Miqdarı | Qeyd |
|---|---|---|---|---|---|---|
| | | | | Monolit d/b sütunlar | | |
| | | 1 | | Monolit d/b sütun Ms-1 | 18 | |
| | | | | | | |
| | | | | | | |
| | | | | | | |

| | | | | | | | |
|---|---|---|---|---|---|---|---|
| | | | | | | Sifarişçi: Cəfərov Mədət İslam oğlu | DK-MK |
| Dəyiş | Sh.sən | Vərəq | Sən.№ | İmza | Tarix | Abşeron rayonu, Qobu qəsəbəsində yerləşən torpaq sahəsində tikintisi nəzərdə tutulan anbar və inzibati binası anbar binası. | |
| L.B.M. | | G. Musayeva | | | | İnzibati bina | Mərhələ: İ.L. / Vərəq: 11 / Vərəqlər |
| Konstruktor | | M. Əzizov | | | | | |
| Norm. nəzarət | | S. Şükürova | | | | -0.80 səviyyəsində sütunların yerləşmə planı. | "STORM BUİLDİNG" MMC |

Razılaşdırılmışdır

İnvent № | İmza və Tarix | İnvent № əvəzinə

Format A3

## Monolit d/b sütun "Ms-1"-in konstruksiyası.

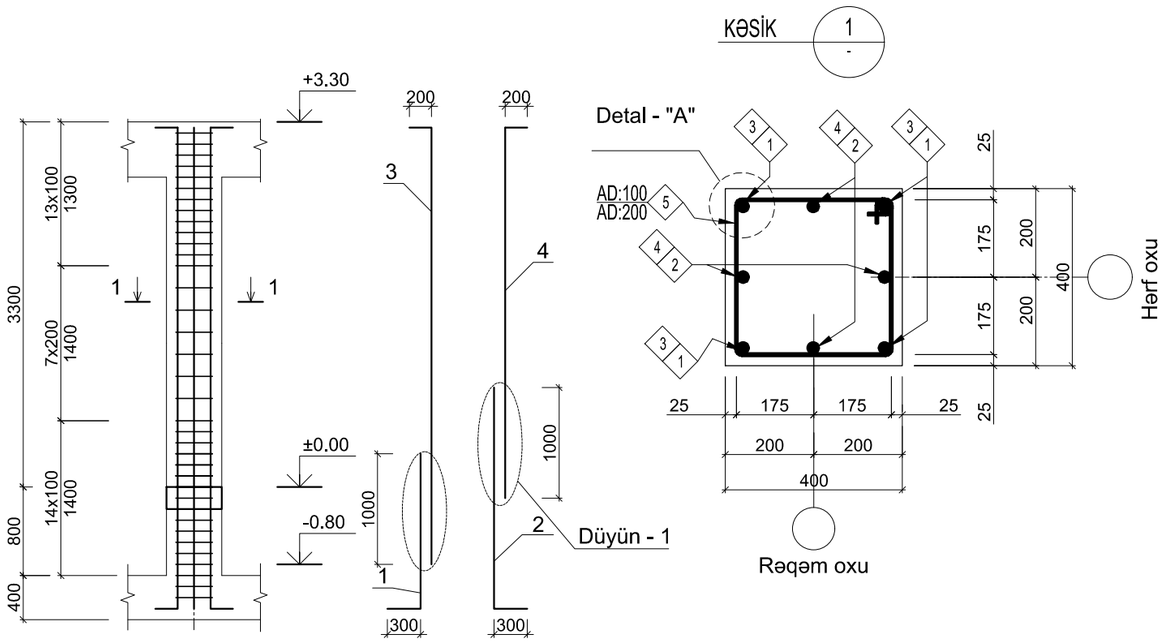


## Materialların təsnifatı. (1 ədəd üçün)

| Format | Zona | Mövqe | İşarəsi | Adı | Miq. | Qeyd |
|---|---|---|---|---|---|---|
| | | | | Monolit d/b sütun "Ms-1" | | |
| | | 1 | DÜİST 52544-2006 | Ø18 A500C , L=1700 mm | 4 | 3.4 / 13.6 |
| | | 2 | ----- // ----- | Ø18 A500C , L=2300 mm | 4 | 4.6 / 18.4 |
| | | 3 | ----- // ----- | Ø18 A500C , L=4150 mm | 4 | 8.3 / 33.2 |
| | | 4 | ----- // ----- | Ø18 A500C , L=3550 mm | 4 | 7.1 / 28.4 |
| | | 5 | DÜİST 5781-82* | Ø8A-I (A240), L=1600 mm | 34 | 0.64 / 21.8 |
| | | | | Material: Beton B25 | - | 0.6 $m^3$ |

## Polad sərfi cədvəli, kq. (18 ədəd üçün)

| Elementin markası | Armatur məmulatları | | | | | | | | | | |
|---|---|---|---|---|---|---|---|---|---|---|---|
| | Armaturun sinfi | | | | | | | | | Yekun | Beton B25 |
| | A-I A(240) | | | A500C | | | | | | | |
| | DÜİST 5781-82* | | | DÜİST 52544-2006 | | | | | | | |
| | Ø8 | Ø10 | Cəmi: | Ø12 | Ø14 | Ø16 | Ø18 | Ø20 | Ø22 | Cəmi: | |
| Monolit d/b sütun "Ms-1" | 392.4 | | 392.4 | | | | 1684.8 | | | 1684.8 | 2077.2 | 10.8 $m^3$ |

## Detalların cədvəli

| Mövqe | Eskiz |
|---|---|
| 1(2) / 3(4) | 1400 (2000) \| 300 / 3950 (3350) \| 200 |
| 5 | 430, 350, 430, 350 |

## Düyün -1

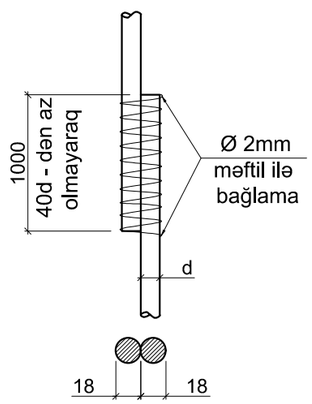


## Detal - "A"

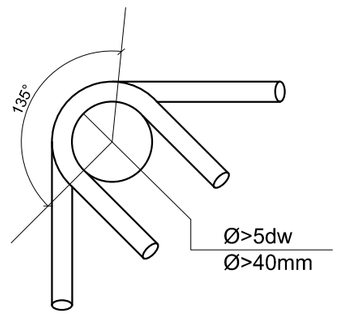


## Armaturların əyilməsi

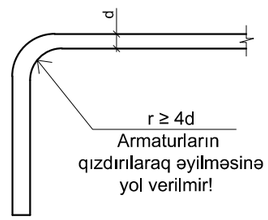


Qeyd:

1. Bu vərəq "DK - 8" vərəqi ilə birgə oxunmalıdır.

| Dəyiş | Sh.sən | Vərəq | Sən.№ | İmza | Tarix | Sifarişçi: Cəfərov Mədət İslam oğlu | DK-MK |
|---|---|---|---|---|---|---|---|
| | | | | | | Abşeron rayonu, Qobu qəsəbəsində yerləşən torpaq sahəsində tikintisi nəzərdə tutulan anbar və inzibati binası anbar binası. | |
| L.B.M. | | G. Musayeva | | | | İnzibati bina | Mərhələ: İ.L. / Vərəq: 12 / Vərəqlər |
| Konstruktor | | M. Əzizov | | | | | |
| Norm. nəzarət | | S. Şükürova | | | | Monolit d/b sütun "Ms-1"-in konstruksiyası. | "STORM BUİLDİNG" MMC |

Razılaşdırılmışdır

İnvent № Əvəzinə

İmza və Tarix

İnvent № İmza

Format A3

+3.30 səviyyəsində rigellərin yerləşmə planı.

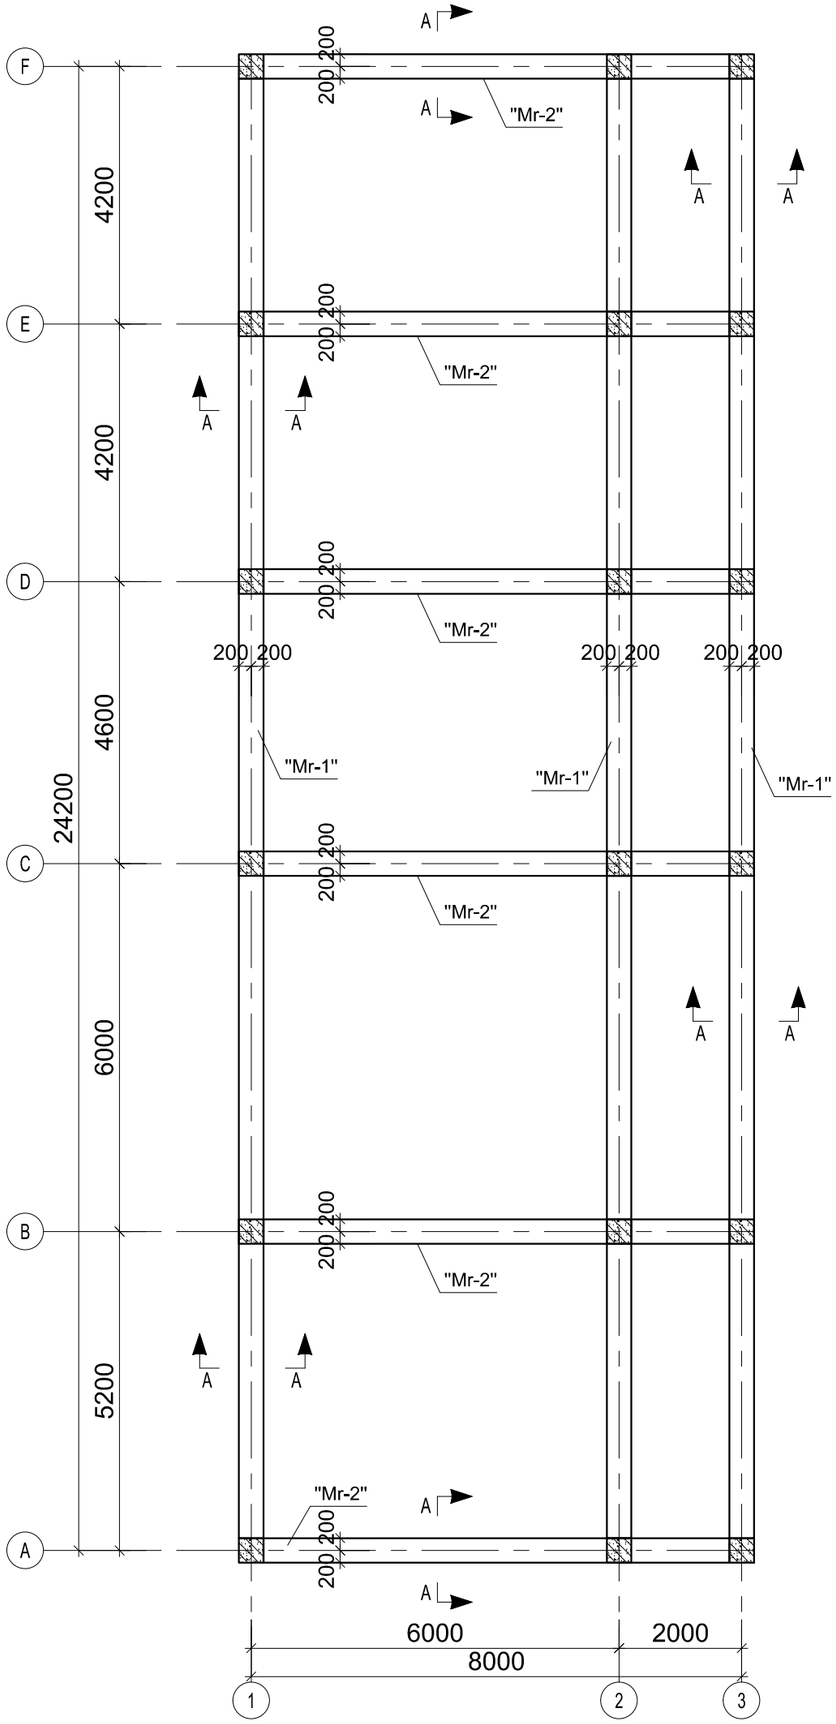


**Kəsik A-A**

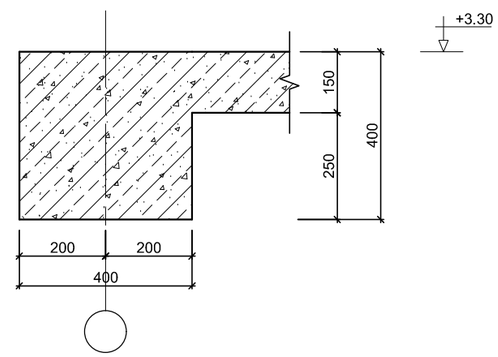


Monolit d/b elementlərin təsnifatı

| Format | Zona | Mövqe | İşarə | Adı | Miqdarı | Qeyd |
|---|---|---|---|---|---|---|
| | | | | Monolit d/b rigellər | | |
| | | | | Monolit d/b rigel Mr-1 | 3 | |
| | | | | Monolit d/b rigel Mr-2 | 6 | |

| | | | | | | | |
|---|---|---|---|---|---|---|---|
| | | | | | | Sifarişçi: Cəfərov Mədət İslam oğlu | DK-MK |
| Dəyiş | Sh.sən | Vərəq | Sən.№ | İmza | Tarix | Abşeron rayonu, Qobu qəsəbəsində yerləşən torpaq sahəsində tikintisi nəzərdə tutulan anbar və inzibati binası anbar binası. | |
| L.B.M. | | G. Musayeva | | | | İnzibati bina | Mərhələ: İ.L. / Vərəq: 13 / Vərəqlər |
| Konstruktor | | M. Əzizov | | | | | |
| Norm. nəzarət | | S. Şükürova | | | | +3.30 səviyyəsində rigellərin yerləşmə planı. | "STORM BUİLDİNG" MMC |

Razılaşdırılmışdır

İnvent № Əvəzinə

İmza və Tarix

İnvent № İmza

Format A3

## MONOLİT D/B RİGEL "MR-1"

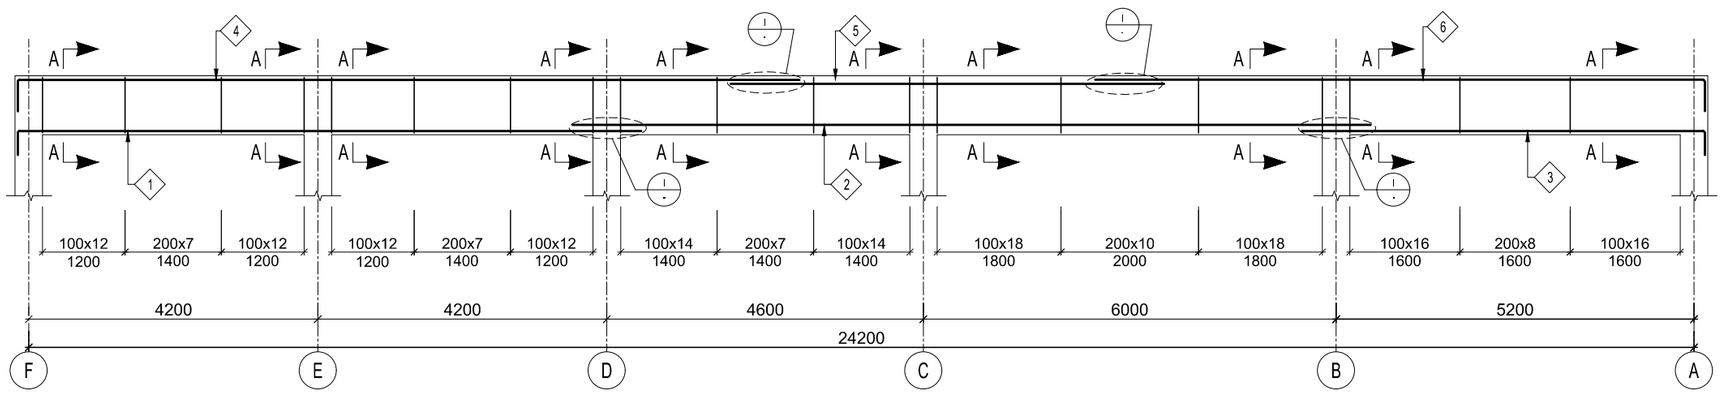


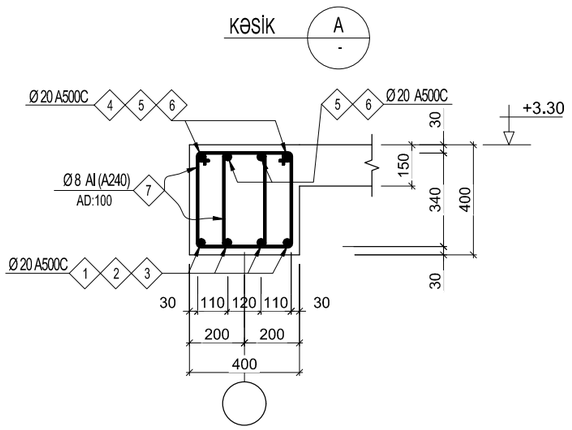


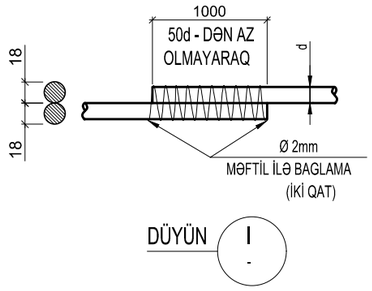


## DETALLAR CƏDVƏLİ

| MÖVQE | ESKİZ |
|---|---|
| 1(3) | 9060(5860) 400 |
| 4(6) | 11360(8860) 400 |
| 7 | 320 420 340 240 |

## MATERİALLARIN TƏSNİFATI.

| FORMAT | ZONA | MÖVQE | İŞARƏ | ADI | MİQDARI | KÜTLƏSİ ( kq ) |
|---|---|---|---|---|---|---|
| | | | | MONOLİT RİGEL "MR -1" | 1 | |
| | | 1 | DÜİST 52544-2006 | Ø18 A500C, L=9460 | 4 | 75.6 |
| | | 2 | ----- // ----- | Ø18 A500C, L=11600 | 4 | 92.7 |
| | | 3 | ----- // ----- | Ø18 A500C, L=6260 | 4 | 50.1 |
| | | 4 | ----- // ----- | Ø18 A500C, L=11760 | 4 | 94.0 |
| | | 5 | ----- // ----- | Ø18 A500C, L=6300 | 4 | 50.4 |
| | | 6 | ----- // ----- | Ø18 A500C, L=9260 | 4 | 74.0 |
| | | 7 | DÜİST 5781-82* | Ø8A-I (A240), L=1320 | 366 | 190.8 |
| | | | | MATERİAL: BETON B25 | - | 2.5 m³ |

## POLAD SƏRFİ CƏDVƏLİ , Kq.

| ELEMENTİN MARKASI | ARMATUR MƏMULATLARI | | | | | | | | ÜMUMİ SƏRF (kq) | BETON B25 |
|---|---|---|---|---|---|---|---|---|---|---|
| | ARMATURUN SİNFİ | | | | | | | | | |
| | A-I (A240) | | | A500C | | | | | | |
| | DÜİST 5781-82* | | | DÜİST 52544-2006 | | | | | | |
| | Ø6 | Ø8 | CƏMİ: | Ø16 | Ø18 | Ø20 | Ø22 | CƏMİ: | | |
| RİGEL "MR -1" (3 ƏDƏD ÜÇÜN) | - | 572.4 | 572.4 | - | 1310.4 | - | - | 1310.4 | 1882.8 | 7.5 m³ |

| | | | | | | |
|---|---|---|---|---|---|---|
| | | | | | | Sifarişçi: Cəfərov Mədət İslam oğlu — DK-MK |
| Dəyiş | Sh.sən | Vərəq | Sən.№ | İmza | Tarix | Abşeron rayonu, Qobu qəsəbəsində yerləşən torpaq sahəsində tikintisi nəzərdə tutulan anbar və inzibati binası anbar binası. |
| L.B.M. | | G. Musayeva | | | | İnzibati bina — Mərhələ: İ.L. — Vərəq: 14 — Vərəqlər: |
| Konstruktor | | M. Əzizov | | | | |
| Norm. nəzarət | | S. Şükürova | | | | MONOLİT D/B RİGEL "MR-1" KONSTRUKSİYASI — "STORM BUİLDİNG" MMC |

Razılaşdırılmışdır

İnvent № Əvəzinə

İmza və Tarix

İnvent № İmza

Format A3

MONOLİT D/B RİGEL "MR-2"

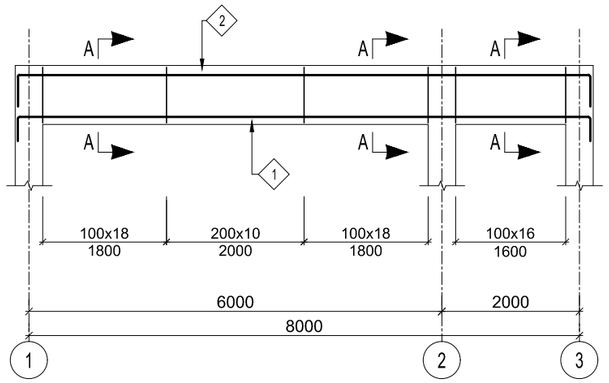


MATERİALLARIN TƏSNİFATI.

| FORMAT | ZONA | MÖVQE | İŞARƏ | ADI | MİQDARI | KÜTLƏSİ ( kq ) |
|---|---|---|---|---|---|---|
| | | | | MONOLİT RİGEL "MR -2" | 1 | |
| | | 1 | DÜİST 52544-2006 | Ø18 A500C, L=9120 | 4 | 72.9 |
| | | 2 | ----- // ----- | Ø18 A500C, L=9120 | 4 | 72.9 |
| | | 3 | DÜİST 5781-82* | Ø8A-I (A240), L=1320 | 124 | 64.7 |
| | | | | MATERİAL: BETON B25 | - | 0.84 m³ |

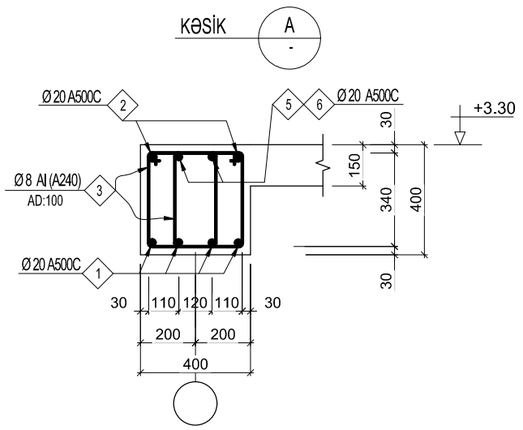


DETALLAR CƏDVƏLİ

| MÖVQE | ESKİZ |
|---|---|
| 1 | 8320<br>400<br>400 |
| 2 | 8320<br>400<br>400 |
| 3 | 320<br>420<br>340<br>240 |

POLAD SƏRFİ CƏDVƏLİ , Kq.

| ELEMENTİN MARKASI | ARMATUR MƏMULATLARI | | | | | | | | ÜMUMİ SƏRF (kq) | BETON B25 |
|---|---|---|---|---|---|---|---|---|---|---|
| | ARMATURUN SİNFİ | | | | | | | | | |
| | A-I (A240) | | | A500C | | | | | | |
| | DÜİST 5781-82* | | | DÜİST 52544-2006 | | | | | | |
| | Ø6 | Ø8 | CƏMİ: | Ø16 | Ø18 | Ø20 | Ø22 | CƏMİ: | | |
| RİGEL "MR -2" (6 ƏDƏD ÜÇÜN) | - | 388.2 | 388.2 | - | 874.8 | - | - | 874.8 | 1263.0 | 5.1 m³ |

Razlaşdırılmışdır

İnvent № Əvəzinə

İmza və Tarix

İnvent № İmza

| | | | | | | | |
|---|---|---|---|---|---|---|---|
| | | | | | | Sifarişçi: Cəfərov Mədət İslam oğlu | DK-MK |
| Dəyiş | Sh.sən | Vərəq | Sən.№ | İmza | Tarix | Abşeron rayonu, Qobu qəsəbəsində yerləşən torpaq sahəsində tikintisi nəzərdə tutulan anbar və inzibati binası anbar binası. | |
| L.B.M. | | G. Musayeva | | | | İnzibati bina | Mərhələ: İ.L. / Vərəq: 15 / Vərəqlər: |
| Konstruktor | | M. Əzizov | | | | | |
| Norm. nəzarət | | S. Şükürova | | | | MONOLİT D/B RİGEL "MR-2" KONSTRUKSİYASI | "STORM BUİLDİNG" MMC |

Format A3

+3.30 səviyyəsində monolit d\b örtüyün yerləşmə planı.

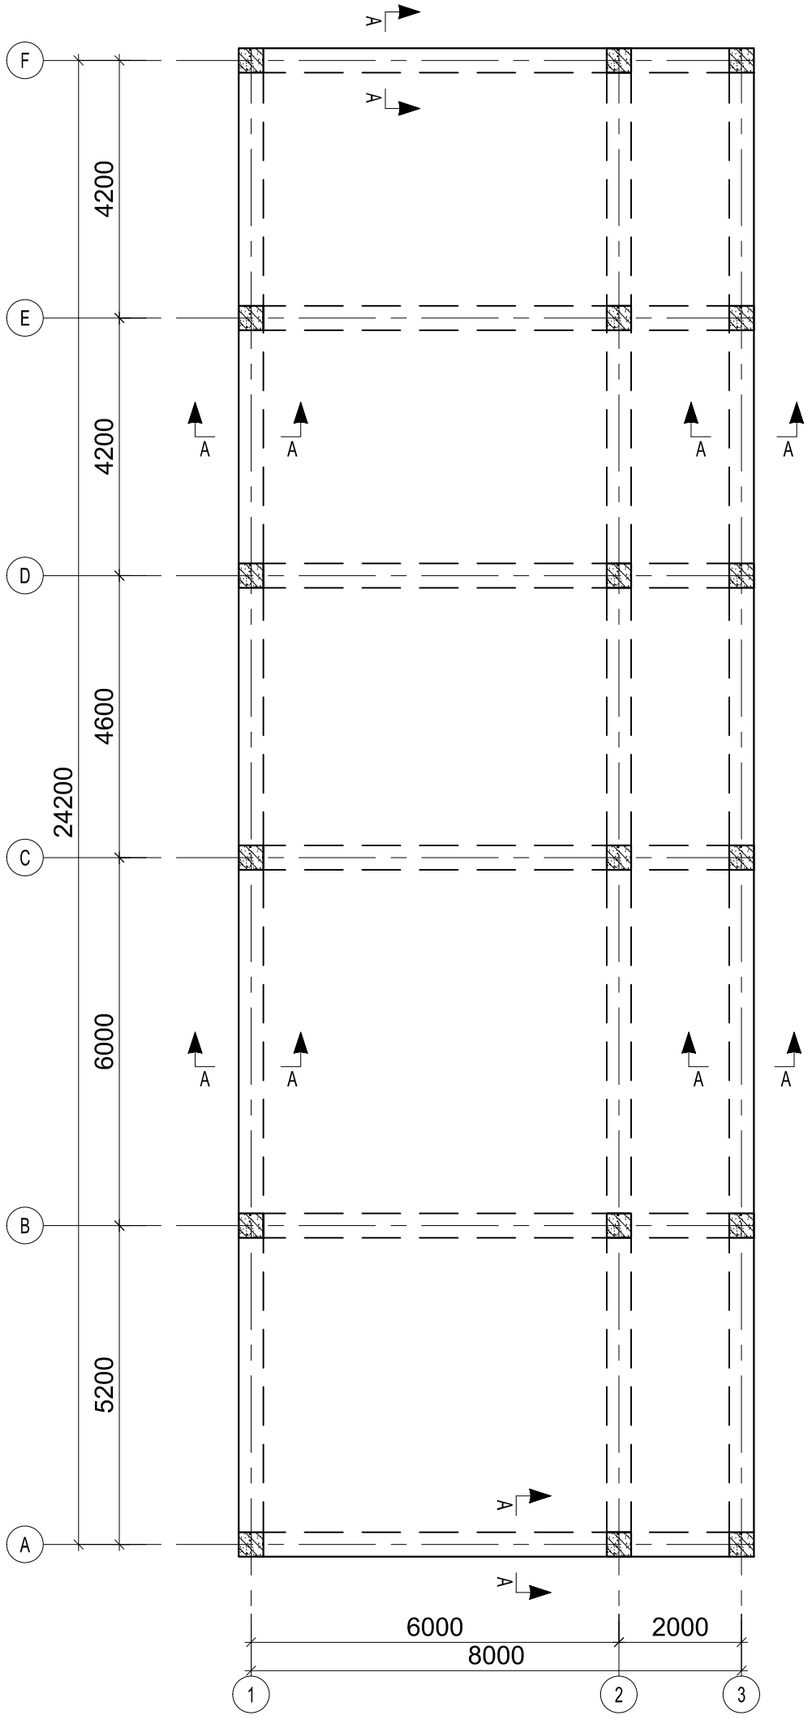


**Kəsik A-A**

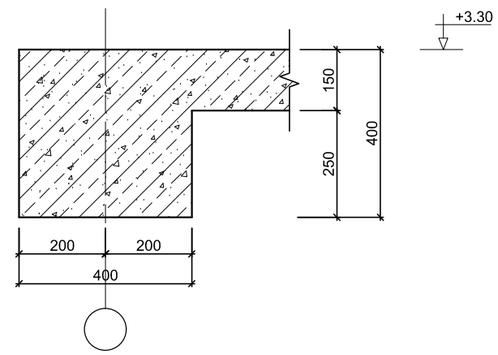


| | | | | | | | |
|---|---|---|---|---|---|---|---|
| | | | | | | Sifarişçi: Cəfərov Mədət İslam oğlu | DK-MK |
| Dəyiş | Sh.sən | Vərəq | Sən.№ | İmza | Tarix | Abşeron rayonu, Qobu qəsəbəsində yerləşən torpaq sahəsində tikintisi nəzərdə tutulan anbar və inzibati binası anbar binası. | |
| L.B.M. | | G. Musayeva | | | | İnzibati bina | Mərhələ: İ.L. / Vərəq: 16 / Vərəqlər: |
| Konstruktor | | M. Əzizov | | | | | |
| Norm. nəzarət | | S. Şükürova | | | | +3.30 səviyyəsində monolit d\b örtüyün yerləşmə planı. | "STORM BUİLDİNG" MMC |

Razılaşdırılmışdır

İnvent № Əvəzinə

İmza və Tarix

İnvent № İmza

Format A3

+3.30 səviyyəsində monolit d\b örtüyün alt torunun armaturlanması

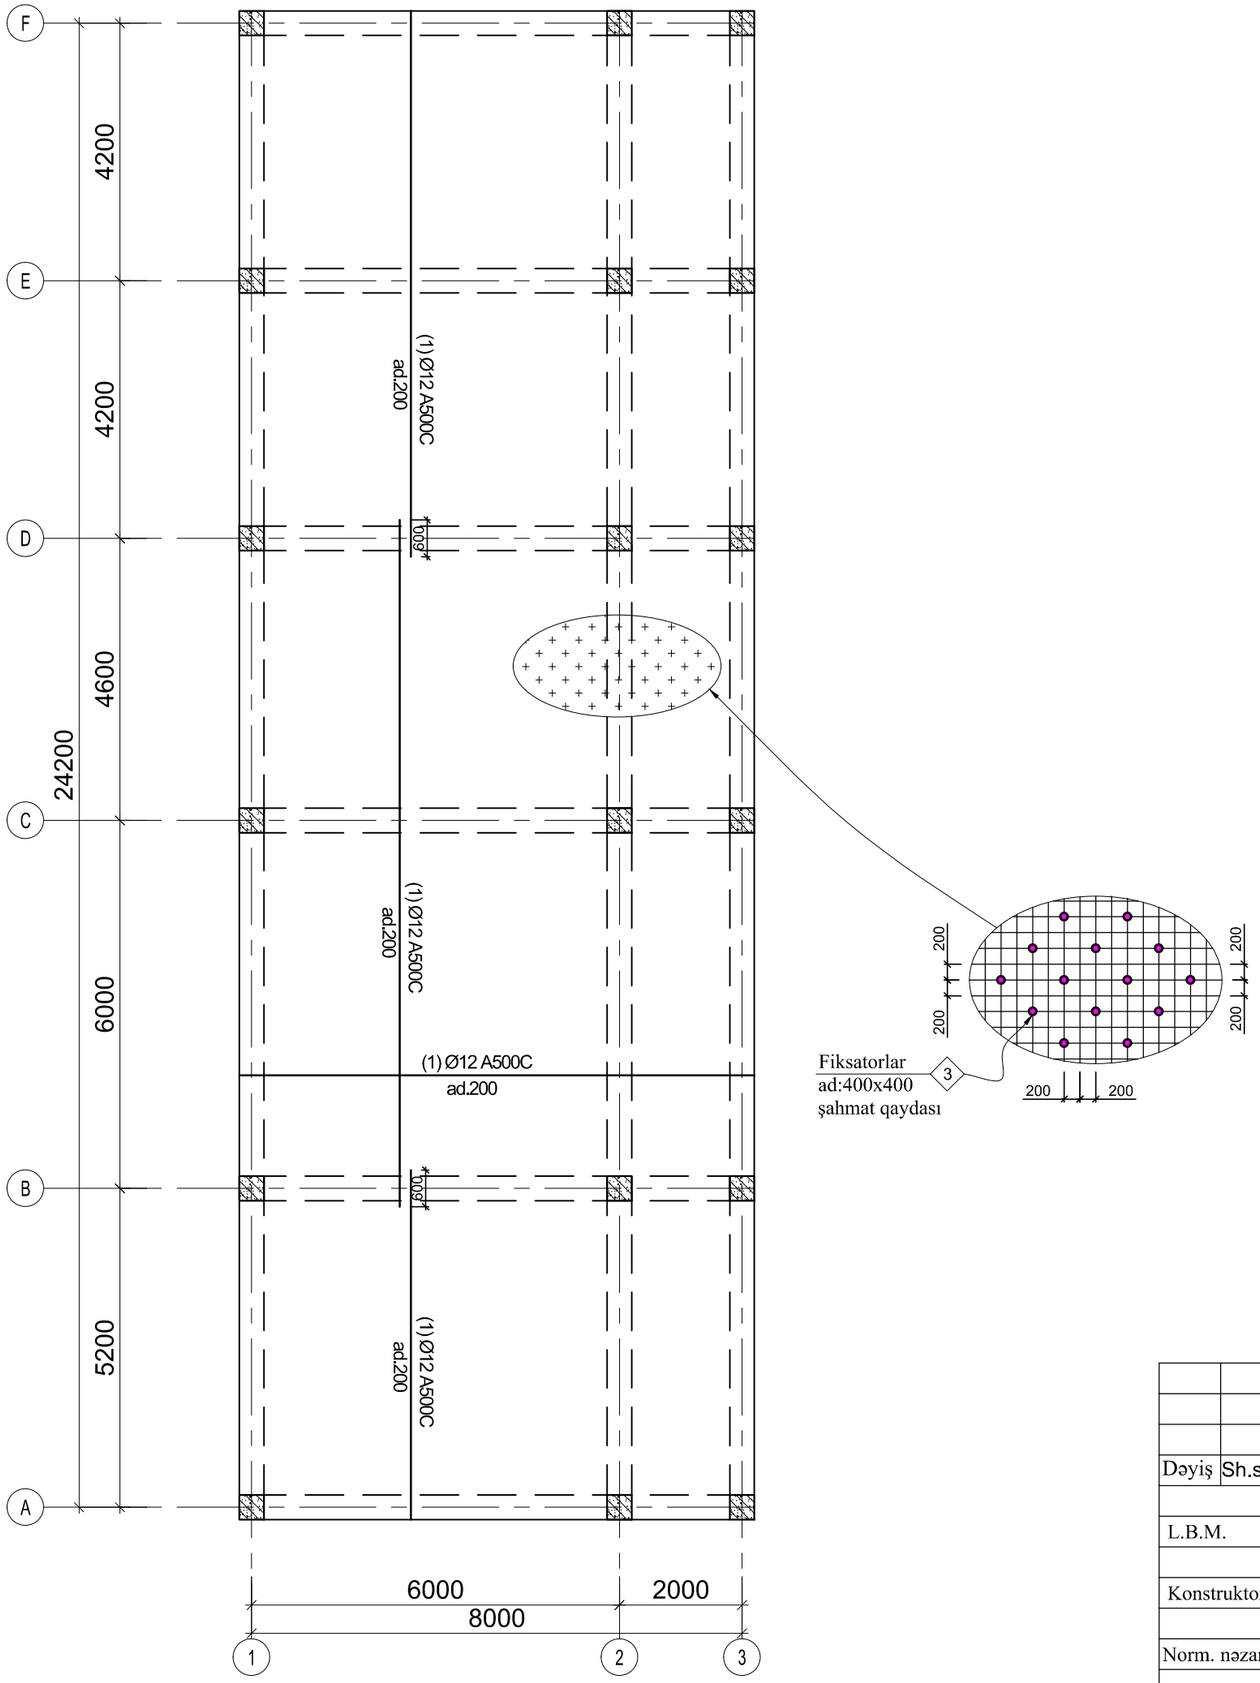


## Qeyd:

1. Monolit d/b örtük tavasında alt armaturlar dayaqda, üst armaturlar isə aşırımın ortasında bağlanmalıdır.
2. Monolit d/b örtük tavasının armaturlanması zamanı armatur millərinin calaq olunduğu hissə eyni bir düz xətt üzrə düşməməlidir.
3. Örtük tavalarında olan texnoloji dəliklərin yerləşməsi mühəndis və memarlıq cizgiləri ilə dəqiqləşdirilməlidir.

| | | | | | | | |
|---|---|---|---|---|---|---|---|
| | | | | | | Sifarişçi: Cəfərov Mədət İslam oğlu | DK-MK |
| Dəyiş | Sh.sən | Vərəq | Sən.№ | İmza | Tarix | Abşeron rayonu, Qobu qəsəbəsində yerləşən torpaq sahəsində tikintisi nəzərdə tutulan anbar və inzibati binası anbar binası. | |
| L.B.M. | | G. Musayeva | | | | İnzibati bina | Mərhələ: İ.L. / Vərəq: 17 / Vərəqlər: |
| Konstruktor | | M. Əzizov | | | | | |
| Norm. nəzarət | | S. Şükürova | | | | +3.30 səviyyəsində monolit d\b örtüyün alt torunun armaturlanması | "STORM BUİLDİNG" MMC |

Format A3

Raziləşdirilmişdir

İnvent № Əvəzinə

İmza və Tarix

İnvent № İmza

+3.30 səviyyəsində monolit d\b örtüyün üst torunun armaturlanması

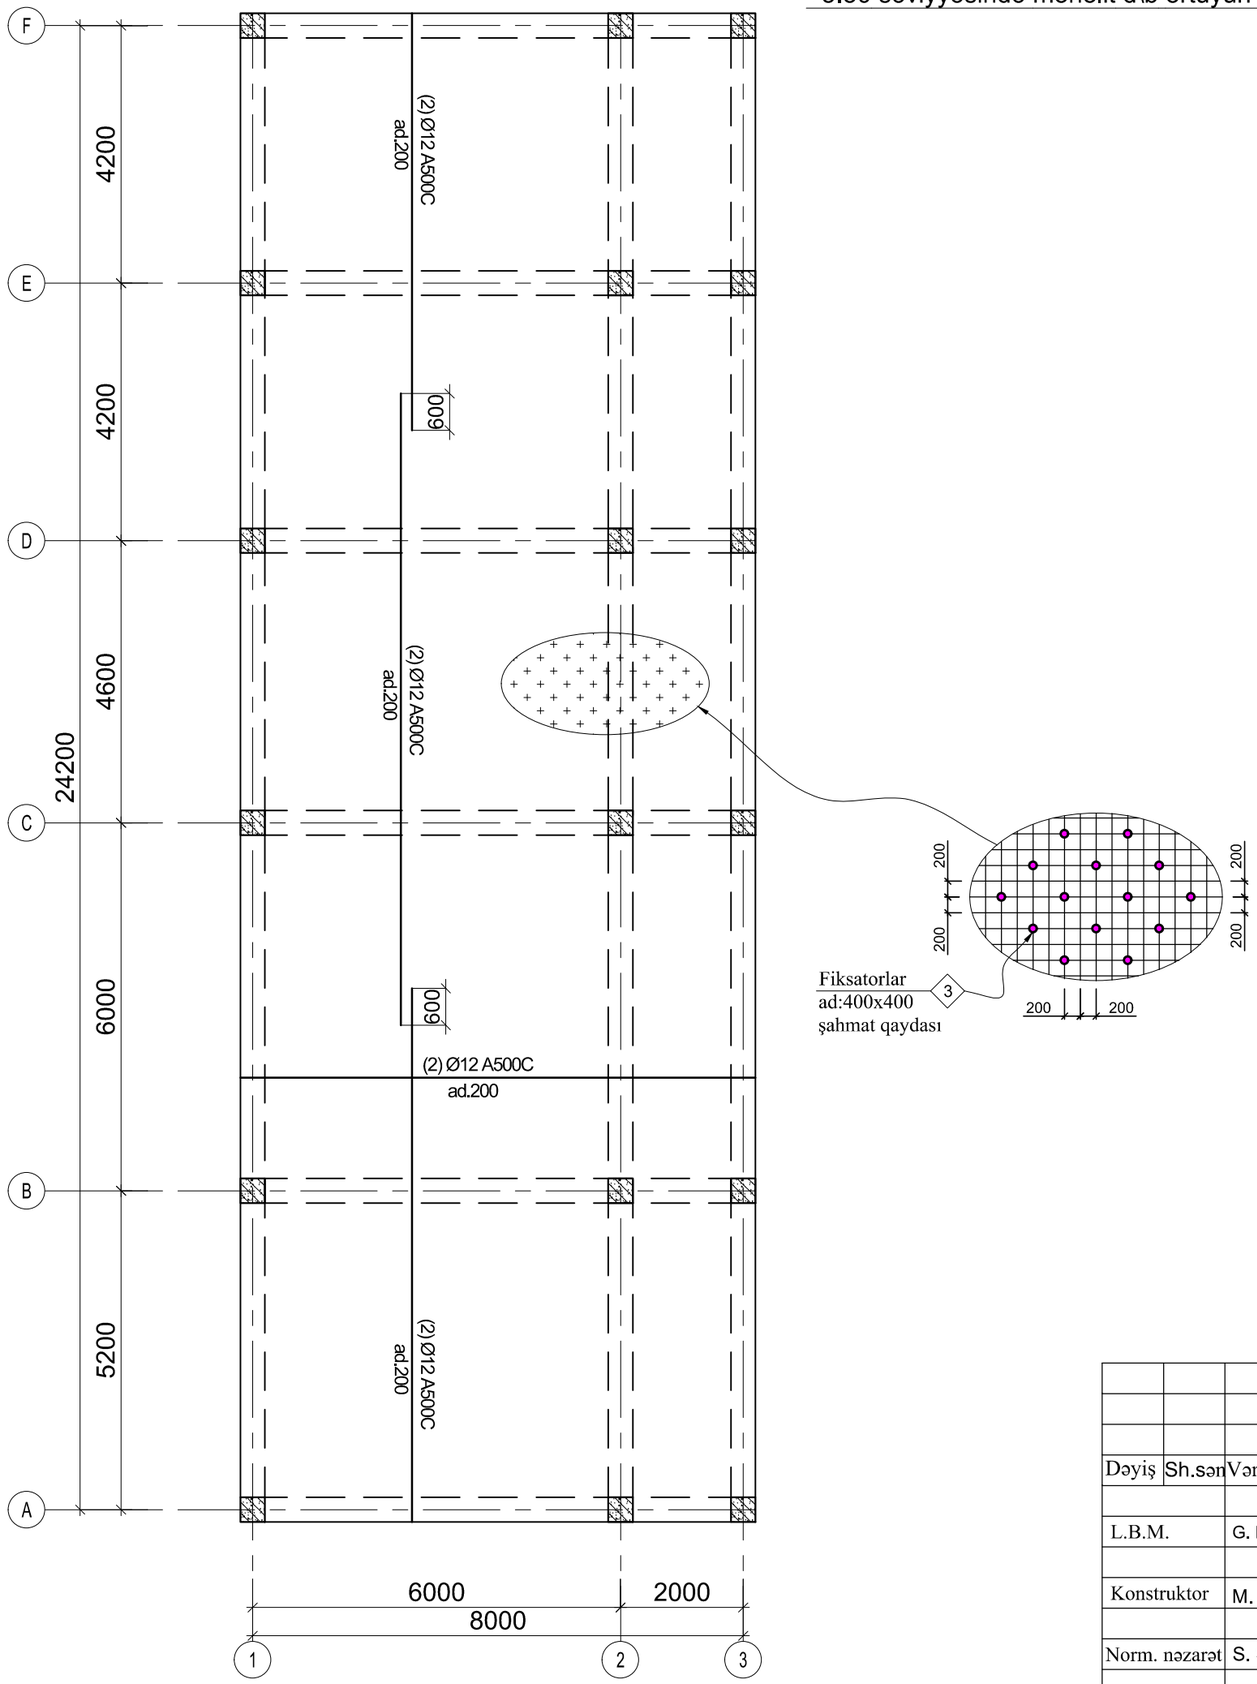


## Qeyd:

1. Monolit d/b örtük tavasında alt armaturlar dayaqda, üst armaturlar isə aşırımın ortasında bağlanmalıdır.
2. Monolit d/b örtük tavasının armaturlanması zamanı armatur millərinin calaq olunduğu hissə eyni bir düz xətt üzrə düşməməlidir.
3. Örtük tavalarında olan texnoloji dəliklərin yerləşməsi mühəndis və memarlıq cizgiləri ilə dəqiqləşdirilməlidir.

| | | | | | | | |
|---|---|---|---|---|---|---|---|
| | | | | | | Sifarişçi: Cəfərov Mədət İslam oğlu | DK-MK |
| Dəyiş | Sh.sən | Vərəq | Sən.№ | İmza | Tarix | Abşeron rayonu, Qobu qəsəbəsində yerləşən torpaq sahəsində tikintisi nəzərdə tutulan anbar və inzibati binası anbar binası. | |
| L.B.M. | | G. Musayeva | | | | İnzibati bina | Mərhələ: İ.L. / Vərəq: 18 / Vərəqlər |
| Konstruktor | | M. Əzizov | | | | | |
| Norm. nəzarət | | S. Şükürova | | | | +3.30 səviyyəsində monolit d\b örtüyün üst torunun armaturlanması | "STORM BUİLDİNG" MMC |

Razılaşdırılmışdır

İnvent № | İmza | İmza və Tarix | İnvent № əvəzinə

Format A3

**Kəsik 1-1**

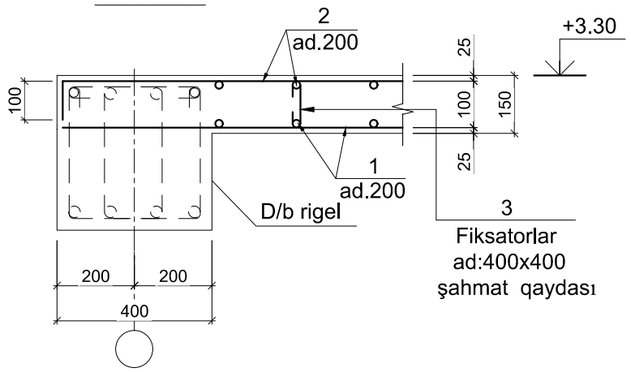


## Materialların təsnifatı

| Format | Zona | Mövqe | İşarəsi | Adı | Miq. | Qeyd |
|---|---|---|---|---|---|---|
| | | | | Monolit d/b örtük tavası | | |
| | | 1 | ГОСТ 52544-2006 | Ø12 A500C , $L_{üm}$=2170.4 pm | - | - / 1927.4 |
| | | 2 | ГОСТ 52544-2006 | Ø12 A500C , $L_{üm}$=2170.40 pm | - | - / 1927.4 |
| | | | | Xamutlar | | |
| | | 3 | DÜİST 5781-82* | Ø8 A-I (A240), L =260 mm | 1300 | 0,1 / 130.0 |
| | | | | Material: Beton B25 | - | 31.1 $m^3$ |
| | | | | | | |

## Polad sərfi cədvəli, kq.

| Elementin markası | Armatur məmulatları | | | | | | | | | |
|---|---|---|---|---|---|---|---|---|---|---|
| | Armaturun sinfi | | | | | | | | | Yekun |
| | A-I A(240) | | | A500C | | | | | | |
| | DÜİST 5781-82* | | | DÜİST 52544-2006 | | | | | | |
| | Ø8 | Ø10 | Cəmi: | | Ø12 | Ø14 | Ø18 | Ø20 | Cəmi: | |
| Monolit d/b örtük tavası | 130.0 | | 130.0 | | 3854.8 | | | | 3854.8 | 3984.8 |

## Detalların cədvəli

| Mövqe | Eskiz |
|---|---|
| 3 | 80 / 80 ) 100 |

**Qeyd:**

1. Monolit d/b örtük tavasında alt armaturlar dayaqda, üst armaturlar isə aşırımın ortasında bağlanmalıdır.
2. Monolit d/b örtük tavasının armaturlanması zamanı armatur millərinin calaq olunduğu hissə eyni bir düz xətt üzrə düşməməlidir.
3. Örtük tavalarında olan texnoloji dəliklərin yerləşməsi mühəndis və memarlıq cizgiləri ilə dəqiqləşdirilməlidir.

| Dəyiş | Sh.sən | Vərəq | Sən.№ | İmza | Tarix |
|---|---|---|---|---|---|
| L.B.M. | | G. Musayeva | | | |
| Konstruktor | | M. Əzizov | | | |
| Norm. nəzarət | | S. Şükürova | | | |

Sifarişçi: Cəfərov Mədət İslam oğlu — DK-MK

Abşeron rayonu, Qobu qəsəbəsində yerləşən torpaq sahəsində tikintisi nəzərdə tutulan anbar və inzibati binası anbar binası.

İnzibati bina

| Mərhələ | Vərəq | Vərəqlər |
|---|---|---|
| İ.L. | 19 | |

"+3,300" Səviyyəsində monolit d/b örtük üçün material təsnifatı cədvəli

"STORM BUİLDİNG" MMC

Razılaşdırılmışdır | İnvent № Əvəzinə | İmza və Tarix | İnvent № İmza

Format A3

# DAMDA ÇATI ELEMENTLƏRİNİN YERLƏŞMƏ PLANI

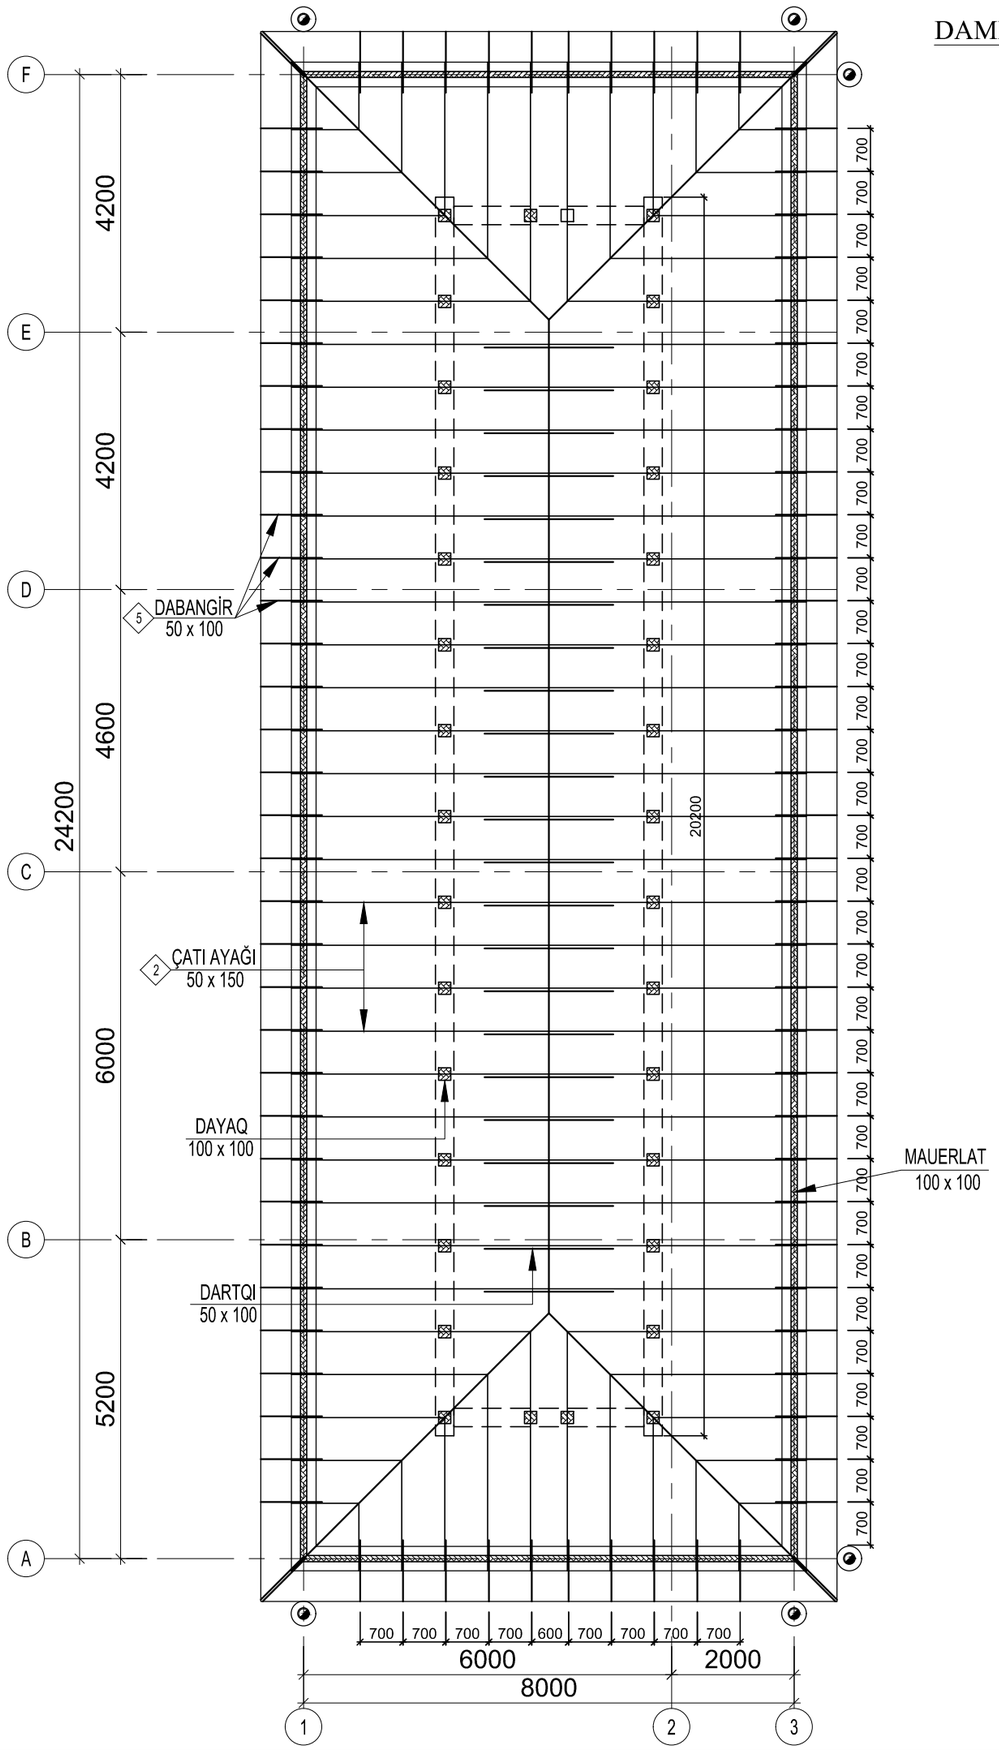


| | | | | | | | |
|---|---|---|---|---|---|---|---|
| | | | | | | Sifarişçi: Cəfərov Mədət İslam oğlu | DK-MK |
| Dəyiş | Sh.sən | Vərəq | Sən.№ | İmza | Tarix | Abşeron rayonu, Qobu qəsəbəsində yerləşən torpaq sahəsində tikintisi nəzərdə tutulan anbar və inzibati binası anbar binası. | |
| L.B.M. | | G. Musayeva | | | | İnzibati bina | Mərhələ: İ.L. / Vərəq: 20 / Vərəqlər |
| Konstruktor | | M. Əzizov | | | | | |
| Norm. nəzarət | | S. Şükürova | | | | DAMDA ÇATI ELEMENTLƏRİNİN YERLƏŞMƏ PLANI | "STORM BUİLDİNG" MMC |

Razılaşdırılmışdır

İnvent № Əvəzinə

İmza və Tarix

İnvent № İmza

Format A3

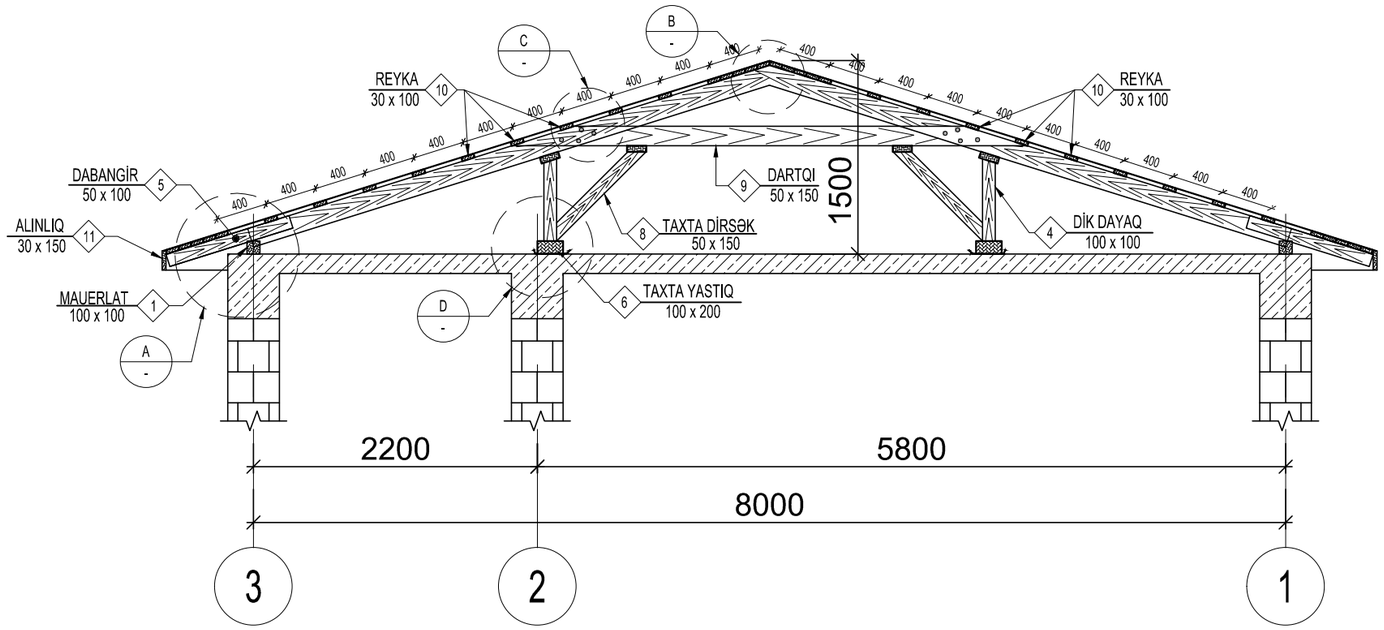


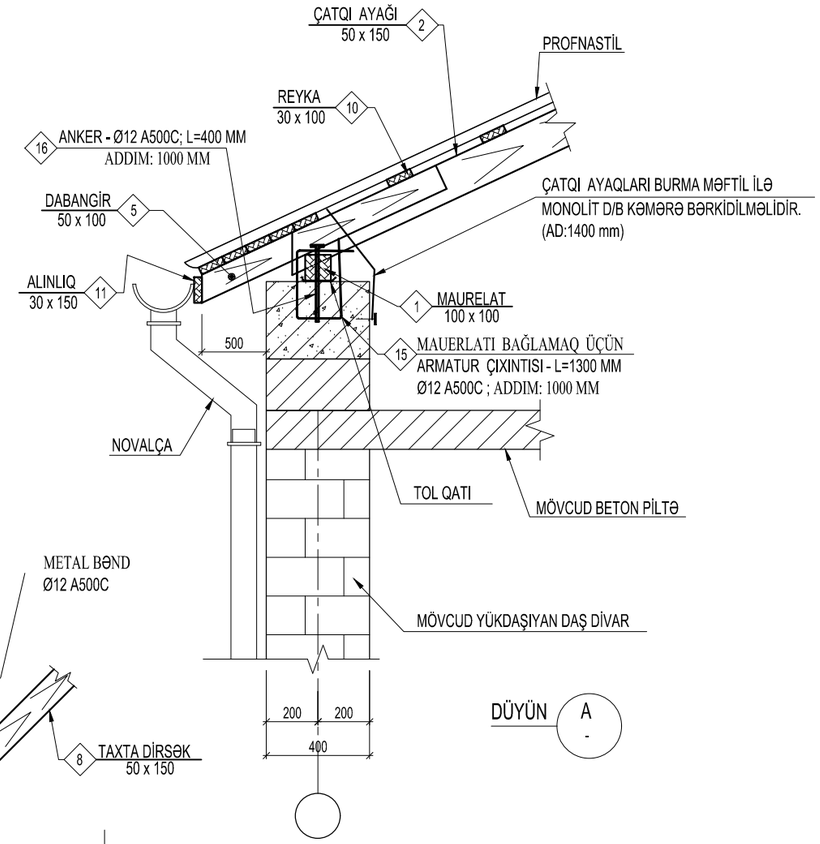


DÜYÜN A -

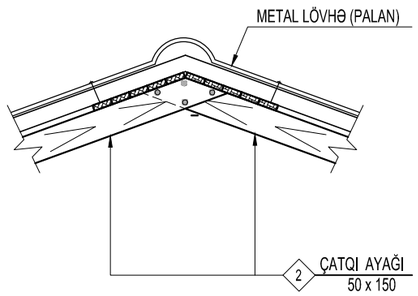


DÜYÜN B -

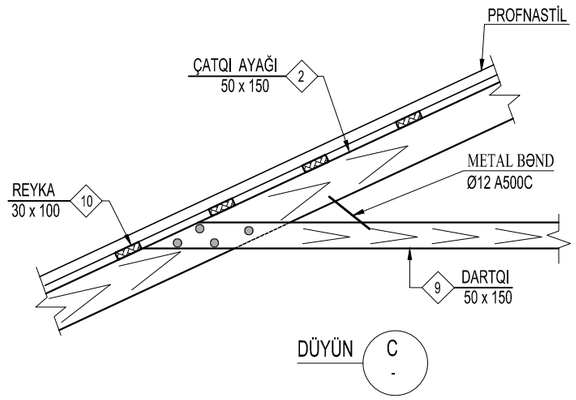


DÜYÜN C -

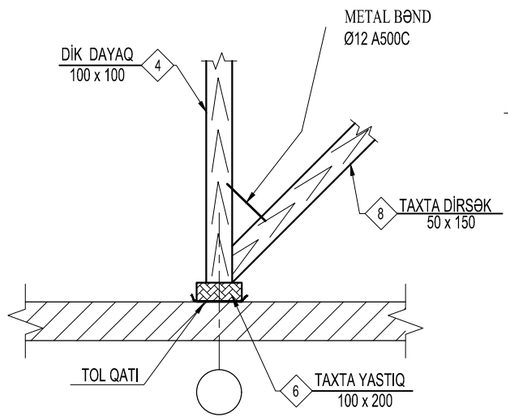


DÜYÜN D -

| | | | | | | | |
|---|---|---|---|---|---|---|---|
| | | | | | | Sifarişçi: Cəfərov Mədət İslam oğlu | DK-MK |
| Dəyiş | Sh.sən | Vərəq | Sən.№ | İmza | Tarix | Abşeron rayonu, Qobu qəsəbəsində yerləşən torpaq sahəsində tikintisi nəzərdə tutulan anbar və inzibati binası anbar binası. | |
| L.B.M. | | G. Musayeva | | | | İnzibati bina | Mərhələ: İ.L. / Vərəq: 21 / Vərəqlər: |
| Konstruktor | | M. Əzizov | | | | | |
| Norm. nəzarət | | S. Şükürova | | | | KƏSİK "1" | "STORM BUİLDİNG" MMC |

Razılaşdırılmışdır

İnvent № Əvəzinə

İmza və Tarix

İnvent № İmza

Format A3

## AĞAC ELEMENTLƏRİNİN TƏSNİFATI.

| ELEMENTİN MARKASI | ELEMENTİN ADI | ÖLÇÜSÜ: (MM) | | | SAYI: (ƏD) | ÜMUMİ UZUNLUĞU (M) | HƏCMİ: ($M^3$) | |
|---|---|---|---|---|---|---|---|---|
| | | ENİ | HÜN. | UZUNU | | | 1-ELEMENT ÜÇÜN | ÜMUMİ |
| 1 | MAUERLAT | 100 | 100 | 64.4 p.m | - | - | - | 0.644 |
| 2 | ÇATI AYAĞI | 50 | 150 | 285.0 p.m | - | - | - | 2.14 |
| 3 | ÇƏP ÇATI AYAĞI | 50 | 150 | 26.0 p.m | - | - | - | 0.195 |
| 4 | DİK DAYAQ | 100 | 100 | 22.7 p.m | - | - | - | 0.23 |
| 5 | DABANGİR | 50 | 100 | 94.0 p.m | - | - | - | 0.47 |
| 6 | TAXTA YASTIQ | 100 | 200 | 46.6 p.m | - | - | - | 0.932 |
| 7 | YƏHƏR TİRİ | 50 | 150 | 78.4 p.m | - | - | - | 0.588 |
| 8 | TAXTA DİRSƏK | 50 | 150 | 30.0 p.m | - | - | - | 0.225 |
| 9 | DARTQI | 50 | 150 | 69.0 p.m | - | - | - | 0.52 |
| 10 | REYKA | 30 | 100 | 708.0 p.m | - | - | - | 2.124 |
| 11 | ALINLIQ | 30 | 100 | 70 p.m | - | - | - | 0.21 |
| | AĞAC ELEMENTLƏRİNİN ÜMUMİ CƏMİ | | | | | | | 8.3 ($M^3$) |
| 12 | MAUERLATI BAĞLAMAQ ÜÇÜN ARMATUR | - | - | Ø12 A500C, L=1300 | 65 əd. | | 1.2 kq | 78 kq |
| 13 | ANKER ARMATUR | - | - | Ø12 A500C, L=400 | 65 əd. | | 0.4 kq | 26 kq |
| | PROFNASTİL - 260.0 $m^2$ | | | | | | | |
| | METAL LÖVHƏ (PALAN) - 42.2 p.m | | | | | | | |
| | SU AXIDAN BORU- Ø100 | | | | 21.8p.m | | | |
| | SU AXIDAN QIF- Ø150 | | | | 6 | | | |
| | SU APARAN NOV- Ø100 | | | | 70.0 p.m | | | |

Razılaşdırılmışdır

İnvent № Əvəzinə

İmza və Tarix

İnvent № İmza

| Dəyiş | Sh.sən | Vərəq | Sən.№ | İmza | Tarix |
|---|---|---|---|---|---|
| L.B.M. | | G. Musayeva | | | |
| Konstruktor | | M. Əzizov | | | |
| Norm. nəzarət | | S. Şükürova | | | |

Sifarişçi: Cəfərov Mədət İslam oğlu — DK-MK

Abşeron rayonu, Qobu qəsəbəsində yerləşən torpaq sahəsində tikintisi nəzərdə tutulan anbar və inzibati binası anbar binası.

| İnzibati bina | Mərhələ | Vərəq | Vərəqlər |
|---|---|---|---|
| | İ.L. | 22 | |

DAMDA ÇATI ELEMENTLƏRİNİN MATERİAL SƏRFİ

"STORM BUİLDİNG" MMC

Format A3